

■ 피지컬 AI리빙센터 구축 공사

건축 기계설비공사

2026.07



한국폴리텍대학
신기술교육원

■ 피지컬 AI리빙센터 구축 공사

건축공사

2026.07.



한국폴리텍대학
신기술교육원

도면번호	도면명	축척	비고
도면목록표			
A - 100	표지	1/150	
A - 101	도면목록표1	1/150	
A - 102	설계설명서 공사범위	1/150	
A - 103	공 정 표	1/150	
A - 104	공사개요	1/150	
A - 105	배 치 도	1/600	
A - 200	변경후 1층 평면도	1/250	
A - 201	변경후 1층 확대 평면도	1/150	
A - 202	데이터센터 스마트팜확대 평면도	1/60	
A - 203	변경후 종단면도1	1/100	
A - 204	변경후 종단면도2	1/100	
A - 205	변경후 횡단면도	1/200	
A - 206	스마트팜 창호도	1/80	
A - 207	창호상세도1	1/5	
A - 208	창호상세도2	1/20	
A - 209	창호 상세도3	1/80	
A - 210	기존 1층 평면도	1/250	
A - 211	기존 1층 창호도	1/150	
A - 212	기존 창호도1	1/120	
A - 213	기존 창호도1	1/120	
A - 214	경량벽체 상세도1	1/100	
A - 300	변경후 3층평면도	1/400	
A - 301	변경후 3층 확대평면도	1/50	
A - 302	휴게실 창호도	1/80	
A - 303	기존 3층평면도	1/400	
A - 304	기존 3층 확대평면도	1/50	
A - 400	변경후 4층평면도	1/350	
A - 401	변경후 4층 확대 평면도	1/150	
A - 402	변경 전후 횡단면도	1/200	
A - 403	경량벽체 상세도2	1/100	
A - 404	실습실2 창호도	1/80	
A - 405	기존 4층평면도	1/350	
A - 406	기존 4층 확대 평면도	1/150	

[illegible][illegible]

설계 설명서 및 공사 범위

사업 개요

- 기존 시설의 개보수 및 리모델링을 통한 피지컬 시리빙센터 및 요소기술 강의실등 시설 구축
- 피지컬 AI 기술확산 및 인력양성을 위한 리빙센터 공간 구축으로 교육환경 개선 및 안전성 확보

공사방향

- 피지컬 AI 기술확산 및 인력양성을 위한 리빙센터 공간 구축위한 시설 설치로 기능성 안전성 경제성 미관적 요소등을 전체적으로 검토 시공
- 기존 건축물(사용중)에 공사를 하는 관계로 시공시 분야별 체크리스트를 작성 운영한다

해체 및 시설공사

- 가설공사
- 철거공사 - 기존 벽체 및 도어,마감재(천정 벽 바닥),설비시설
- 시설공사 - 설계도서 및 내역서 참조

건설 일반폐기물 운반 및 처리

- 건설 혼합 생활폐기물 운반 및 처리(5톤이상 반출시 사전신고)

기타사항

1. 철거계획서,폐기물처리 신고(관련기관),철거관련 인 허가사항,예정공정표 작성 및 시공시 인접 건축물 및 시설(포장마감,조경수등) 훼손이 없도록 시공 및 관리
2. 산소용접기 작업시 화재 예방을 위한 작업전 안전 조치를하며 현장내 작업장별로 소화기 배치(또는 소방법에 준한 배치) 및 작업자와 별도 안전요원(소화기 휴대)배치
3. 장비 이용 작업시 낙하물 및 추락방지 대책 및 신호수 배치 해야하며 비탈면과 연결된 건물 철거시 경사면에 대하여 안전조치 한다
4. 통행인 및 통행차량에 대한 안전조치후 시공 및 안내판설치
5. 철거자재는 우천시 오염수 우수관유입방지 ,악취 ,철거재 비산,안전사고등 고려 보호 덮개 또는 즉시 반출조치한다(공사시 배풍시설(필터내장형) 설치 운영)
6. 철거공사 주변 정리 정돈 및 주변 오염부분 제거를 한다
7. 시공사는 작업전 감독에게 작업인원 보고 및 안전교육실시 안전장구 착용
8. 철거전 행정절차 이행후 시공하며 인접부지등에 비산먼지 및 소음,진동등에 관한 안전 및 방지계획서 제출
9. 철거전 가스,전기,수도등 공공시설등에 대하여 공급업체와 사전 협의 및 안전 보호 조치한다.
10. 공사중 민원 및 안전사고 발생시 즉시 공사 중단후 안전조치,발주청에 보고하여야하며,철거건축물 인근인접주택 보호를 위한 보호 가설공사 조치후 시공한다
11. 철거전 현장 답사 조사 결과 및 현장 규격 위치 실측후 결과를 감독관에 제출후 공사에 착수한다
12. 엑폭시 바닥 마감재 시공전 로봇 이동 및 스마트팜 미끄럼에 대한 검토후 마감 표면상태 시공계획을 수립한다
13. 데이터 센터는 소음 차단 및 향온향습설비 , 스마트팜은 실내 온 습도 유지가 되도록 시공한다(자재등 사전 검토 및 감독관 협의후 시공)

PROJECT TITLE



피지컬 시리빙센터 구축 공사

Date.

No. Revision

-

-

-

-

-

-

-

-

-

-

-

-

-

NOTE

Structure


Mechanical

Electrical

Fire Protection

Civil

Landscape

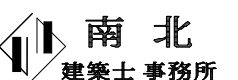

建築士 鄭 範 洙

전북 전주시 완산구 서신로57 7층

TEL : 063)247-7787

FAX : 063)247-7786

E-MAIL : nba2007@daum.net

SHEET TITLE

설계설명서 공사범위

DESIGN BY

SCALE

A3 1/150

CHECKED BY

DATE

APPROVED BY

SHEET NO.

SERIAL NO.

A- 102

피지컬 AI리빙센터 구축 공사

소요일수 : 50 일 (공휴일/우천일 포함)

[illegible]

일 일	1							2										
	4	8	12	16	20	25	30	34	38	42	46	50						
	가설공사 철거 공사(일반 폐기물) 조적 창호공사 폐기물 반출 운반 현장 정리 정돈-청소 수장 공사 설비 공사																	



피지컬 AI리빙센터 구축 공사

[illegible]

NOTE

Structure


Mechanical

Electrical

Fire Protection

Civil

Landscape

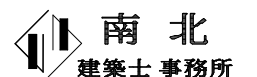

建築士 鄭 範 洙

전북 전주시 완산구 서신로57 7층
TEL : 063)247-7787
FAX : 063)247-7786
E-MAIL : nba2007@daum.net

SHEET TITLE

공 정 표

DESIGN BY	SCALE
	A3 1/150

APPROVED BY	SHEET NO.
-------------	-----------

SERIAL NO.	A-103
------------	-------

공사현장

장소 : 전주시 덕진구 유상로 20

공사개요

층	실명	면적m2	비고
1	스마트팜	30.9	신설
1	데이터센터	16.22	신설
1	유틸리티룸	13.11	신설
1	기존 시설 보완	620.17	벽체 천정 도장,스크린설치,벽체 도어설치
1층 소계	1층	680.4	금회공사부분
3	휴게실	50.29	기존시설보완
3층소계	1층	50.29	금회공사부분
4	실습실1	113.15	벽체 이설 보완사업
4	실습실2	127.75	실습 가벽 조성
4층소계	1층	240.9	금회공사부분
공사면적계		971.59	

PROJECT TITLE



피지컬 시리빙센터 구축 공사

Date.

No. Revision

-

-

-

-

-

-

-

-

-

-

-

NOTE

Structure


Mechanical

Electrical

Fire Protection

Civil

Landscape

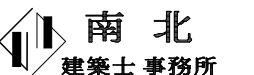

建築士 鄭 範 洙

전북 전주시 완산구 서신로57 7층

TEL : 063)247-7787

FAX : 063)247-7786

E-MAIL : nba2007@daum.net

SHEET TITLE

공사개요

DESIGN BY

SCALE

A3 1/150

CHECKED BY


DATE

APPROVED BY

SHEET NO.

SERIAL NO.

A- 104

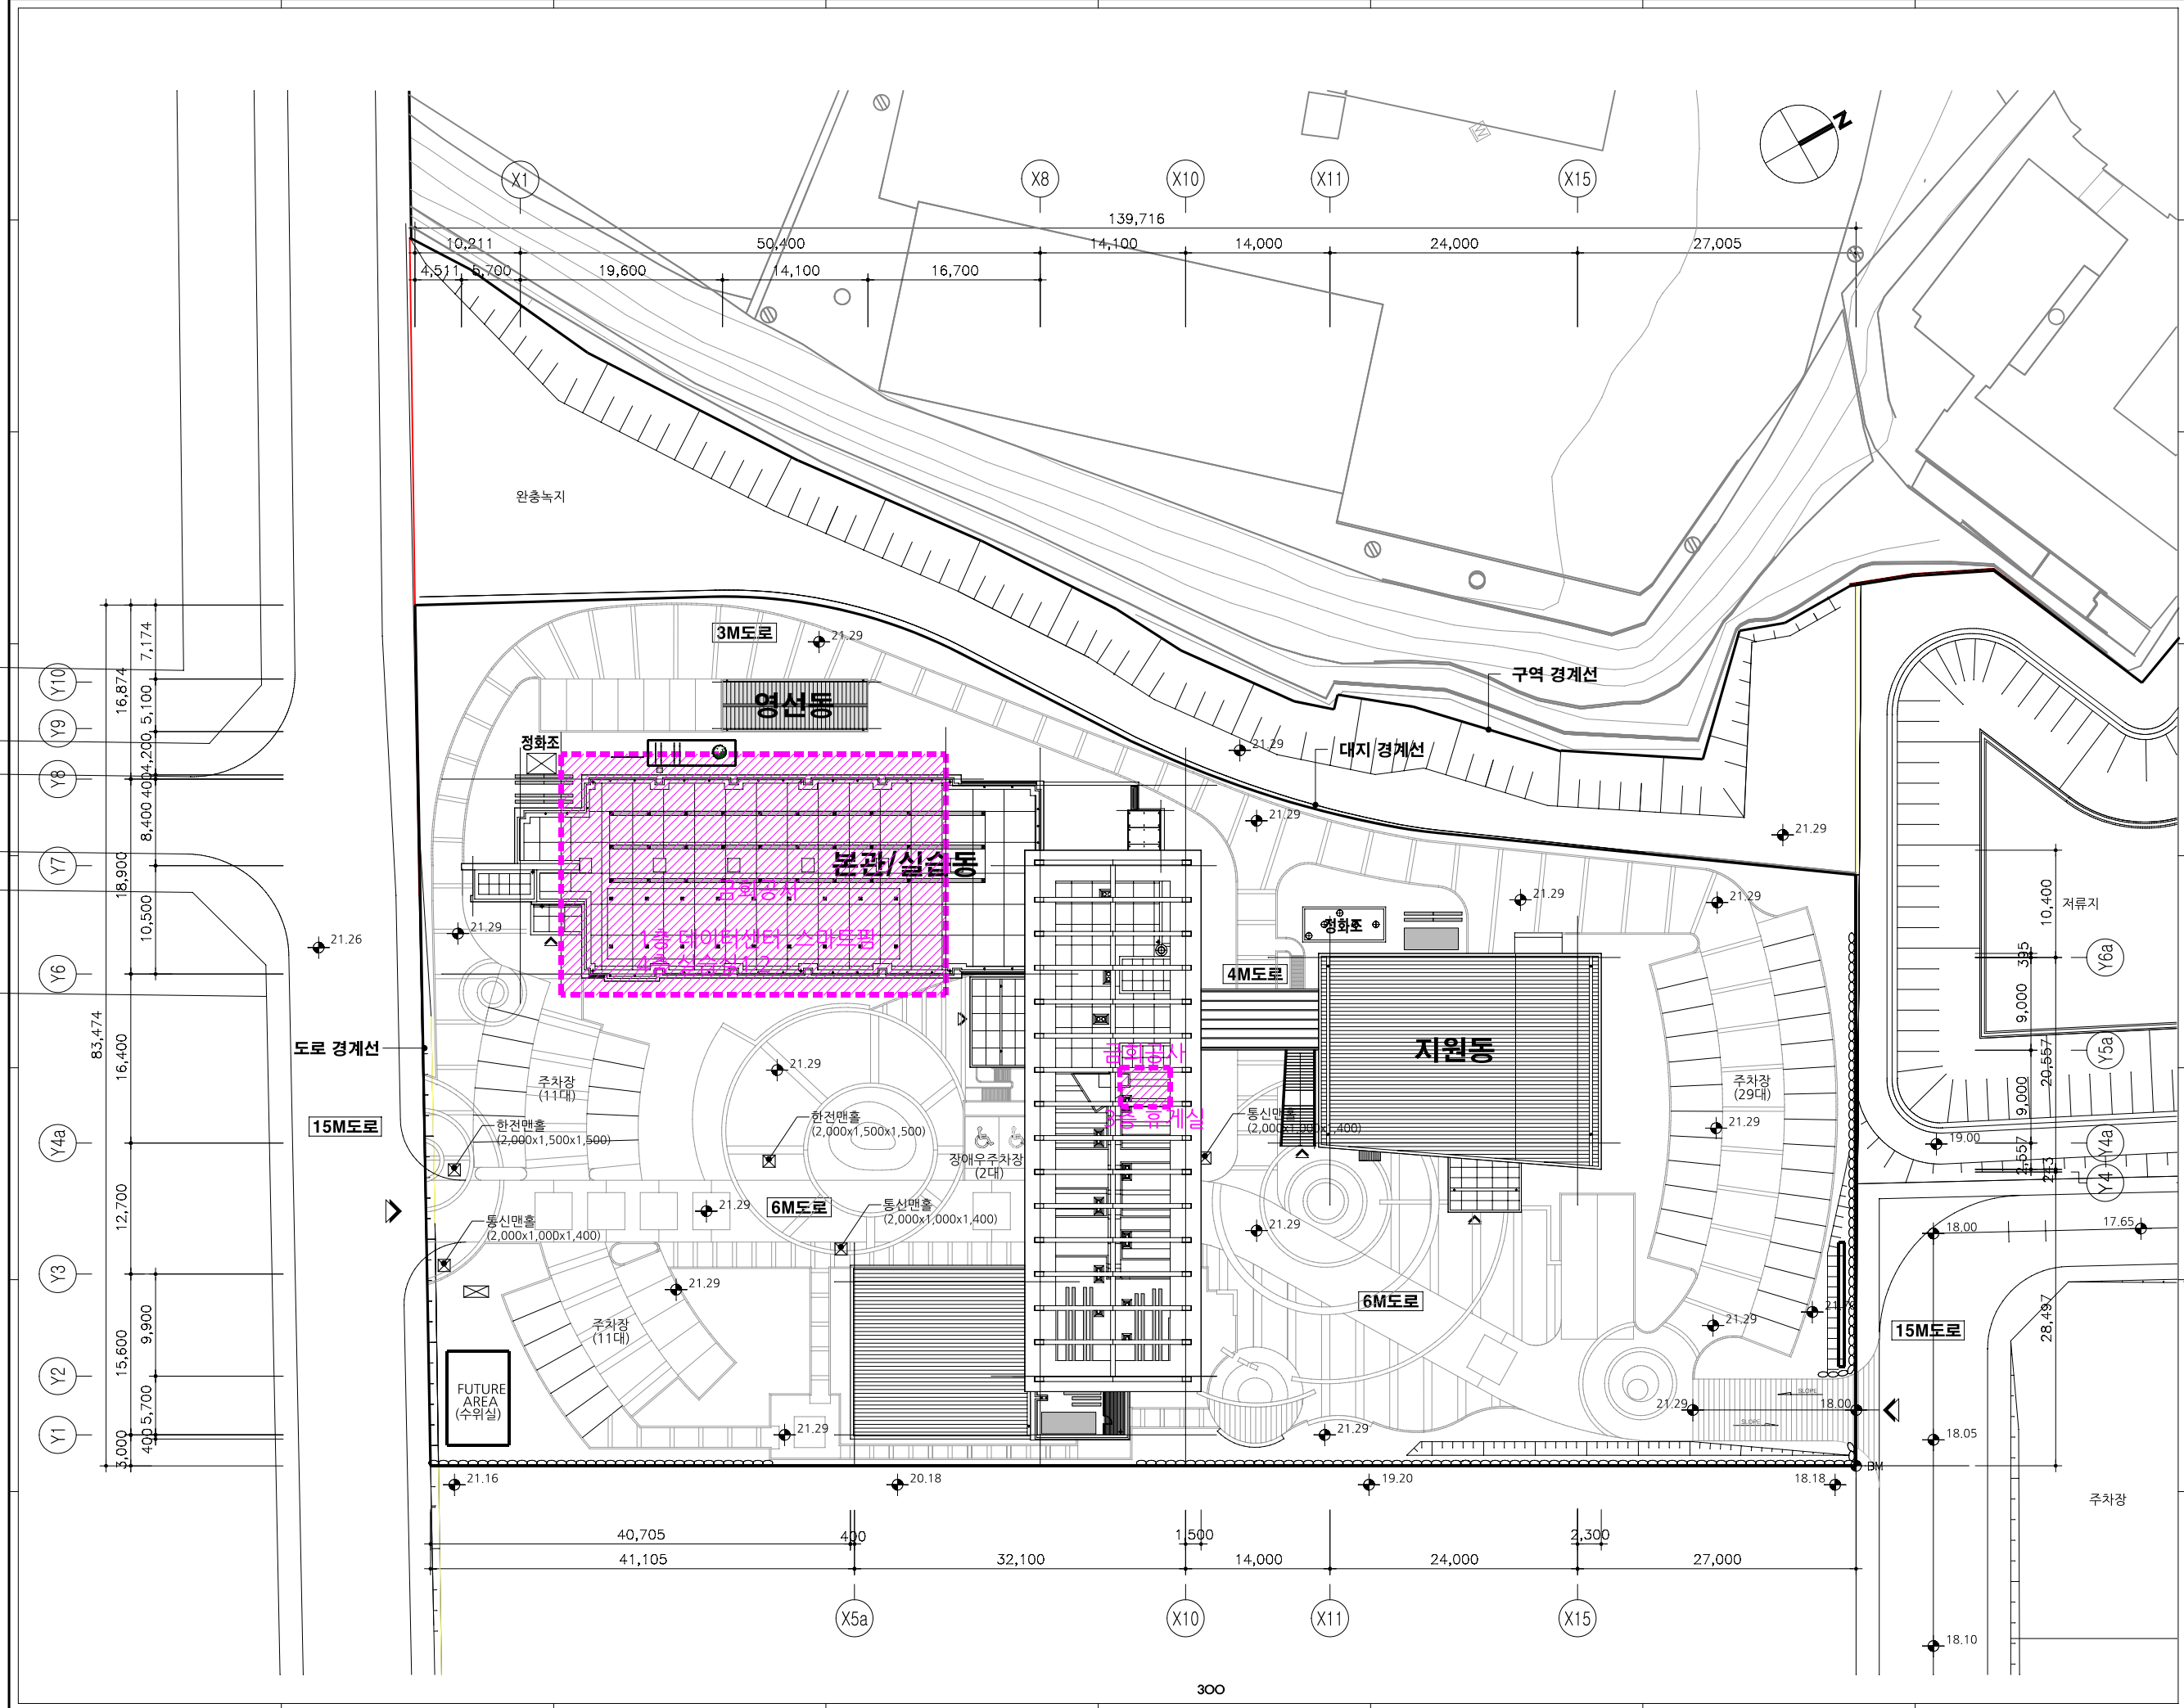



PROJECT TITLE

피지컬 시리빙센터 구축 공사

Date.

No.	Revision
-	-
-	-
-	-
-	-
-	-
-	-
-	-
-	-
-	-
-	-

NOTE

Structure

Mechanical

Electrical

Fire Protection

Civil

Landscape



南北
建築士事務所

建築士 鄭 範 洙

전북 전주시 완산구 서신로57 7층
TEL : 063)247-7787
FAX : 063)247-7786
E-MAIL : nba2007@daum.net

SHEET TITLE

배 치 도

DESIGN BY	SCALE A3 1/600
CHECKED BY	DATE
APPROVED BY	SHEET NO.
SERIAL NO.	A- 105



이동식 웬스(이미지 사진)



1층 공사 범위표

1. 스마트팜 조성
2. 데이터센터
3. 영상 스크린패널
4. 경량 칸막이 및 도어
5. CURTAIN WALL 필름지 부착

데이터 센터 소음차단(인접실)

구 분	금회공사
천 정	경량천정틀 T12흡음텍스 L형 천정몰딩
벽	경량벽체 T100 / WP2회 (소음차단) 기둥 벽면 WP2회 실리콘(바닥,벽,천정연결부) MDF 걸레받이
바 닥	바탕청소/T0.3 에폭시코팅 (표면 마감 협의)

유틸리티룸

구 분	금회공사
천 정	경량천정틀 T12흡음텍스 L형 천정몰딩
벽	준불연 판넬 벽체 T100 / OP2회 유리커튼월 연결시공 실리콘(바닥,벽,천정연결부) MDF 걸레받이
바 닥	바탕청소

스마트팜

구 분	금회공사
천 정	경량천정틀 T0.45금속천정재(지정색) L형 천정몰딩
벽	단열 유리커튼월 T150 (노출부) 준불연 판넬 T150 (천정속) 실리콘(바닥,벽,천정연결부)
바 닥	바탕청소/T0.3 에폭시코팅(지정색) (표면 마감 협의)

지정장소 - 범위 지정 장소(HATCH부분)

구 분	금회공사
천 정	기존 텍스위 /WP2회
벽	기존 벽체 면정리 /WP2회
기둥	기존 걸레받이 벽체 면정리 세라민2회 H 100
바 닥	바탕청소

변경후 1층 평면도

1/250

PROJECT TITLE



피지컬 시리빙센터 구축 공사

Date.

No. Revision

-	-
-	-
-	-
-	-
-	-
-	-
-	-
-	-
-	-
-	-

NOTE

WP(지정색)

벽체 (판넬 ,커튼월)
이질 자재 연결부
외측 마감면을 기준
경량칸막이 ,판넬
바닥 벽 천정 연결부
실리콘 처리

Structure


Mechanical

Electrical

Fire Protection

Civil

Landscape

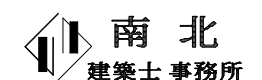

建築士 鄭 範 洙

전북 전주시 완산구 서신로57 7층

TEL : 063)247-7787

FAX : 063)247-7786

E-MAIL : nba2007@daum.net

SHEET TITLE

변경후 1층 평면도

DESIGN BY

SCALE

A3 1/250

CHECKED BY

DATE

APPROVED BY

SHEET NO.

SERIAL NO.

A- 200

PROJECT TITLE



피지컬 시리빙센터 구축 공사

Date.

No. Revision

-	-
-	-
-	-
-	-
-	-
-	-
-	-
-	-
-	-
-	-

NOTE

Structure


Mechanical

Electrical

Fire Protection

Civil

Landscape

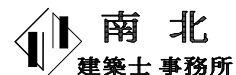

建築士 鄭 範 洙

전북 전주시 완산구 서신로57 7층

TEL : 063)247-7787

FAX : 063)247-7786

E-MAIL : nba2007@daum.net

SHEET TITLE

변경후 1층 확대 평면도

DESIGN BY

SCALE

A3 1/150

CHECKED BY


DATE

APPROVED BY

SHEET NO.

SERIAL NO.

A- 201

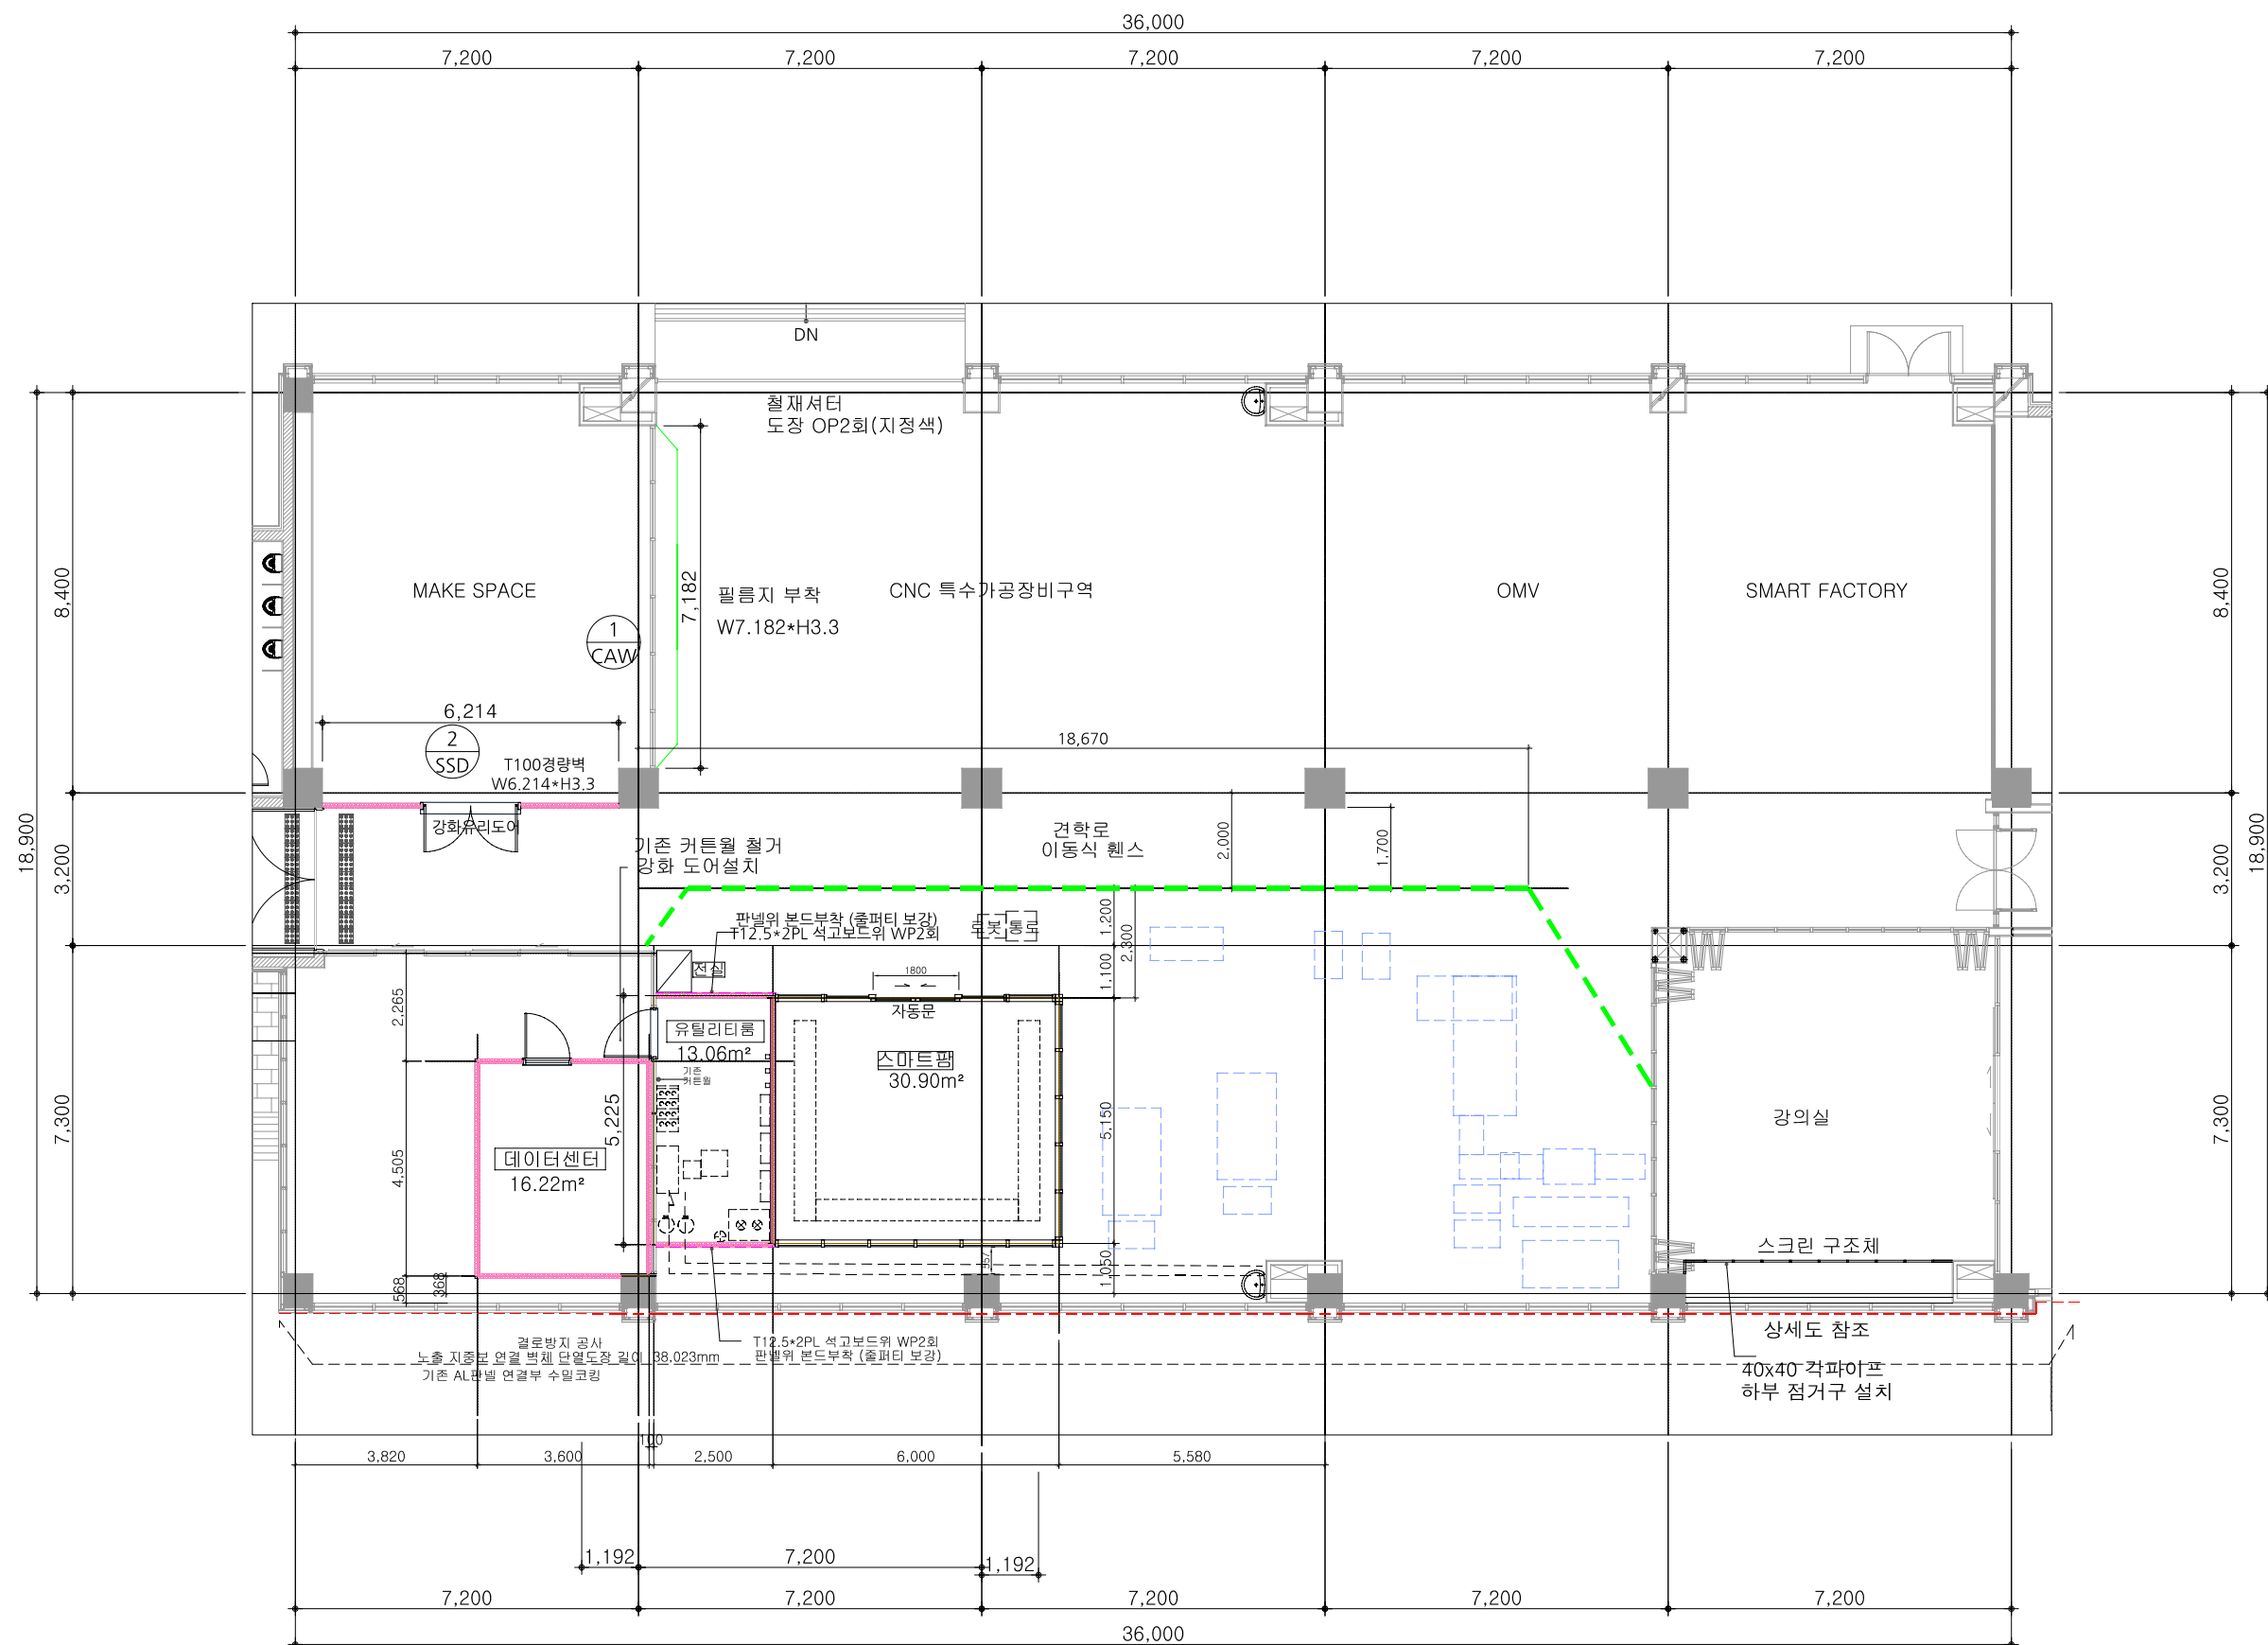

데이터 센터 소음차단(인접실)

구 분	금회공사
천 정	경량천정틀 T12흡음텍스 L형 천정물딩
벽	경량벽체 T100 / WP2회 (소음차단) 가동 벽면 WP2회 실리콘(바닥,벽,천정연결부) MDF 걸레받이
바 닥	바탕청소/T0.3 에폭시코팅 (표면 마감 협의)

유틸리티룸


구 분	금회공사
천 정	경량천정틀 T12흡음텍스 L형 천정물딩
벽	준불연 판넬 벽체 T100 / OP2회 유리커튼월 연결시공 실리콘(바닥,벽,천정연결부) MDF 걸레받이
바 닥	바탕청소

스마트팜

구 분	금회공사
천 정	경량천정틀 T0.45금속천정재(지정색) L형 천정물딩
벽	단열 유리커튼월 T150 (노출부) 준불연 판넬 T150 (천정속) 실리콘(바닥,벽,천정연결부)
바 닥	바탕청소/T0.3 에폭시코팅(지정색) (표면 마감 협의)


지정장소 - 범위 지정 장소(HATCH부분)

구 분	금회공사
천 정	기존 텍스워 /WP2회
벽	기존 벽체 면정리 /WP2회
기둥	기존 걸레받이 벽체 면정리 세라민2회 H 100
바 닥	바탕청소

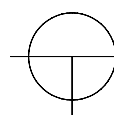

변경후 1층 확대 평면도

1/150

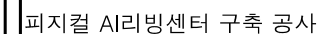




NOTE

기존 창호 실측후
금회공사 창호 제작설치

 **南北**
建築士事務所
建築士 鄭 範 洙

SHEET TITLE
데이터센터 스마트팜
확대 평면도

DESIGN BY	SCALE A3 1/60
CHECKED BY	DATE
APPROVED BY	SHEET NO. A-202
SERIAL NO.	

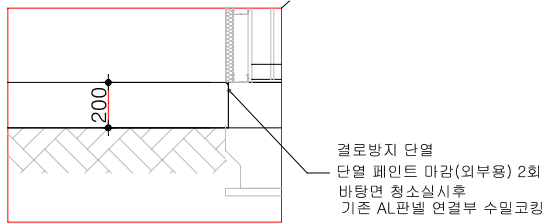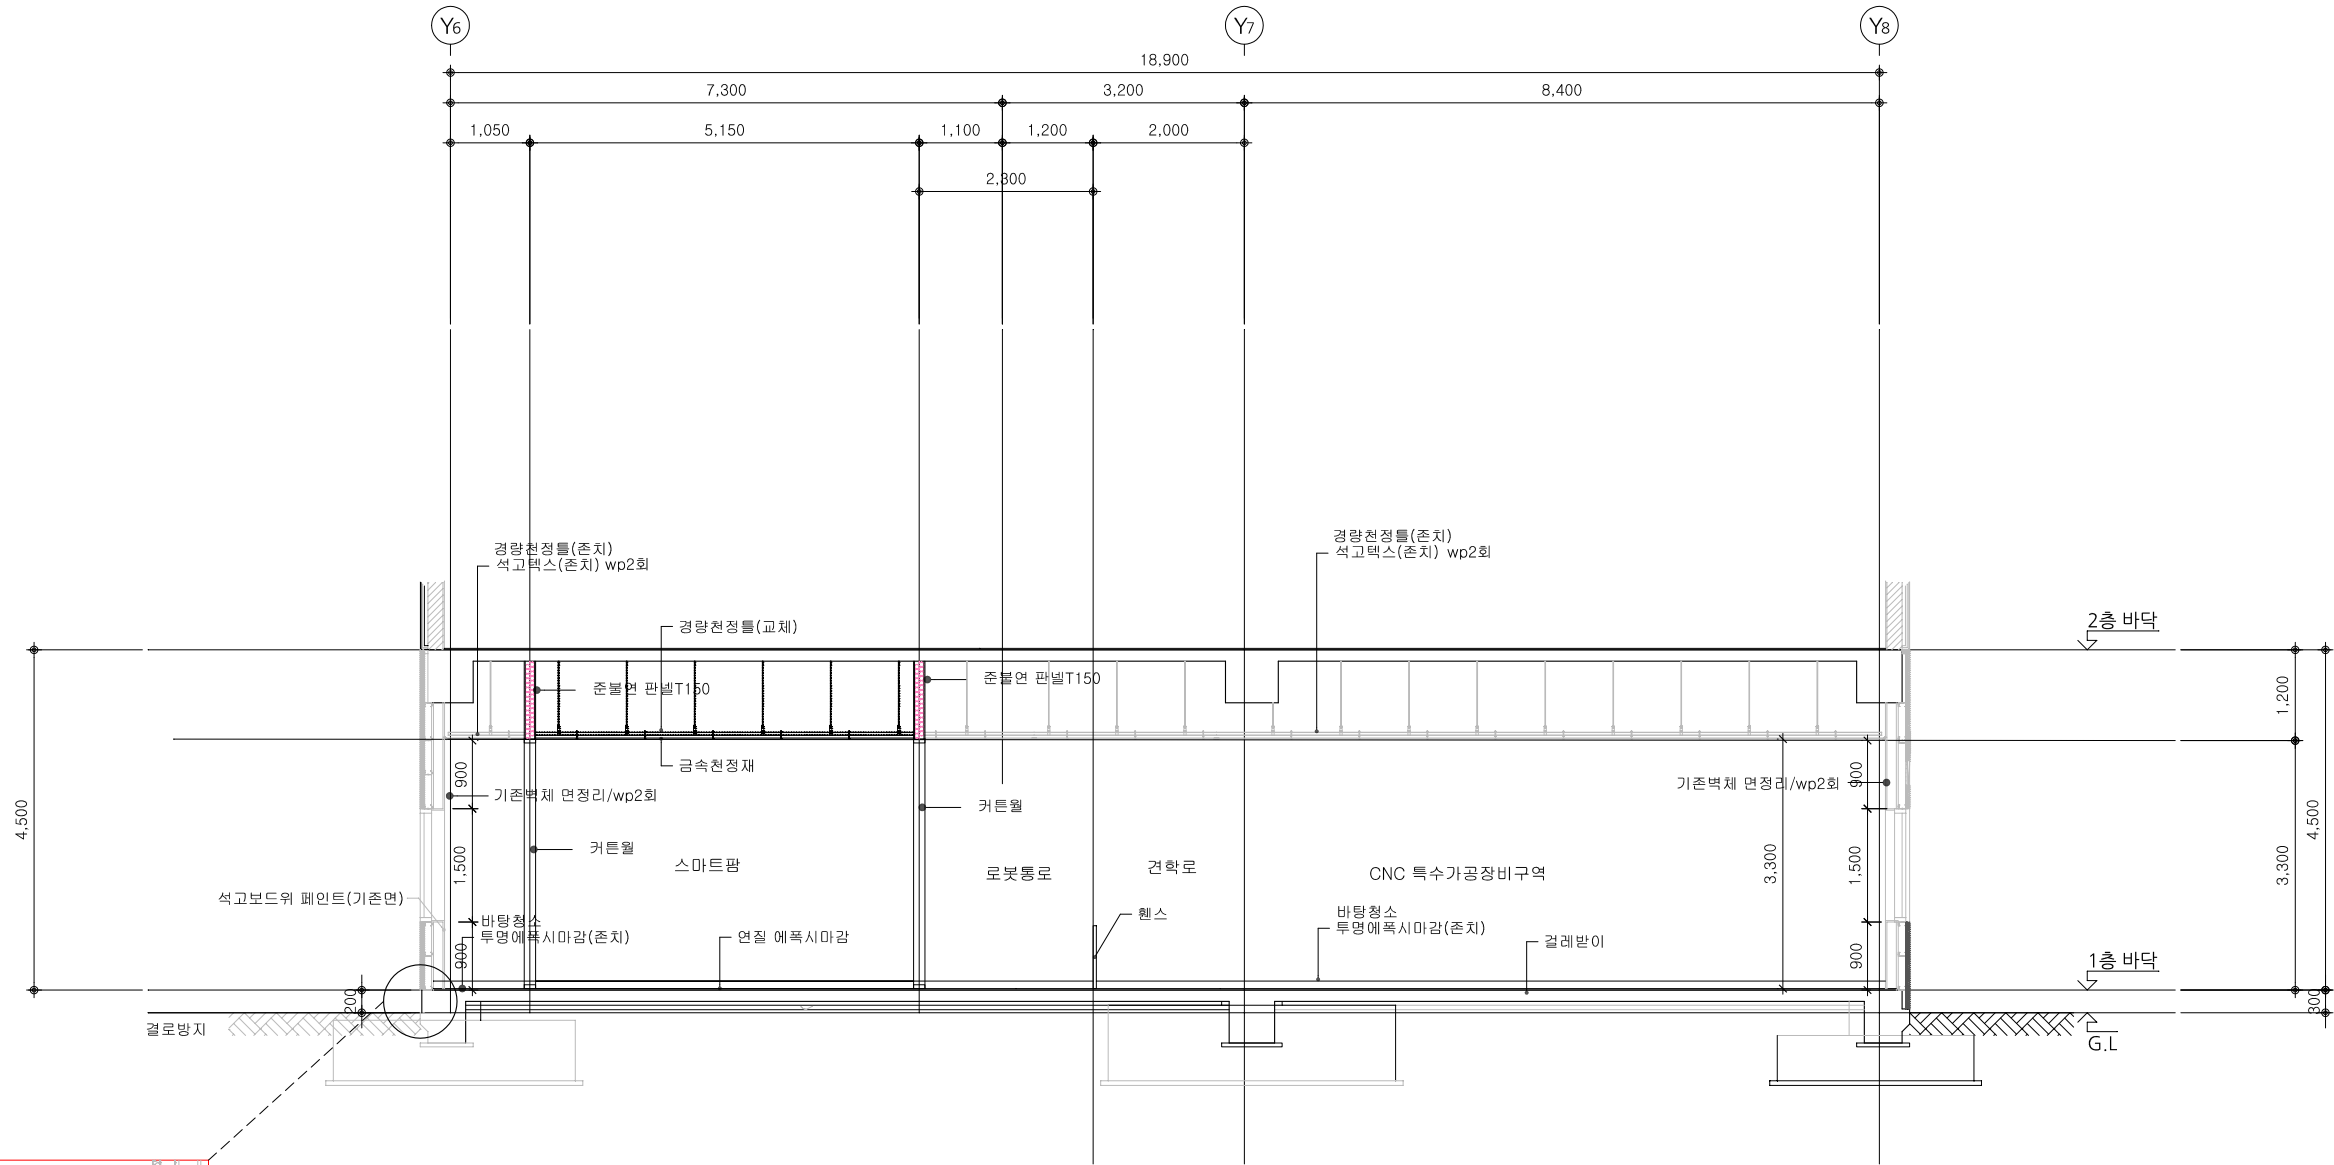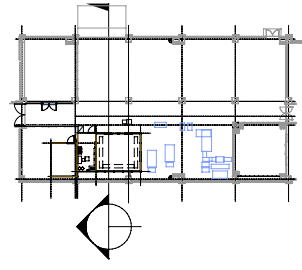

변경후 종단면도1
1/100

PROJECT TITLE



피지컬 시리빙센터 구축 공사

Date.

No. Revision

-
-
-
-
-
-
-
-
-
-
-

NOTE

Structure


Mechanical

Electrical

Fire Protection

Civil

Landscape

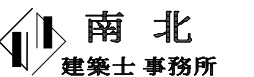

建築士 鄭 範 洙

전북 전주시 완산구 서신로57 7층

TEL : 063)247-7787

FAX : 063)247-7786

E-MAIL : nba2007@daum.net

SHEET TITLE

변경후 종단면도1

DESIGN BY

SCALE

A3 1/100

CHECKED BY



DATE

APPROVED BY

SHEET NO.

SERIAL NO.

A- 203

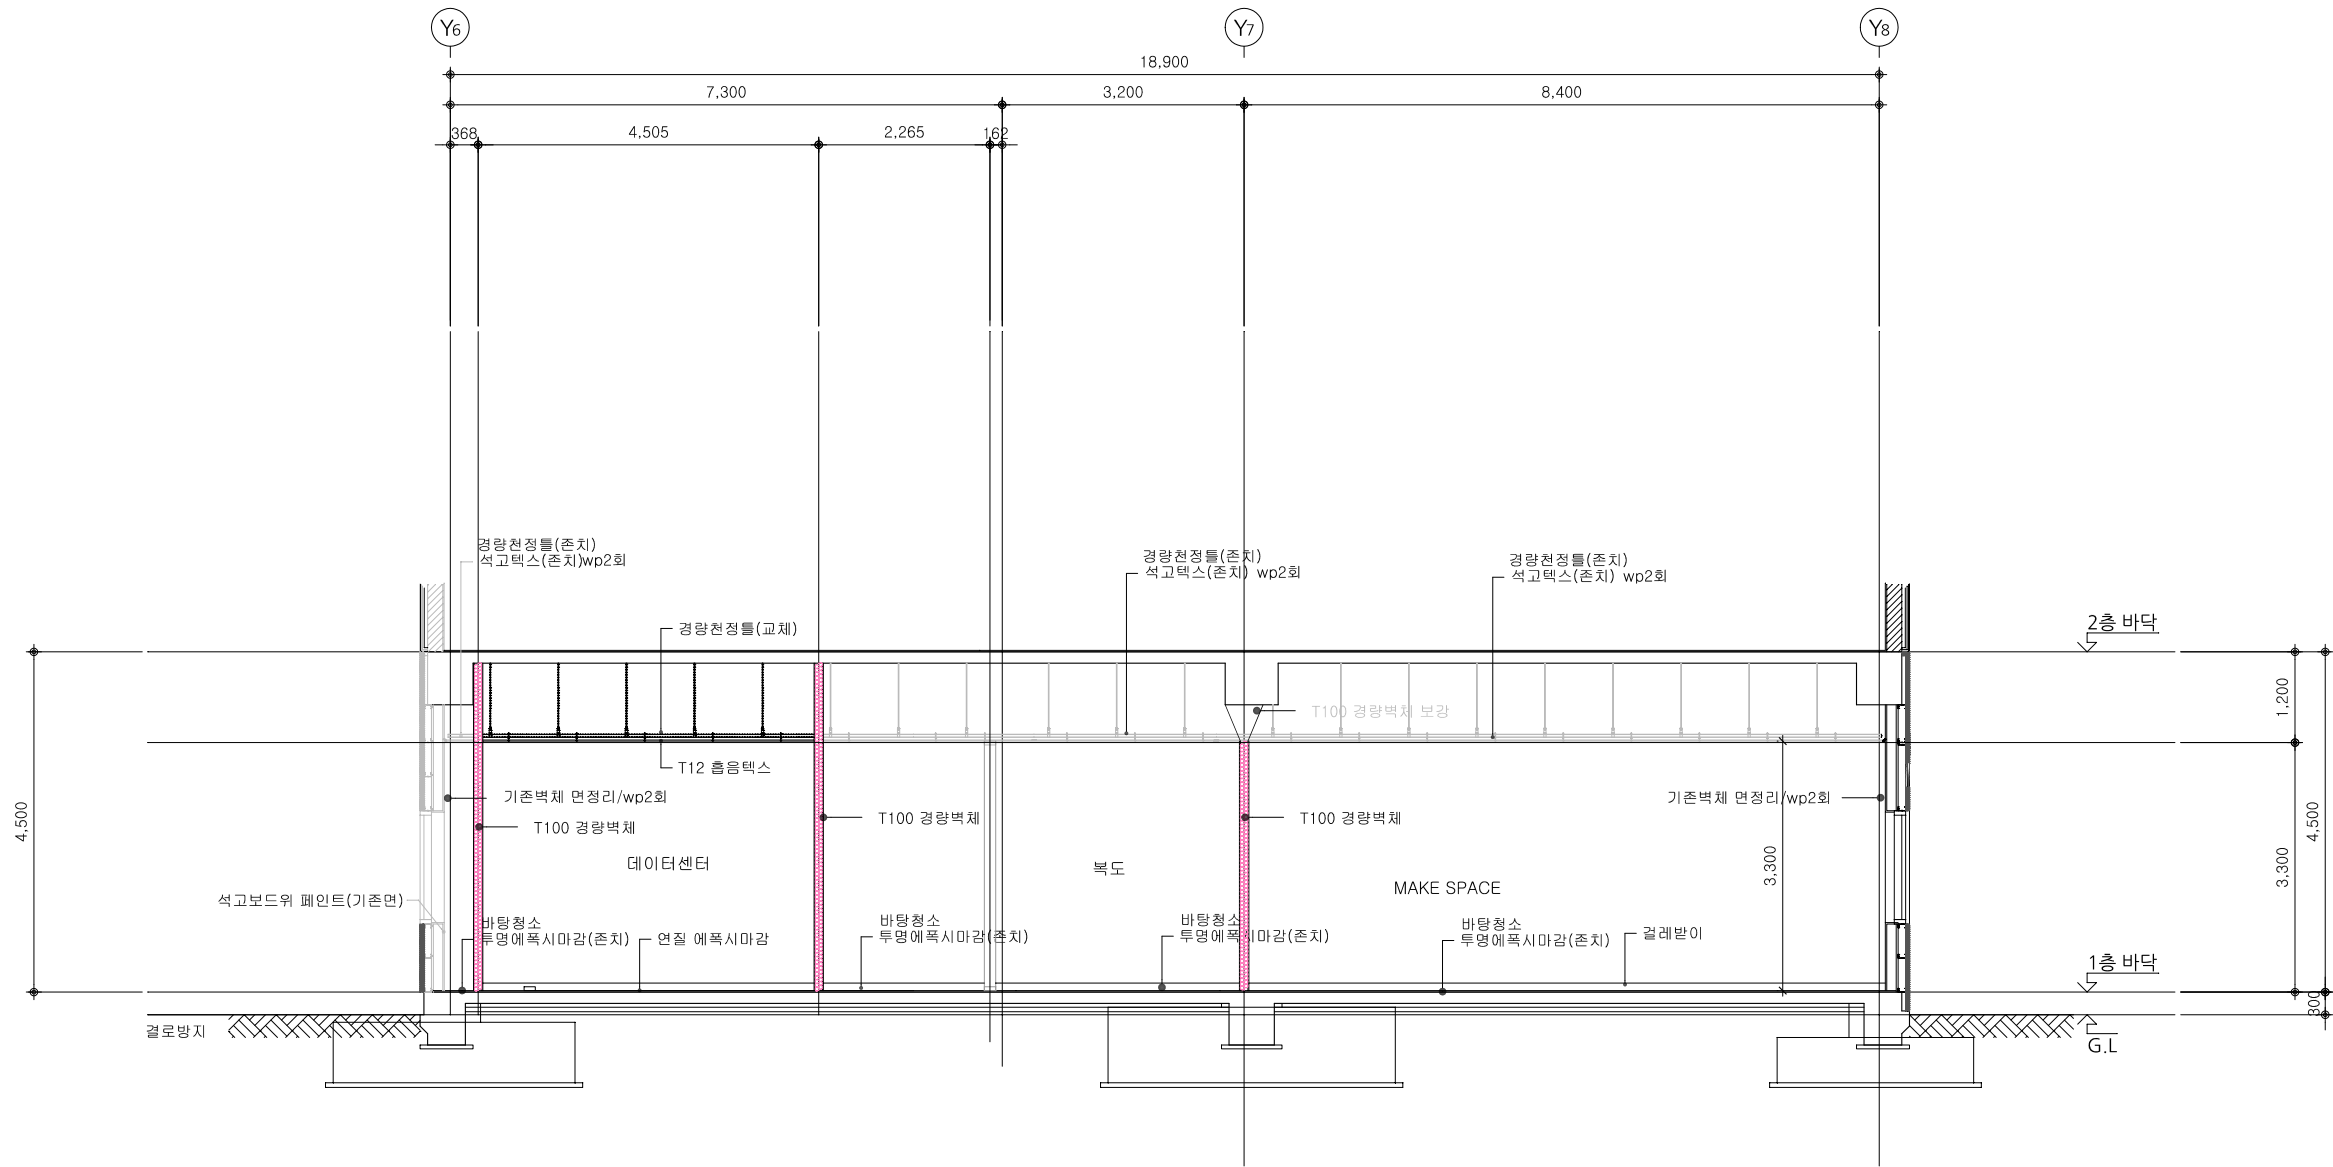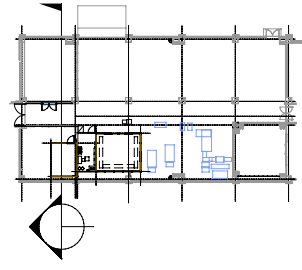

변경후 종단면도2
1/100

PROJECT TITLE


피지컬 시리빙센터 구축 공사

Date.

No.	Revision
-	-
-	-
-	-
-	-
-	-
-	-
-	-
-	-
-	-

NOTE

Structure

Mechanical

Electrical

Fire Protection

Civil

Landscape

 南北
建築士事務所


建築士 鄭 範 洙

전북 전주시 완산구 서신로57 7층
TEL : 063)247-7787
FAX : 063)247-7786
E-MAIL : nba2007@daum.net

SHEET TITLE

변경후 종단면도2

DESIGN BY	SCALE A3 1/100
CHECKED BY	DATE
APPROVED BY	SHEET NO. A- 204
SERIAL NO.	

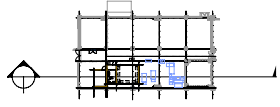

PROJECT TITLE



피지컬 시리빙센터 구축 공사

Date.

No. Revision

-	
-	
-	
-	
-	
-	
-	
-	
-	
-	
-	

NOTE

Structure


Mechanical

Electrical

Fire Protection

Civil

Landscape

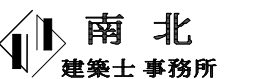

建築士 鄭 範 洙

전북 전주시 완산구 서신로57 7층

TEL : 063)247-7787

FAX : 063)247-7786

E-MAIL : nba2007@daum.net

SHEET TITLE

변경후 횡단면도

DESIGN BY

SCALE

A3 1/200

CHECKED BY



DATE

APPROVED BY

SHEET NO.


SERIAL NO.

A- 205

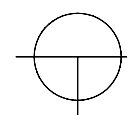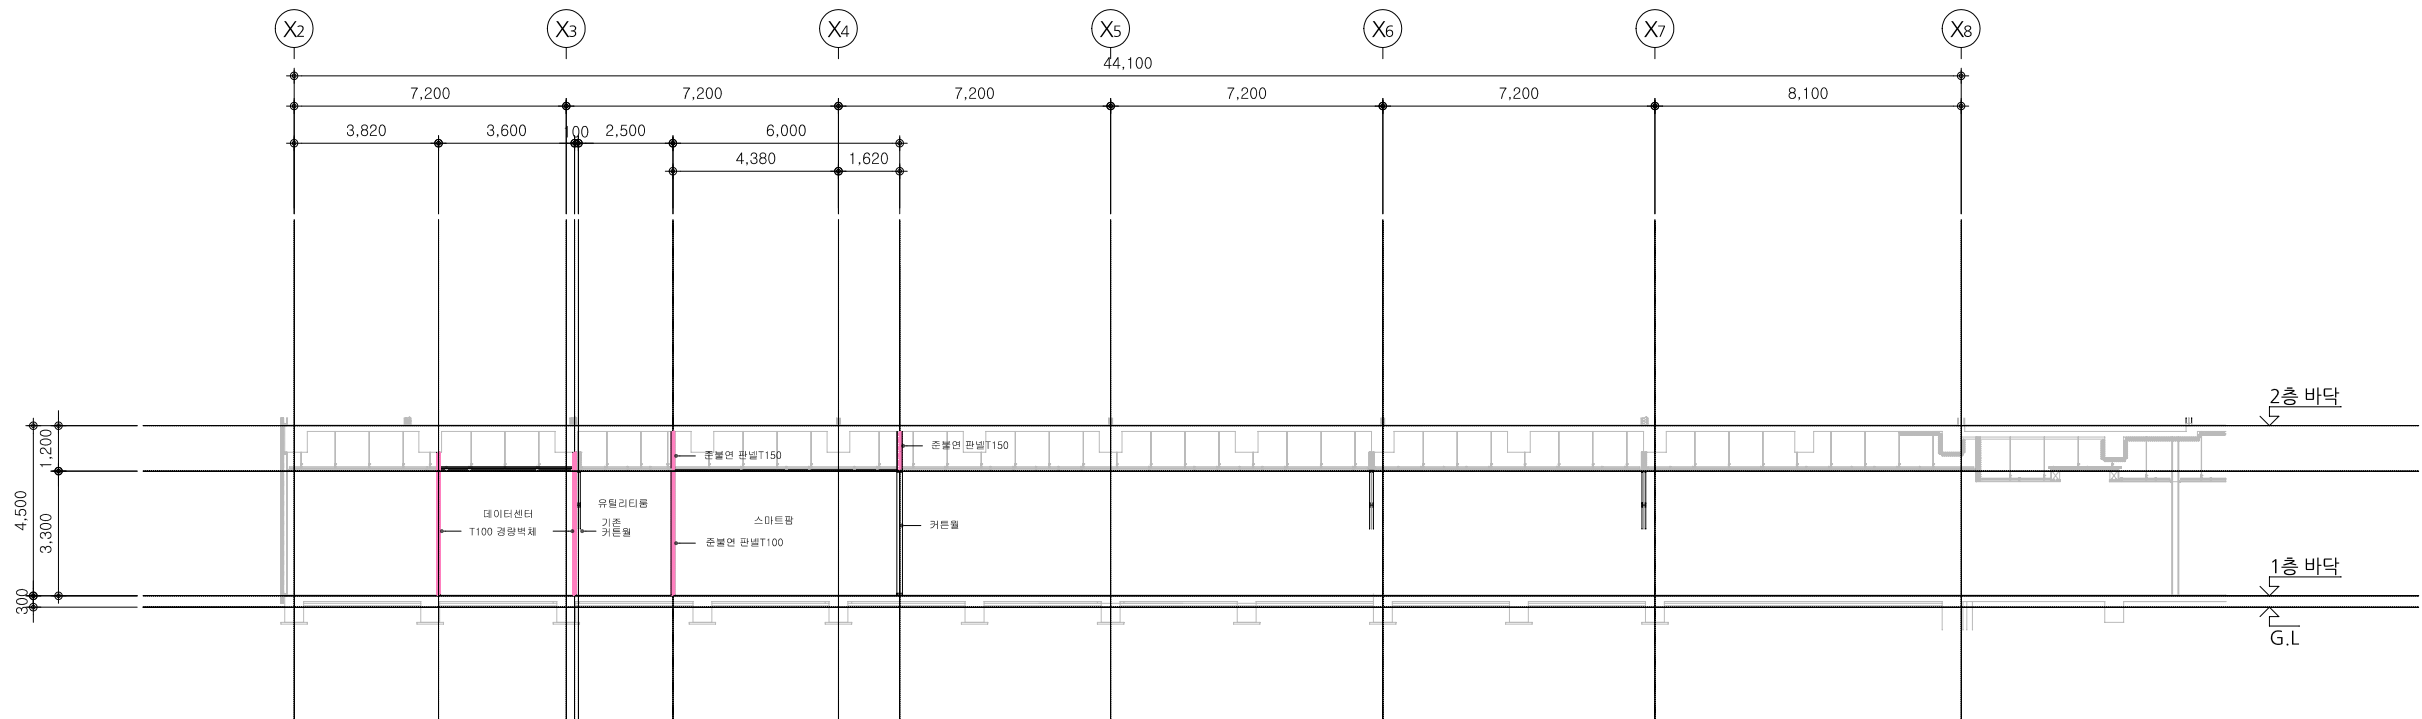

변경후 횡단면도

1/200

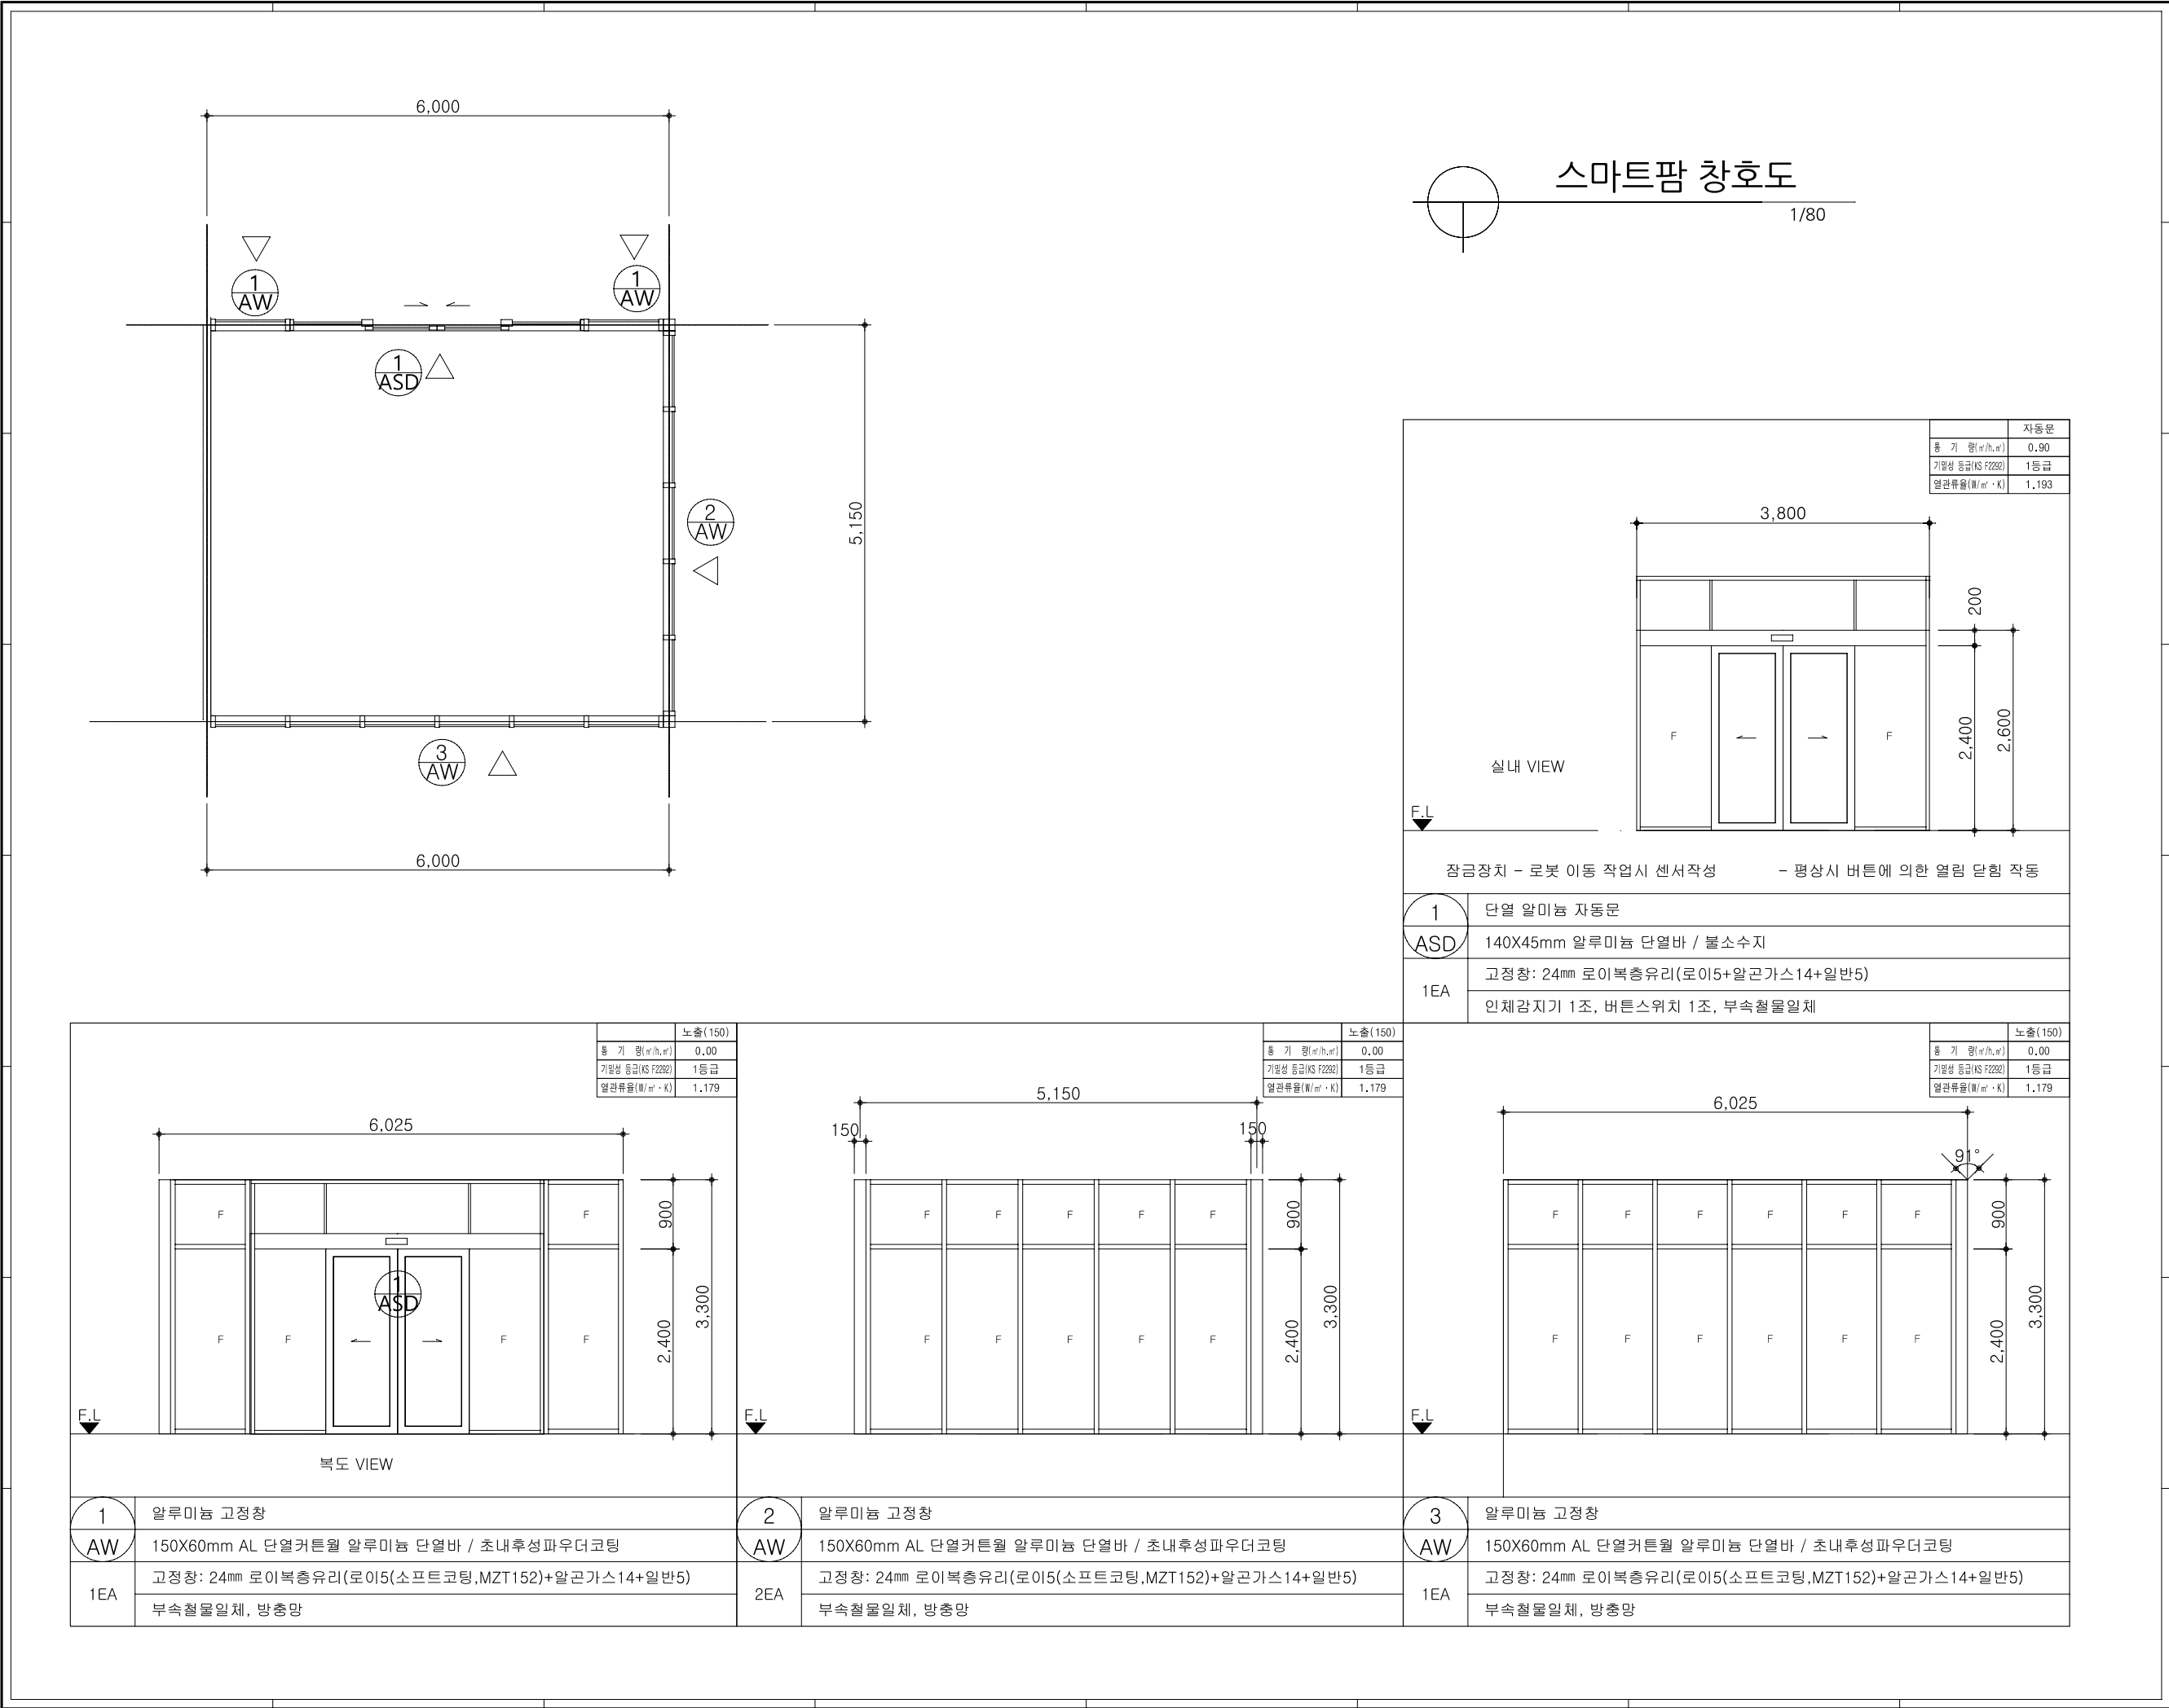

PROJECT TITLE



피지컬 시리빙센터 구축 공사

Date.

No.	Revision
-	-
-	-
-	-
-	-
-	-
-	-
-	-
-	-
-	-

NOTE

커튼월 수직바 등간격 설치

Structure

Mechanical

Electrical

Fire Protection

Civil

Landscape



南北
建築士事務所

建築士 鄭 範 洙


전북 전주시 완산구 서신로57 7층
TEL : 063)247-7787
FAX : 063)247-7786
E-MAIL : nba2007@daum.net

SHEET TITLE

스마트팜 창호도


DESIGN BY	SCALE
CHECKED BY	A3 1/80
APPROVED BY	DATE
SERIAL NO.	SHEET NO.
	A- 206

A

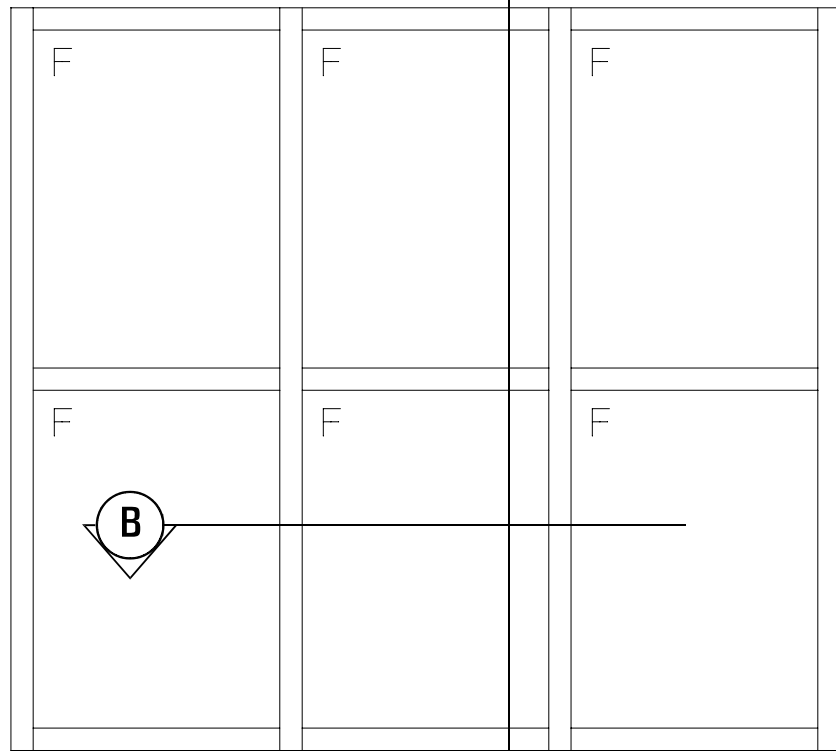

B

1 ELEVATION

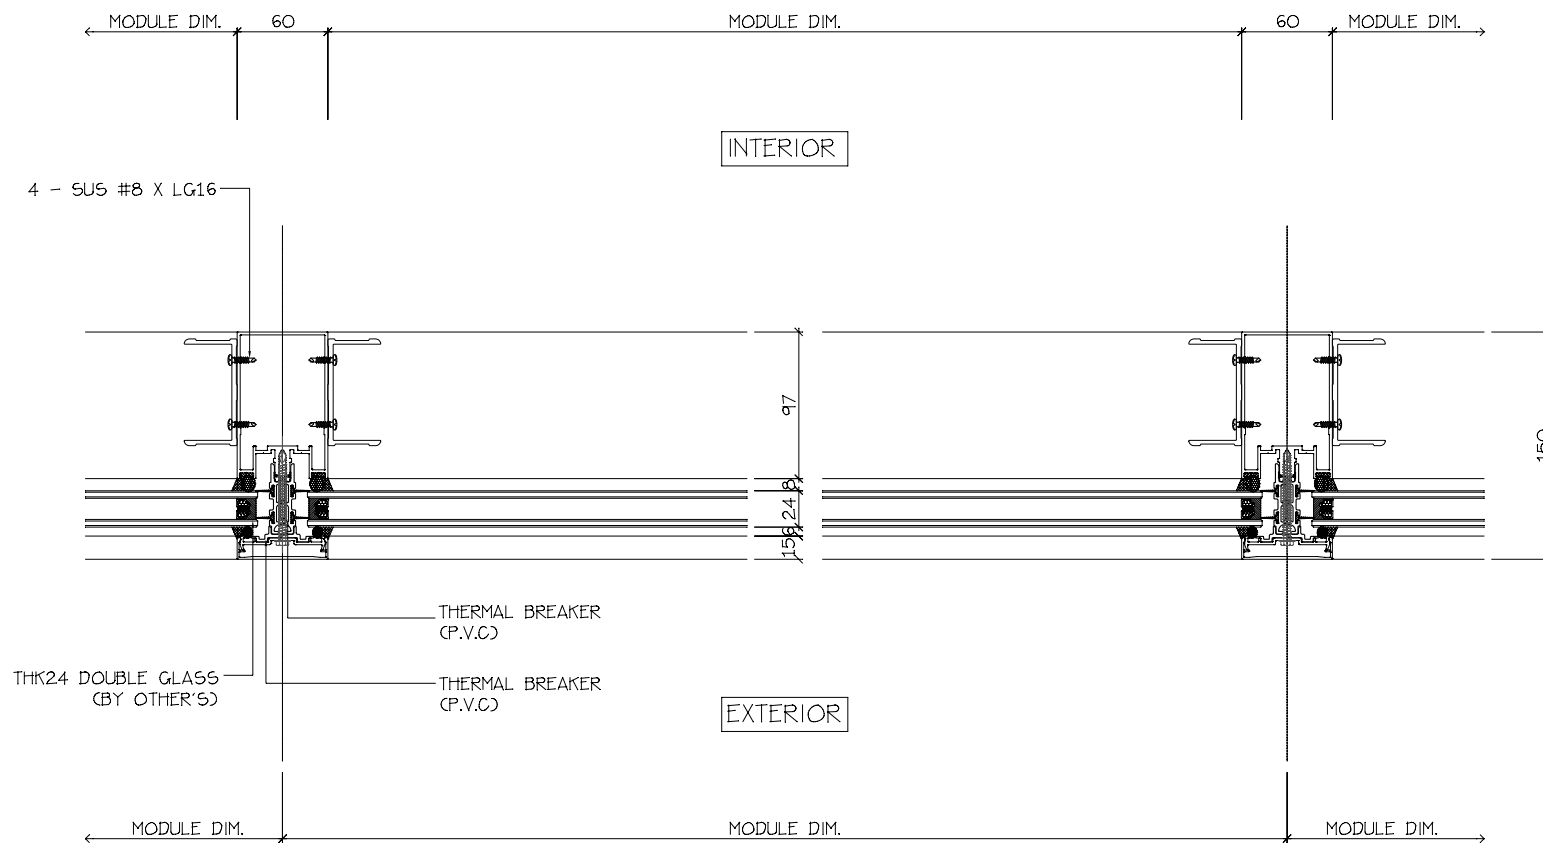

2 150MM 단열 커튼월(HORIZONTAL SECTION - B)

MODULE DIM.

MODULE DIM.

3 150MM 단열 커튼월(VERTICAL SECTION - A)

THK24 DOUBLE GLASS
(BY OTHER'S)

EXTERIOR

STRUCTUAL SILICON SEALANT
/W NORTON TAPE
(BY OTHER'S)

SHEAR BLOCK
(CHROMATE FIN.)

INTERIOR

THERMAL BREAKER
(P.V.C)

158 24 8 97 150

PROJECT TITLE



피지컬 시리빙센터 구축 공사

Date.

No. Revision

NOTE

Structure

Mechanical

Electrical

Fire Protection

Civil

Landscape

南北
建築士事務所

建築士 鄭 範 洙

전북 전주시 완산구 서신로57 7층

TEL : 063)247-7787

FAX : 063)247-7786

E-MAIL : nba2007@daum.net

SHEET TITLE

창호상세도1

DESIGN BY

SCALE
A3 1/5

CHECKED BY



DATE


APPROVED BY

SHEET NO.

SERIAL NO.

A- 207

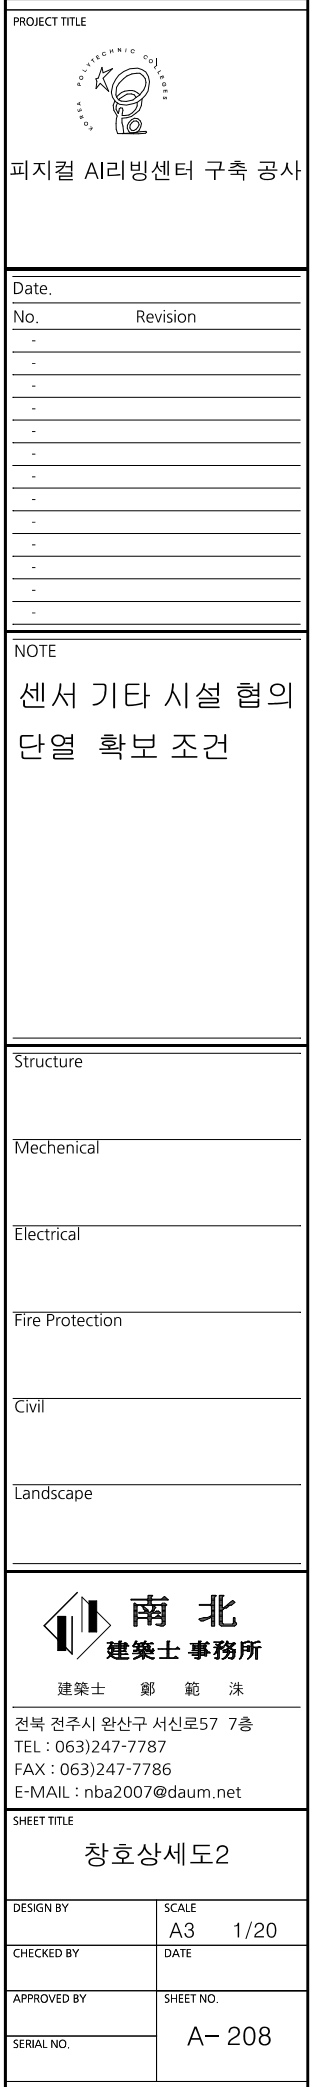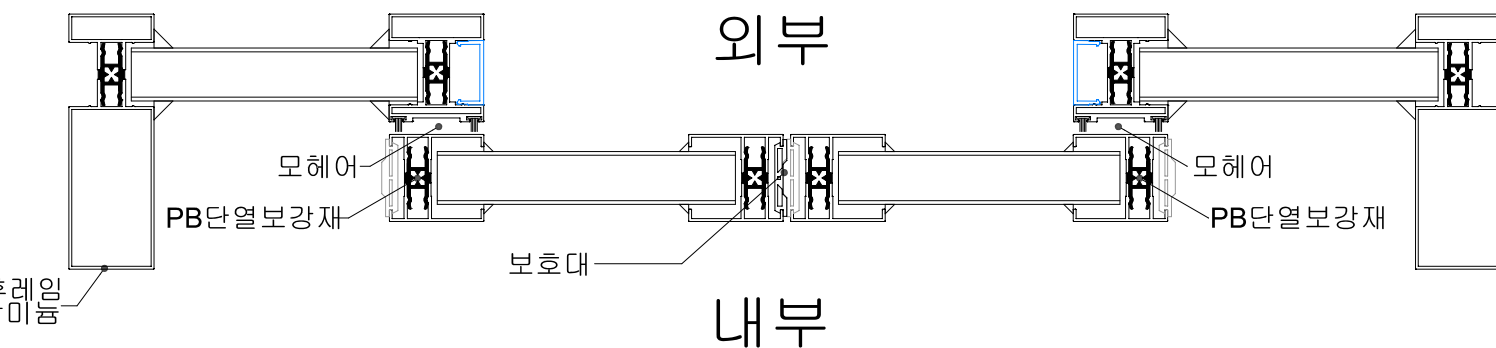

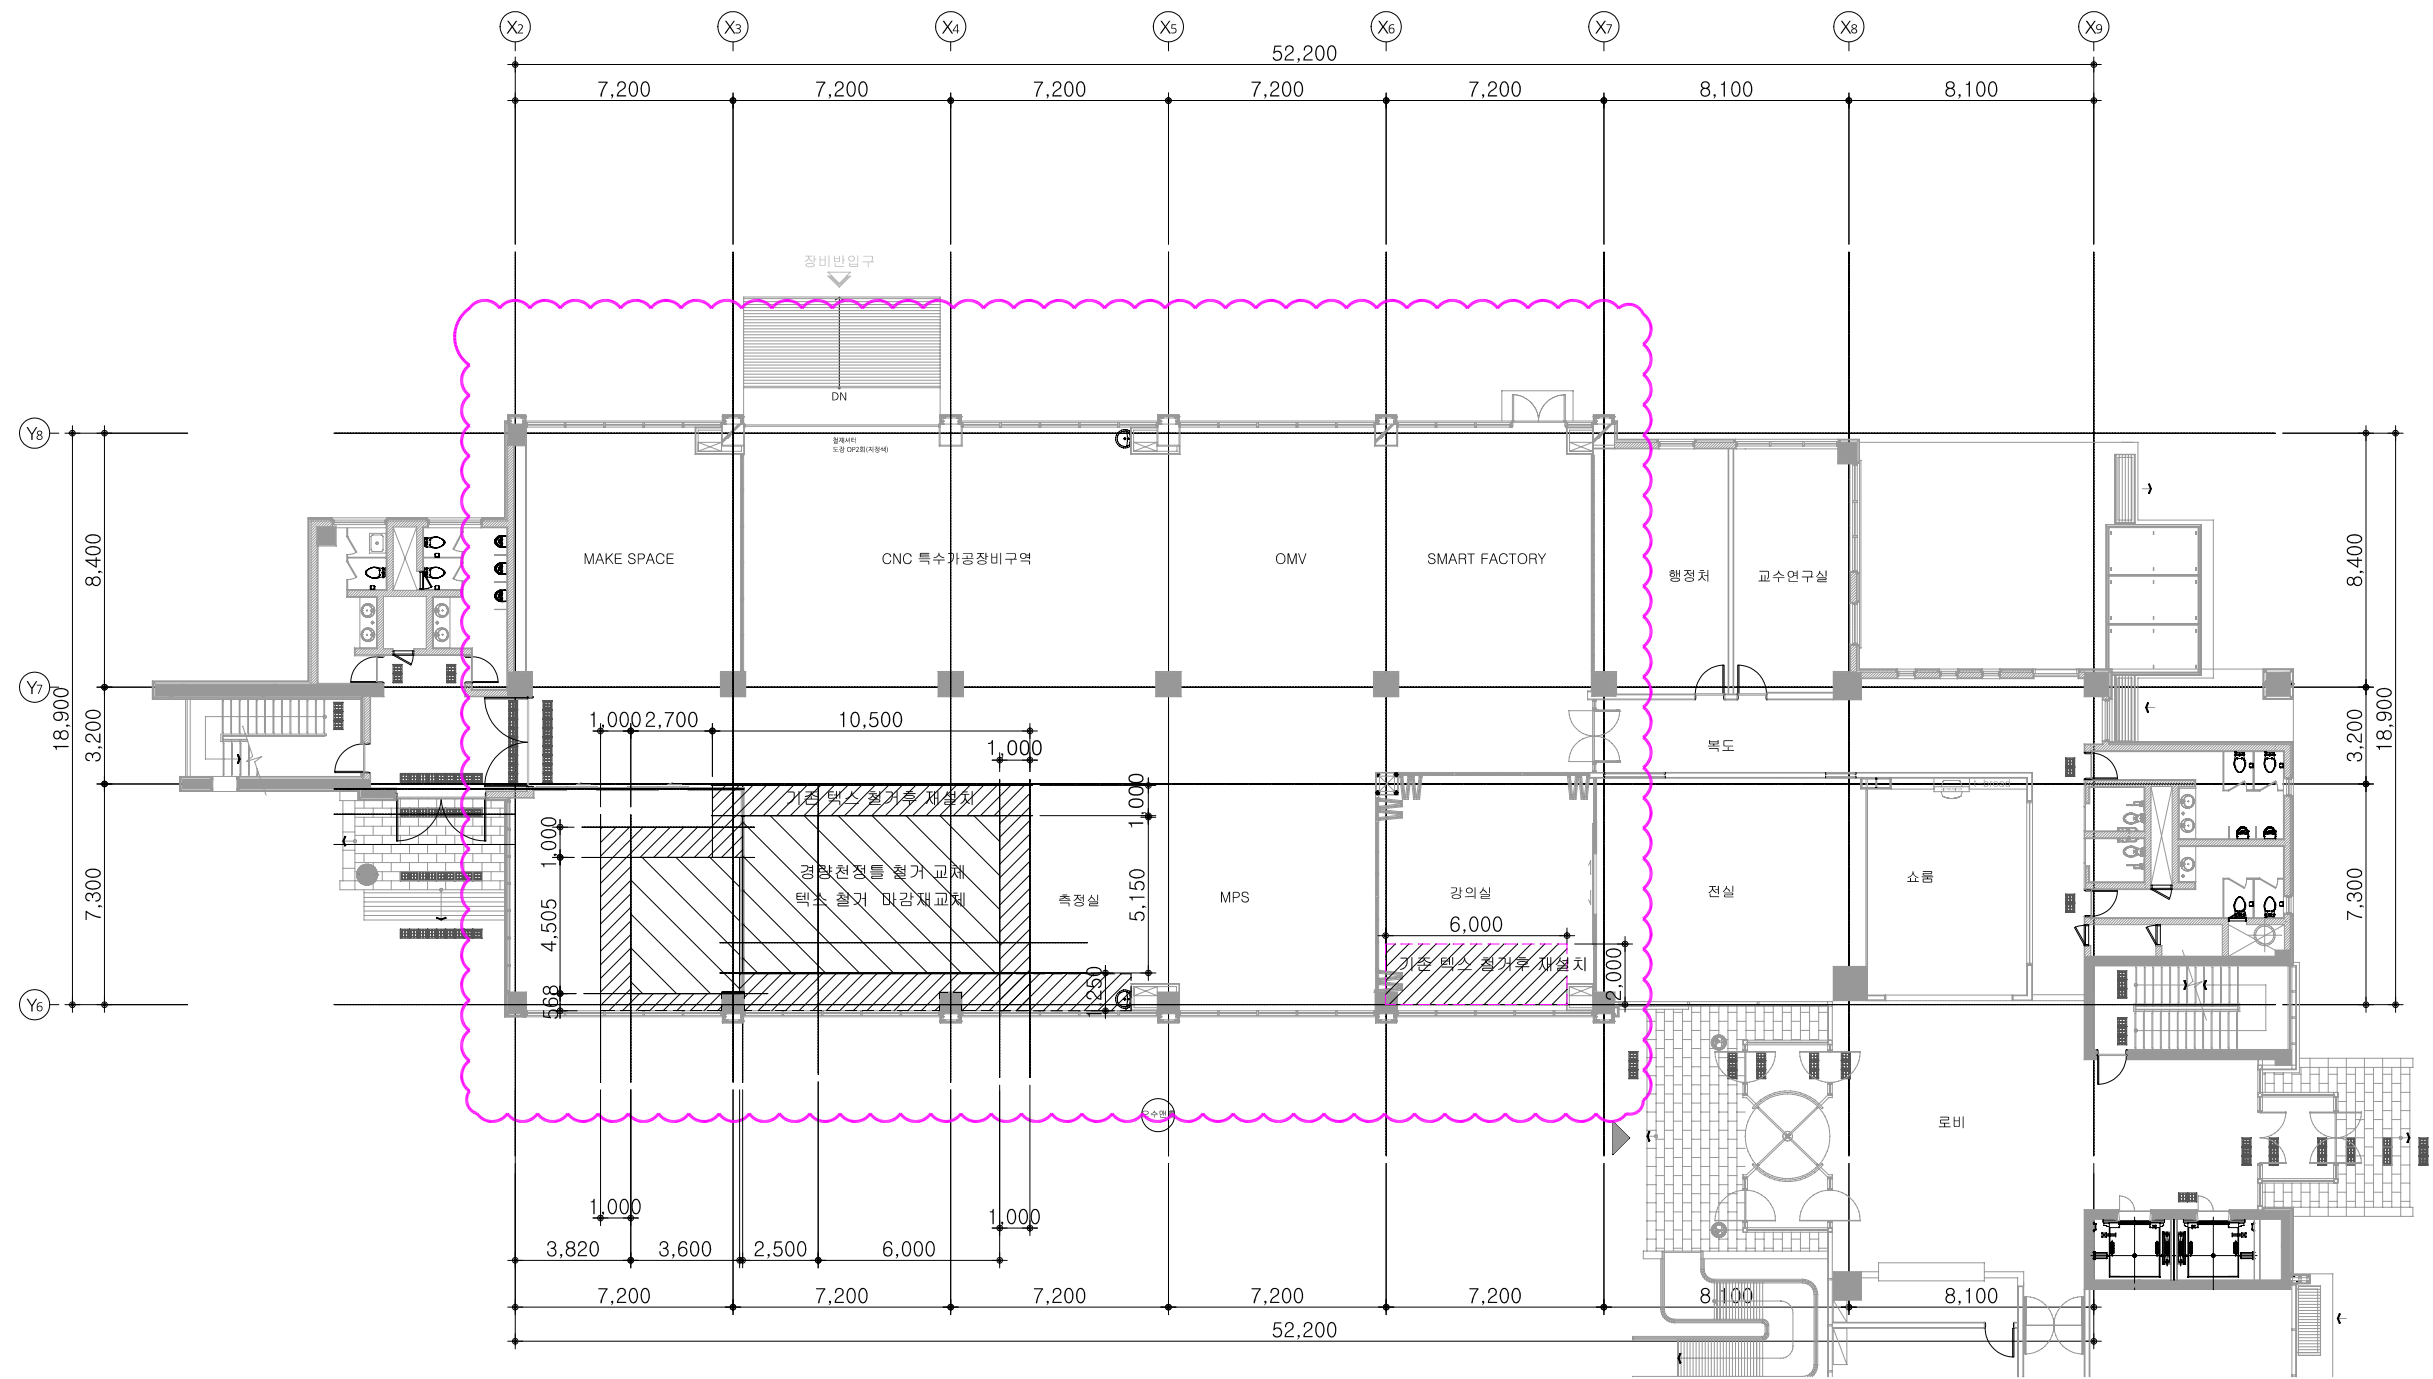


기타 시설

구 분	철거 및 시공
천 정	기존 텍스워 T9.5*1PL /WP3회
벽	기타벽면 WP2회 실리콘(바닥 벽 천정연결부)
바 닥	기존 에폭시 마감 청소

데이터 센터 유틸리티실 스마트팜

구 분	철거 및 시공
천 정	기존 텍스 및 천정을 철거
벽	기존 커튼월 벽체 존치
바 닥	기존 에폭시 마감 청소

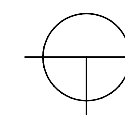

기존 1층 평면도

1/250

PROJECT TITLE



피지컬 시리빙센터 구축 공사

Date.

No. Revision

-	-
-	-
-	-
-	-
-	-
-	-
-	-
-	-
-	-
-	-

NOTE

Structure


Mechanical

Electrical

Fire Protection

Civil

Landscape

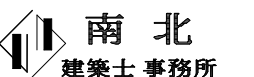

建築士 鄭 範 洙

전북 전주시 완산구 서신로57 7층

TEL : 063)247-7787

FAX : 063)247-7786

E-MAIL : nba2007@daum.net

SHEET TITLE

기존 1층 평면도

DESIGN BY

SCALE

A3 1/250

CHECKED BY


DATE

APPROVED BY

SHEET NO.

SERIAL NO.

A- 210

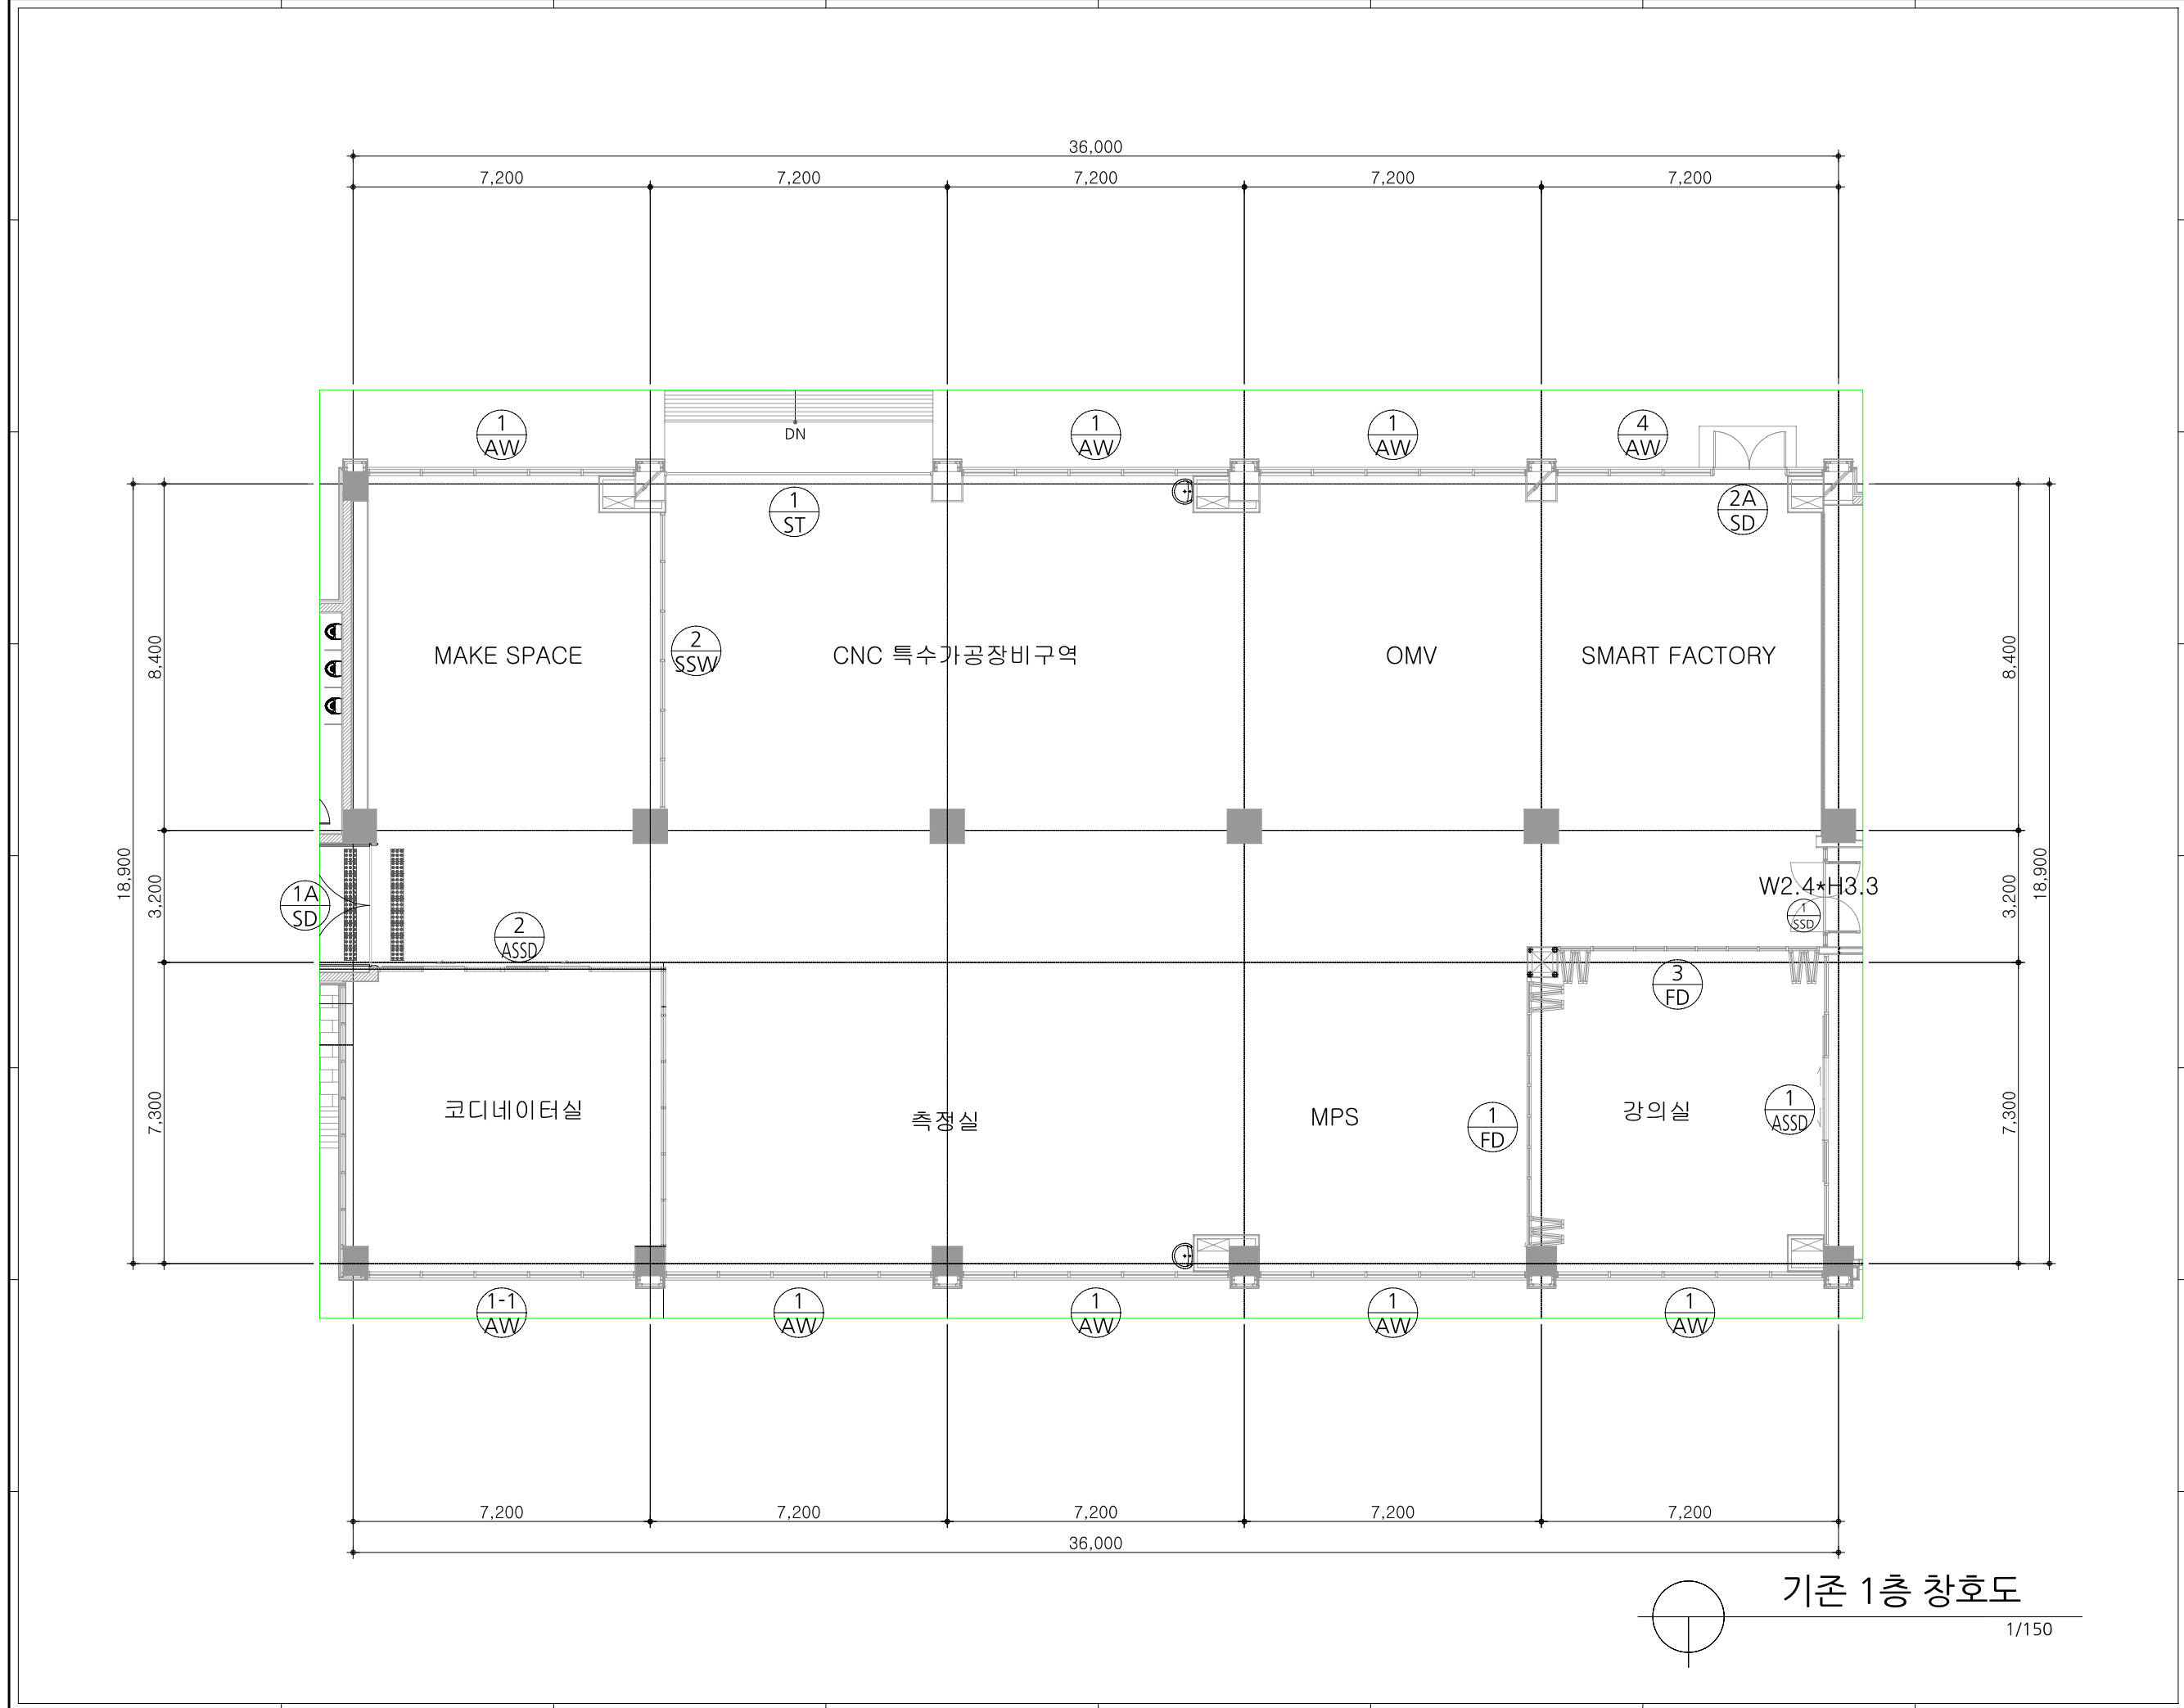

PROJECT TITLE


피지컬 시리빙센터 구축 공사

Date.

No.	Revision
-	-
-	-
-	-
-	-
-	-
-	-
-	-
-	-
-	-

NOTE

Structure

Mechanical

Electrical

Fire Protection

Civil

Landscape

 南北
建築士事務所
建築士 鄭 範 洙

전북 전주시 완산구 서신로57 7층
TEL : 063)247-7787
FAX : 063)247-7786
E-MAIL : nba2007@daum.net

SHEET TITLE

기존 1층 창호도

DESIGN BY	SCALE A3 1/150
CHECKED BY	DATE
APPROVED BY	SHEET NO.
SERIAL NO.	A- 211

PROJECT TITLE



피지컬 시리빙센터 구축 공사

Date.

No. Revision

-	-
-	-
-	-
-	-
-	-
-	-
-	-
-	-
-	-
-	-
-	-

NOTE

Structure


Mechanical

Electrical

Fire Protection

Civil

Landscape

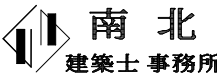

建築士 鄭 範 洙

전북 전주시 완산구 서신로57 7층

TEL : 063)247-7787

FAX : 063)247-7786


E-MAIL : nba2007@daum.net

SHEET TITLE

기존 창호도1

DESIGN BY	SCALE A3 1/120
CHECKED BY	DATE
APPROVED BY	SHEET NO. A- 212
SERIAL NO.	

명칭	위치	재	유리 / 마감	철	물	태	태	태	태
명칭	위치	재	유리 / 마감	철	물	태	태	태	태
명칭	위치	재	유리 / 마감	철	물	태	태	태	태
명칭	위치	재	유리 / 마감	철	물	태	태	태	태

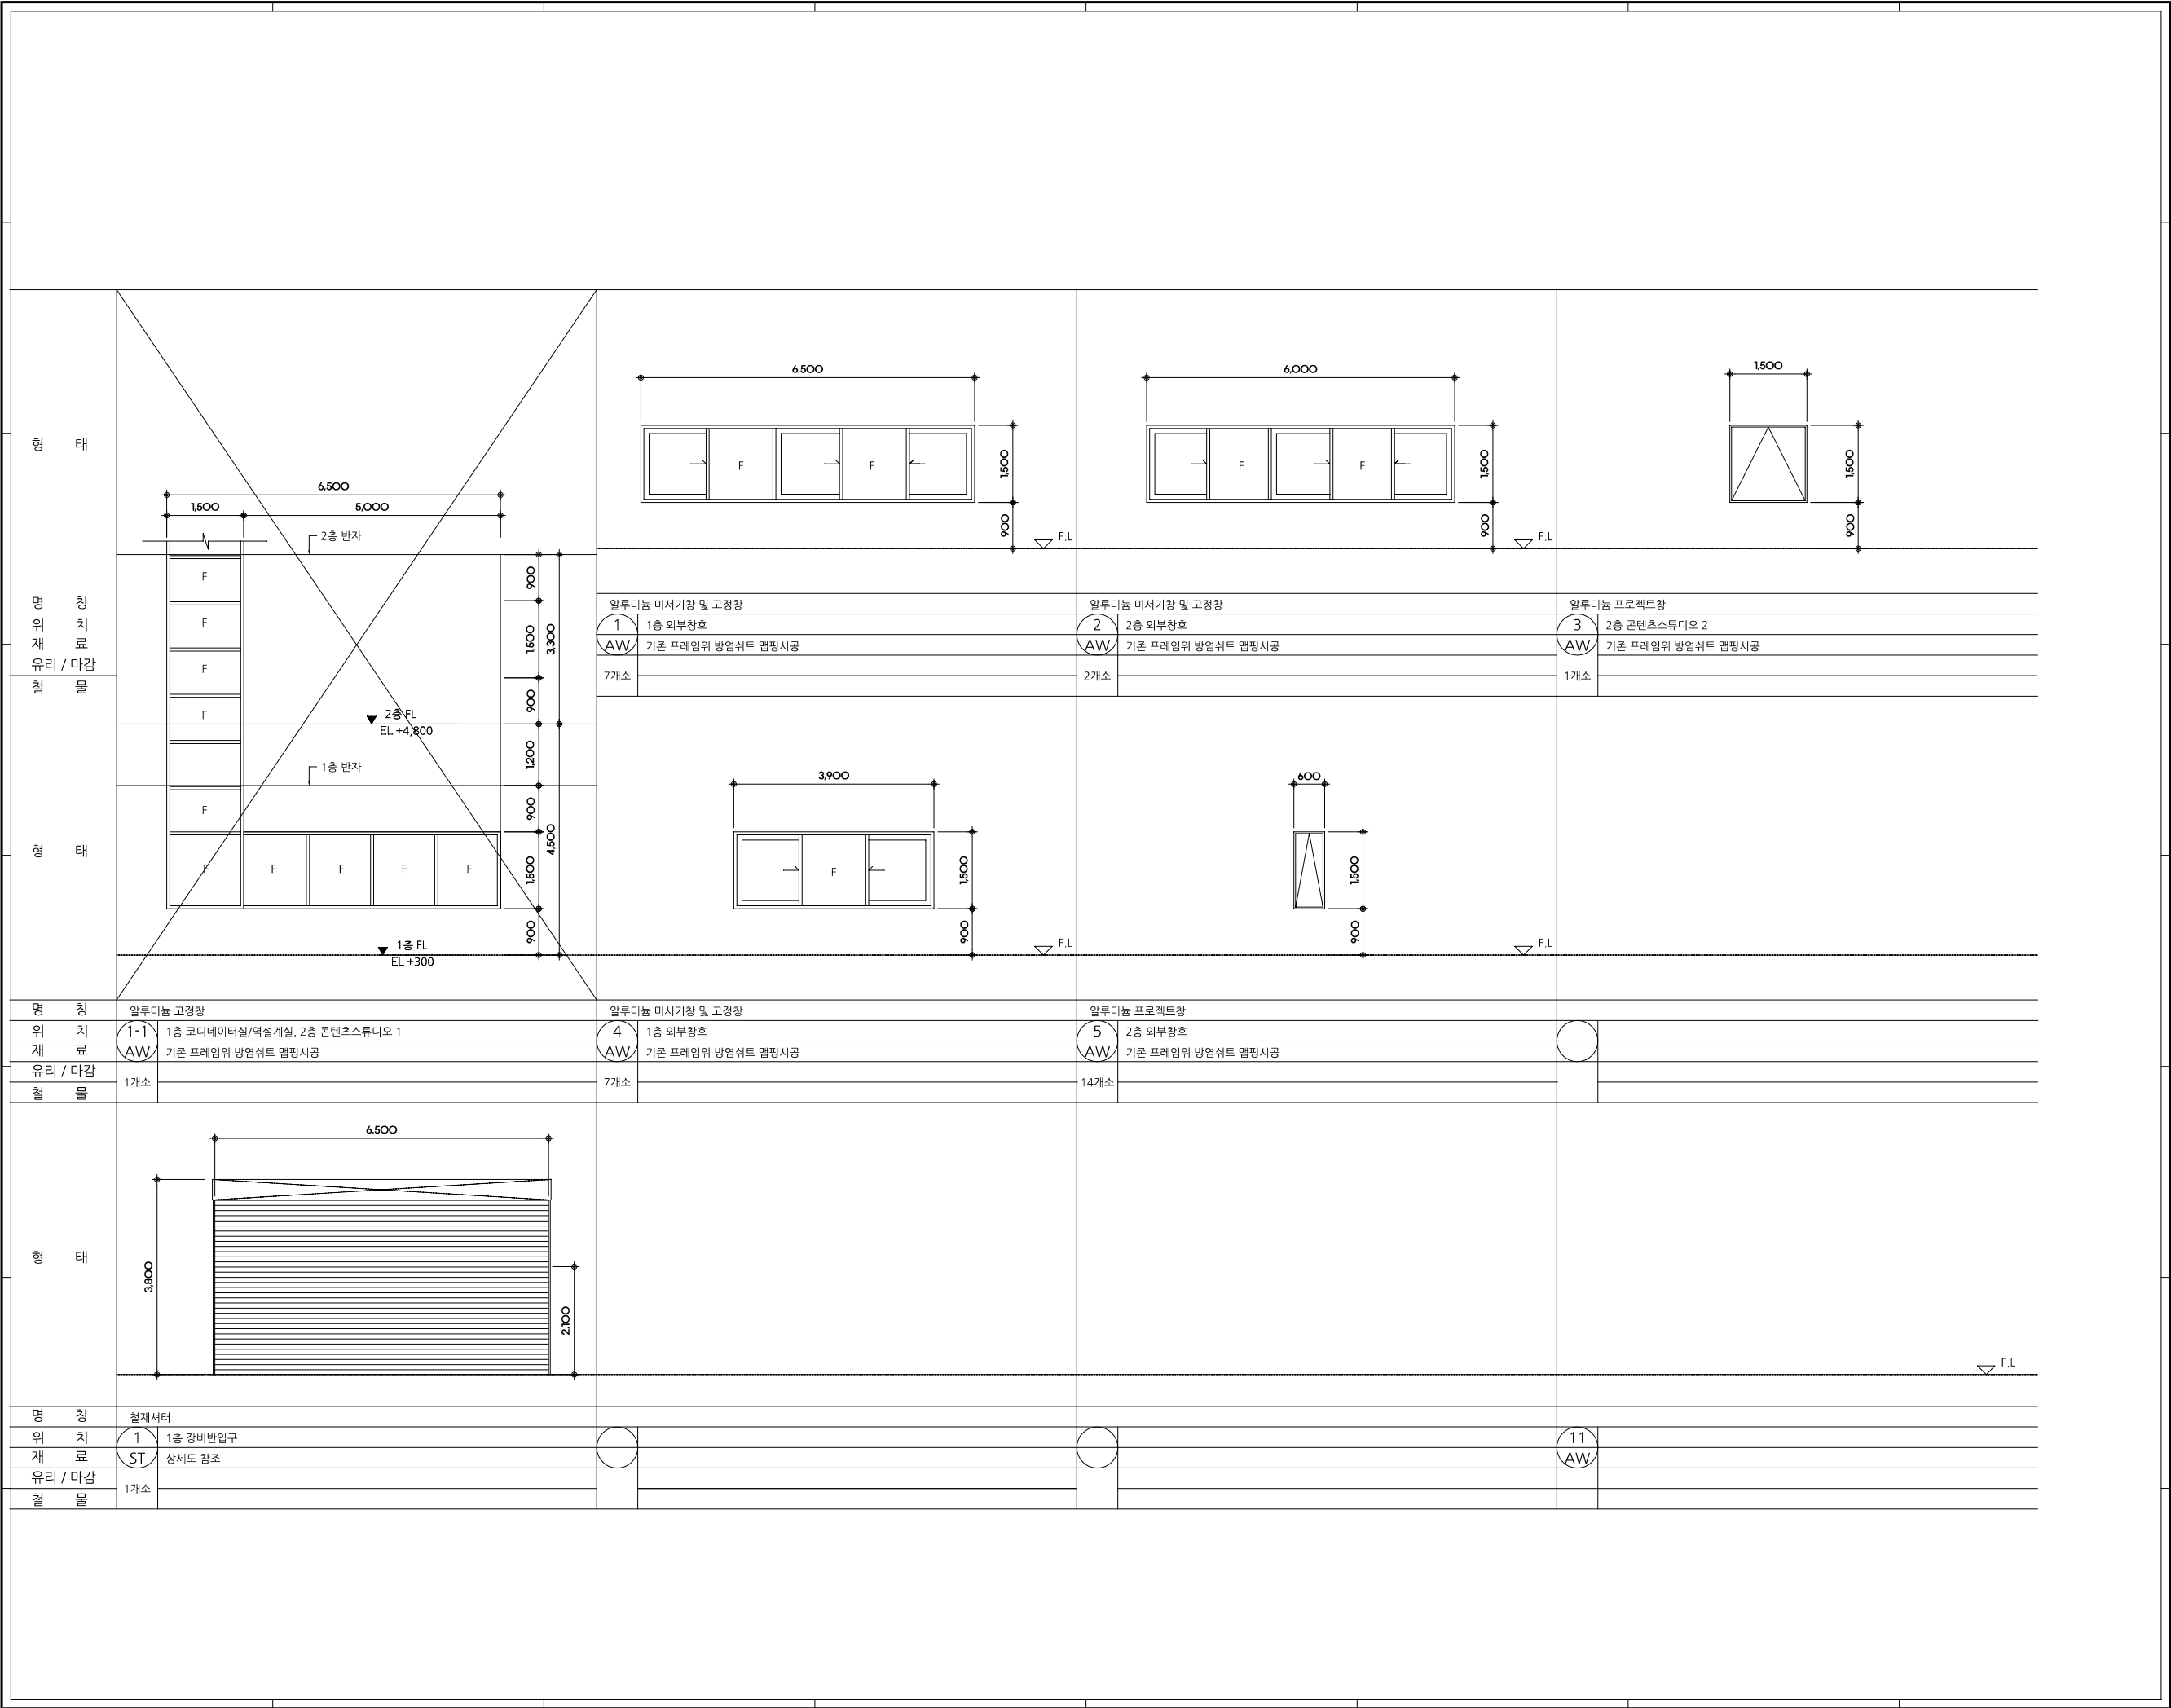

PROJECT TITLE	
피지컬 시리빙센터 구축 공사	
Date.	
No.	Revision
-	-
-	-
-	-
-	-
-	-
-	-
-	-
-	-
-	-
NOTE	
Structure	
Mechanical	
Electrical	
Fire Protection	
Civil	
Landscape	
南北 建築士事務所 建築士 鄭 範 洙 전북 전주시 완산구 서신로57 7층 TEL : 063)247-7787 FAX : 063)247-7786 E-MAIL : nba2007@daum.net	
SHEET TITLE	
기존 창호도1	
DESIGN BY	SCALE
CHECKED BY	A3 1/120
APPROVED BY	DATE
SHEET NO.	SHEET NO.
A- 213	

PROJECT TITLE



피지컬 시리빙센터 구축 공사

Date.

No. Revision

-	
-	
-	
-	
-	
-	
-	
-	
-	
-	

NOTE

- 시험성적서

Structure


Mechanical

Electrical

Fire Protection

Civil

Landscape

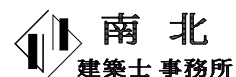

建築士 鄭 範 洙

전북 전주시 완산구 서신로57 7층

TEL : 063)247-7787

FAX : 063)247-7786

E-MAIL : nba2007@daum.net

SHEET TITLE

경량벽체 상세도1

DESIGN BY

SCALE

A3 1/100

CHECKED BY


DATE

APPROVED BY


SHEET NO.

SERIAL NO.

A- 214

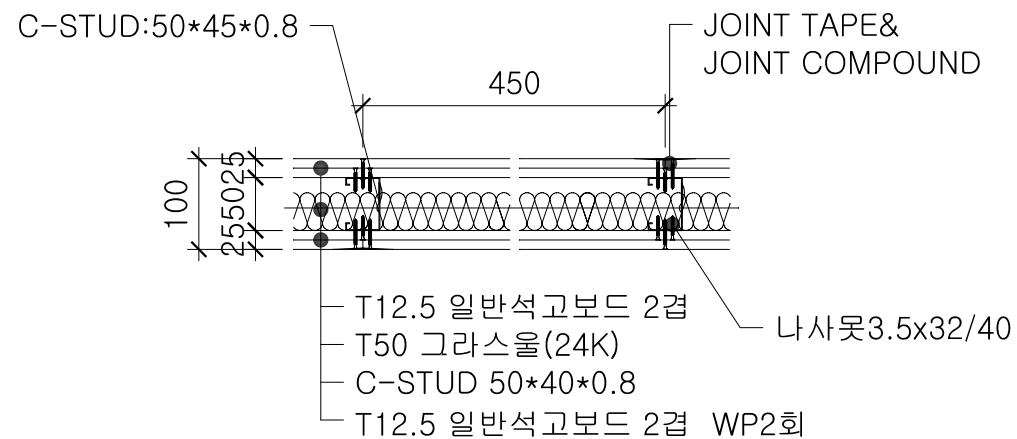


DW2 평면도

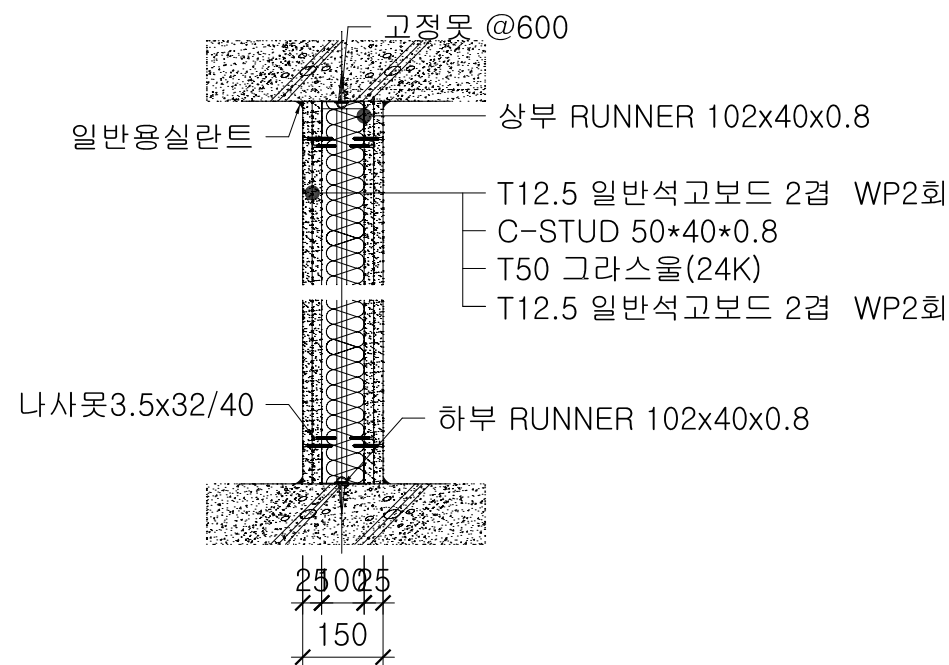


DW2 단면도

바닥 벽체 천정 연결부 실리콘 코킹(소음방지)

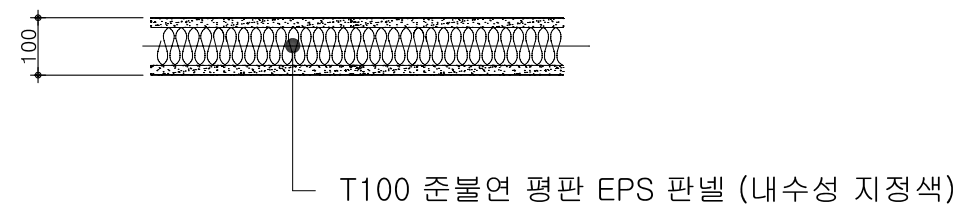


PN1 평면도

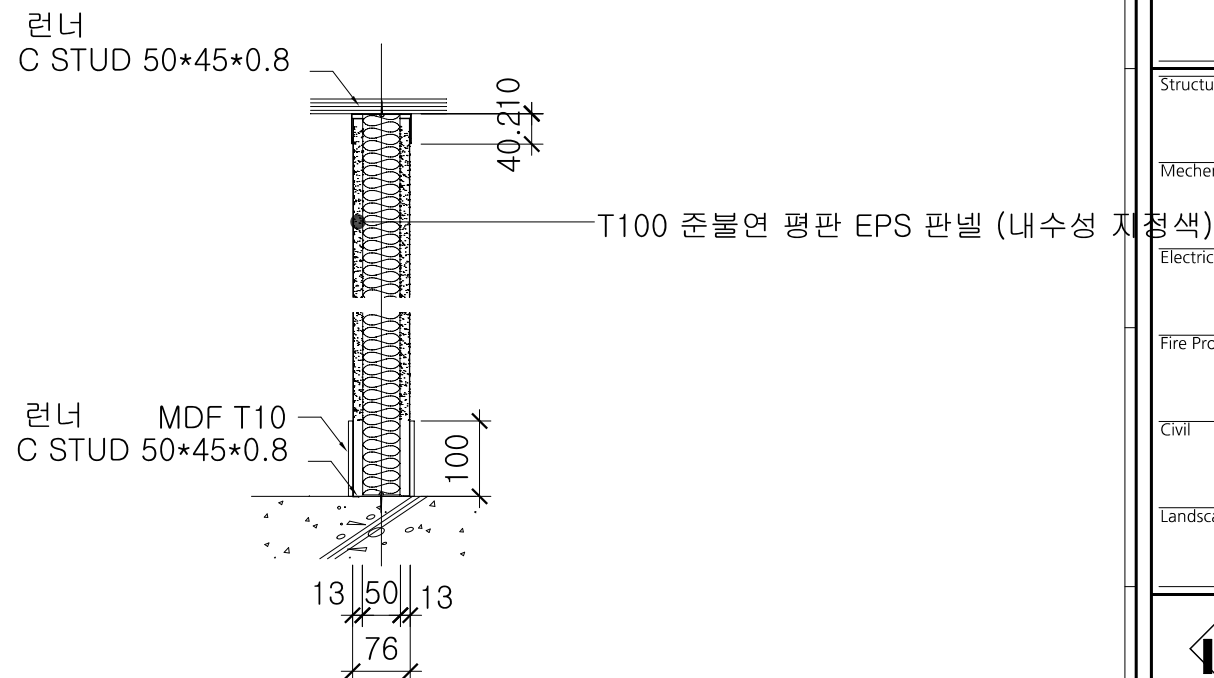


PN1 단면도

바닥 벽체 천정 연결부 실리콘 코킹(수밀성 확보)

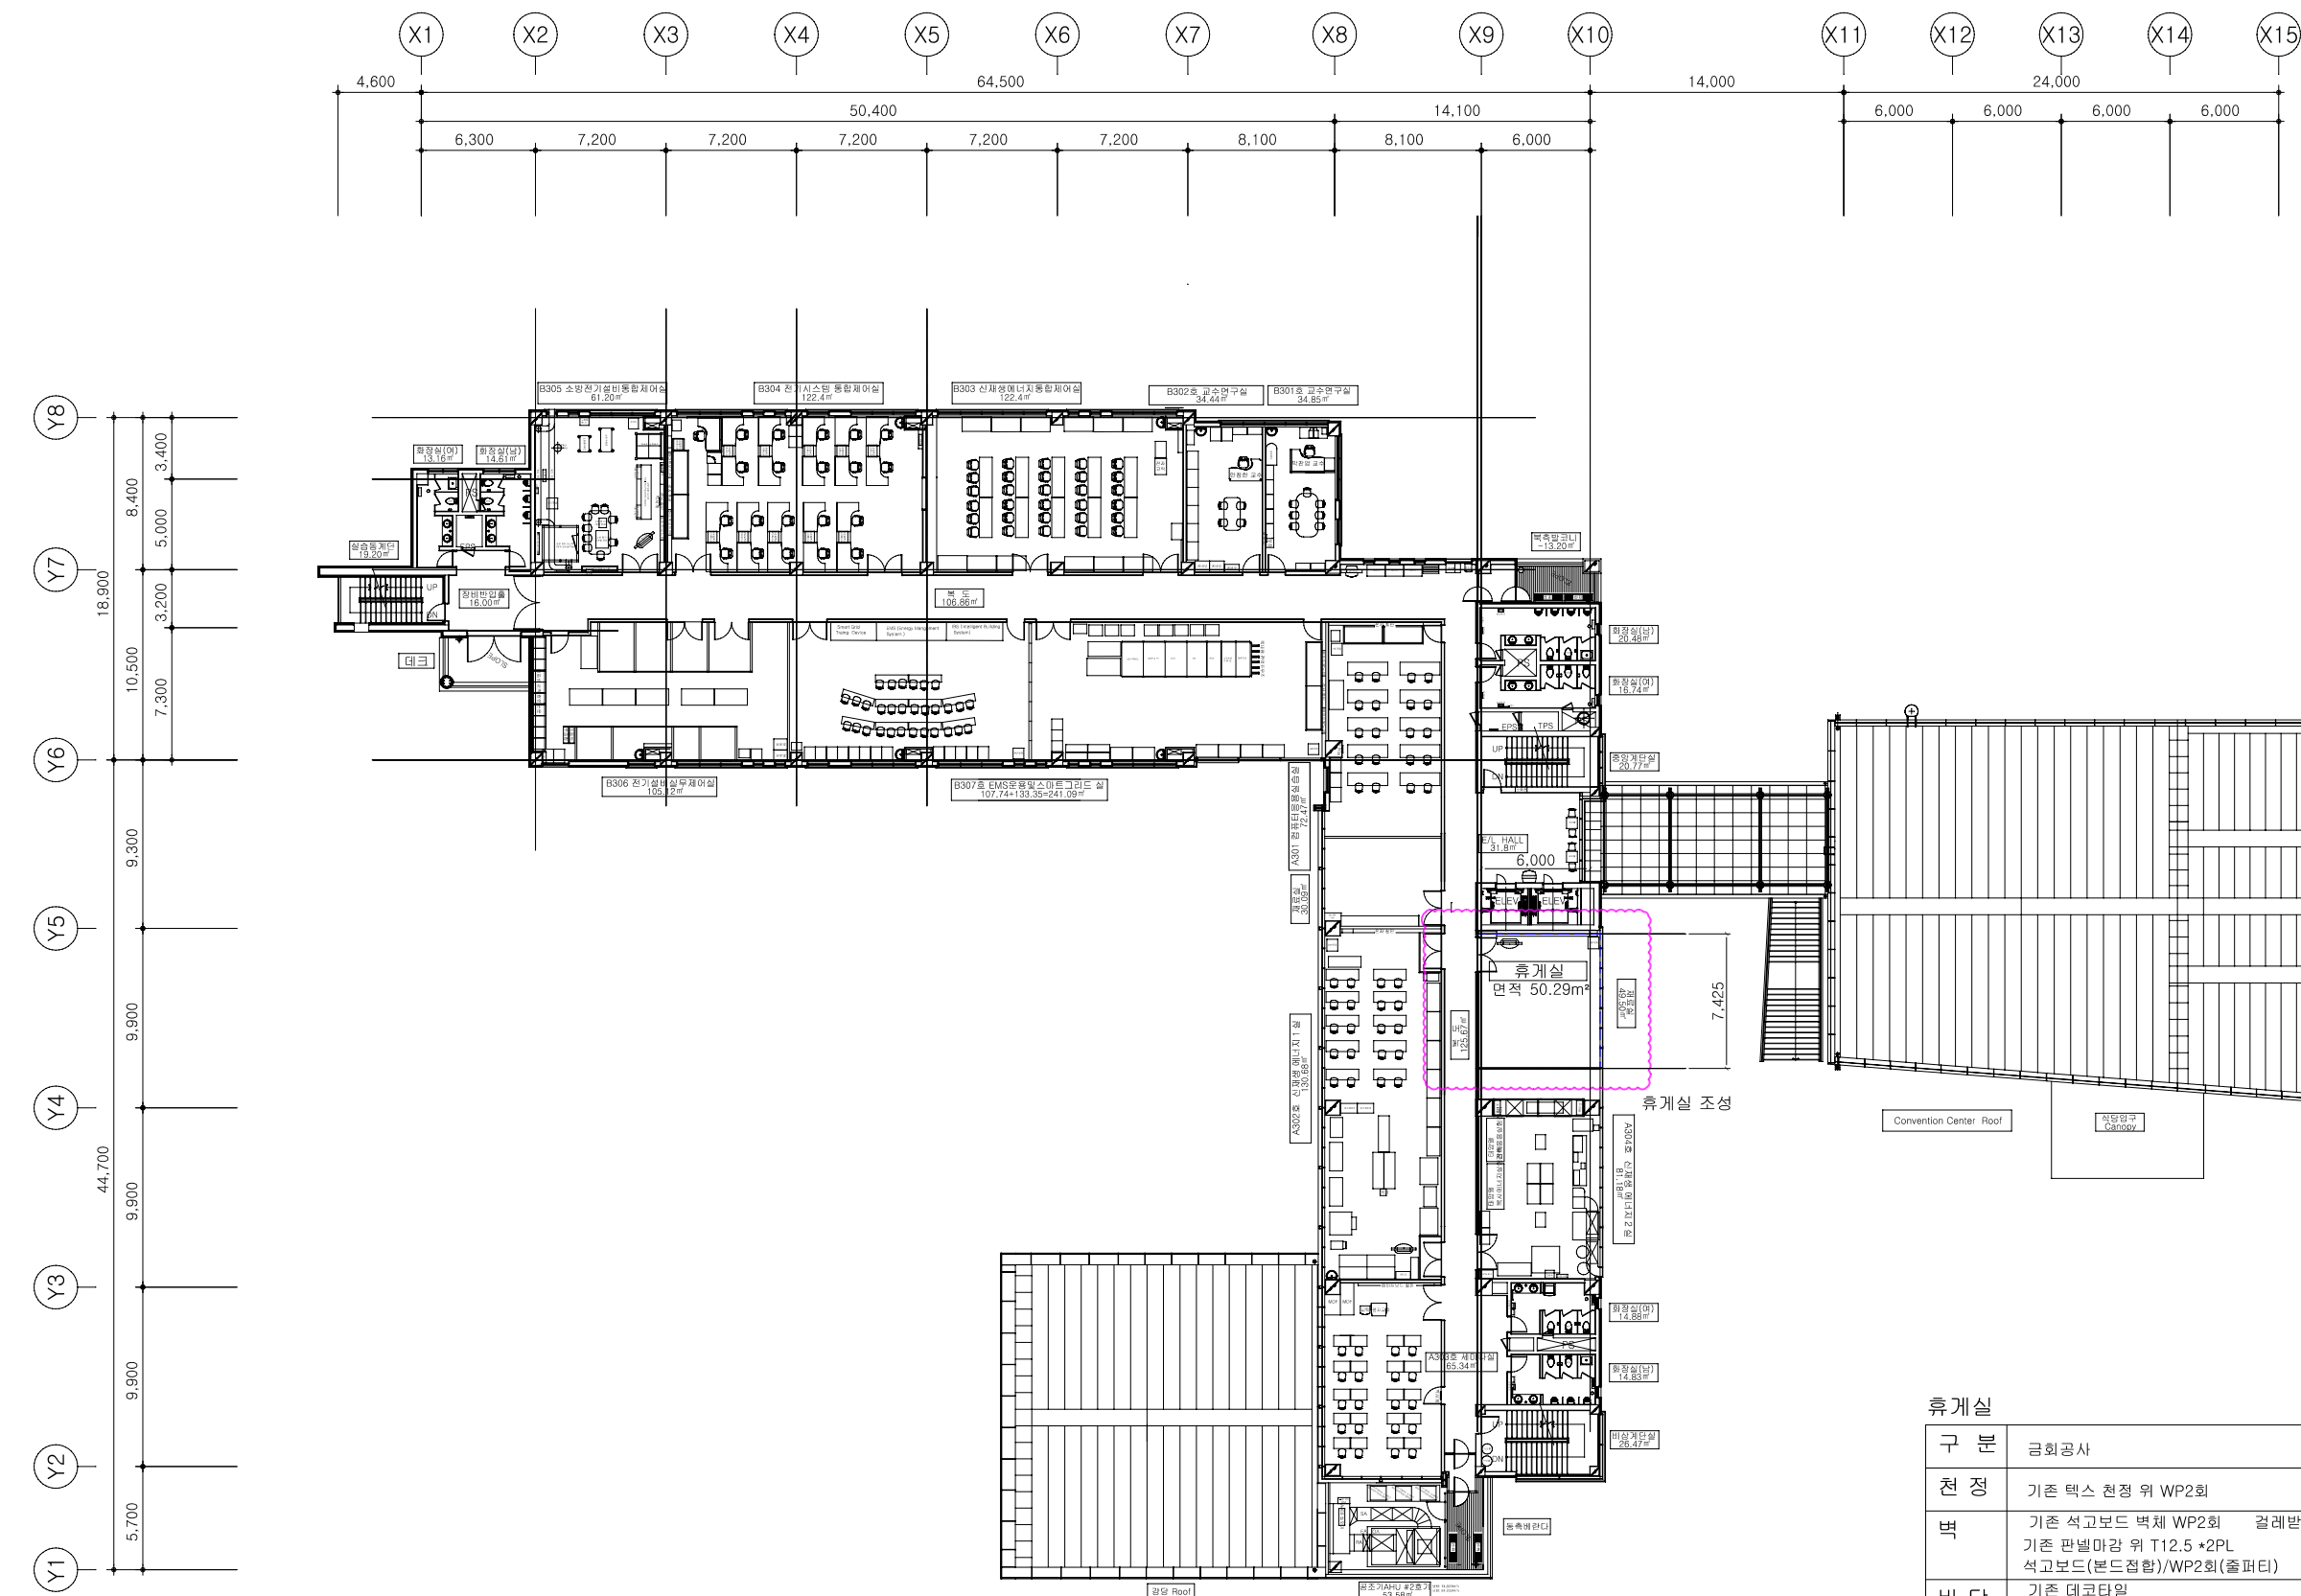

3층 공사 범위표
1. 휴게소 조성

구분	금회공사
천정	기존 텍스 천정 위 WP2회
표	기존 석고보드 벽체 WP2회 걸레받이 MDF 기존 판넬마감 위 T12.5 * 2PL 석고보드(본드접합)/WP2회(줄퍼티)
바닥	기존 데코타일 바탕청소 실시

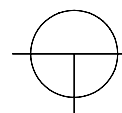

변경후 3층평면도

1/400

PROJECT TITLE



피지컬 시리빙센터 구축 공사

Date.

No. Revision

-	-
-	-
-	-
-	-
-	-
-	-
-	-
-	-
-	-
-	-

NOTE

Structure


Mechanical

Electrical

Fire Protection

Civil

Landscape

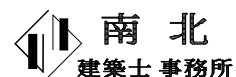

建築士 鄭 範 洙

전북 전주시 완산구 서신로57 7층
TEL : 063)247-7787
FAX : 063)247-7786
E-MAIL : nba2007@daum.net

SHEET TITLE

변경후 3층평면도

DESIGN BY

SCALE

A3 1/400

CHECKED BY


DATE

APPROVED BY

SHEET NO.


SERIAL NO.

A- 300

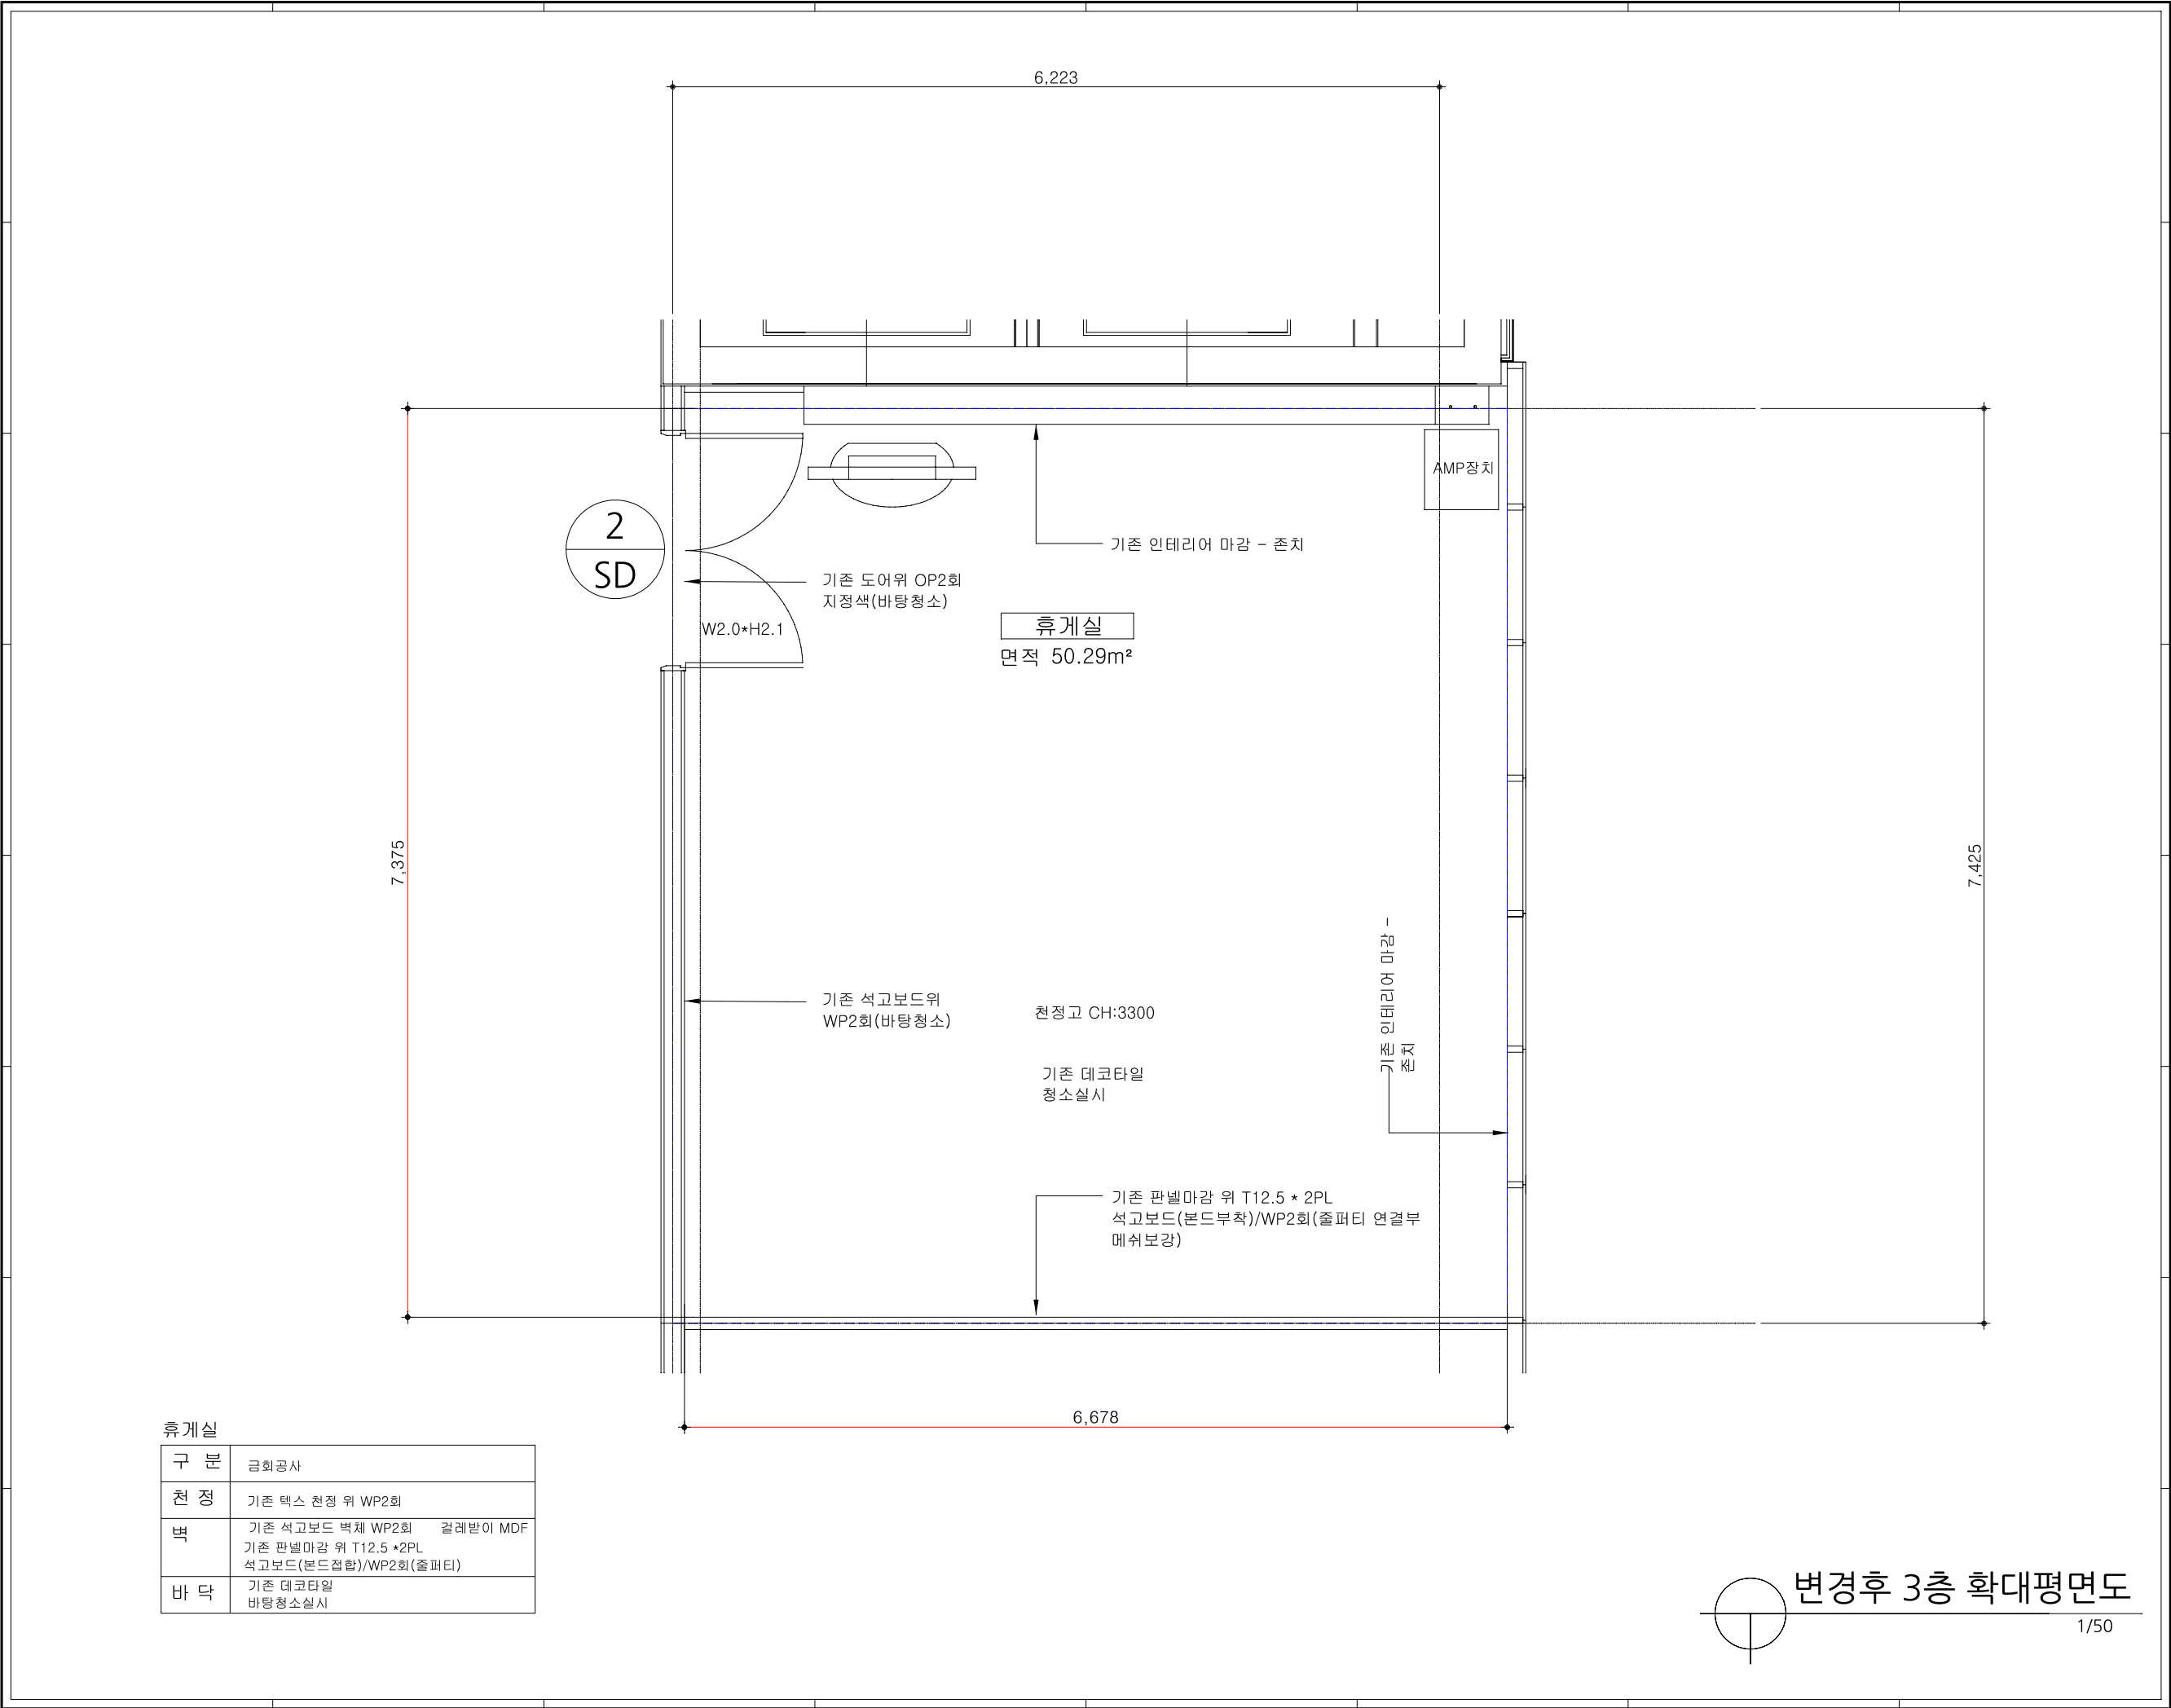

휴게실

구 분	금회공사
천 정	기존 텍스 천정 위 WP2회
벽	기존 석고보드 벽체 WP2회 기존 판넬마감 위 T12.5 * 2PL 석고보드(본드접합)/WP2회(줄퍼티)
바 닥	기존 데코타일 바탕청소실시

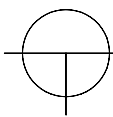

변경후 3층 확대평면도

1/50

PROJECT TITLE



피지컬 시리빙센터 구축 공사

Date.

No.	Revision
-	-
-	-
-	-
-	-
-	-
-	-
-	-
-	-
-	-

NOTE

Structure

Mechanical

Electrical

Fire Protection

Civil

Landscape



南北
建築士事務所


建築士 鄭 範 洙

전북 전주시 완산구 서신로57 7층
TEL : 063)247-7787
FAX : 063)247-7786
E-MAIL : nba2007@daum.net

SHEET TITLE

변경후 3층 확대평면도

DESIGN BY	SCALE
CHECKED BY	A3 1/50
APPROVED BY	DATE
SHEET NO.	SHEET NO.
SERIAL NO.	A- 301

 [illegible]

NOTE

Structure
Mechanical
Electrical
Fire Protection
Civil
Landscape




전북 전주시 완산구 서신로57 7층
TEL : 063)247-7787
FAX : 063)247-7786
E-MAIL : nba2007@daum.net

SHEET TITLE

휴게실 창호도

DESIGN BY	SCALE A3 1/80
CHECKED BY	DATE
APPROVED BY	SHEET NO.
SERIAL NO.	A- 302

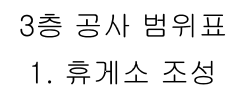

휴게실	
구 분	철거 및 시공
천 정	기존 텍스 천정
벽	기존 인테리어 마감 기존 판넬마감
바 닥	기존 데코타일 마감

기존 3층평면도



피지컬 AI리빙센터 구축 공사

Date.

[illegible]

NOTE

Structure


Mechanical

Electrical

Fire Protection

Civil

Landscape

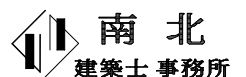

建築士 鄭 範 洙

전북 전주시 완산구 서신로57 7층
TEL : 063)247-7787
FAX : 063)247-7786
E-MAIL : nba2007@daum.net

SHEET TITLE

기존 3층평면도

DESIGN BY


SCALE	
A3	1/400
DATE	

APPROVED BY

SHEET NO. _____


SERIAL NO.	
------------	--

A- 303

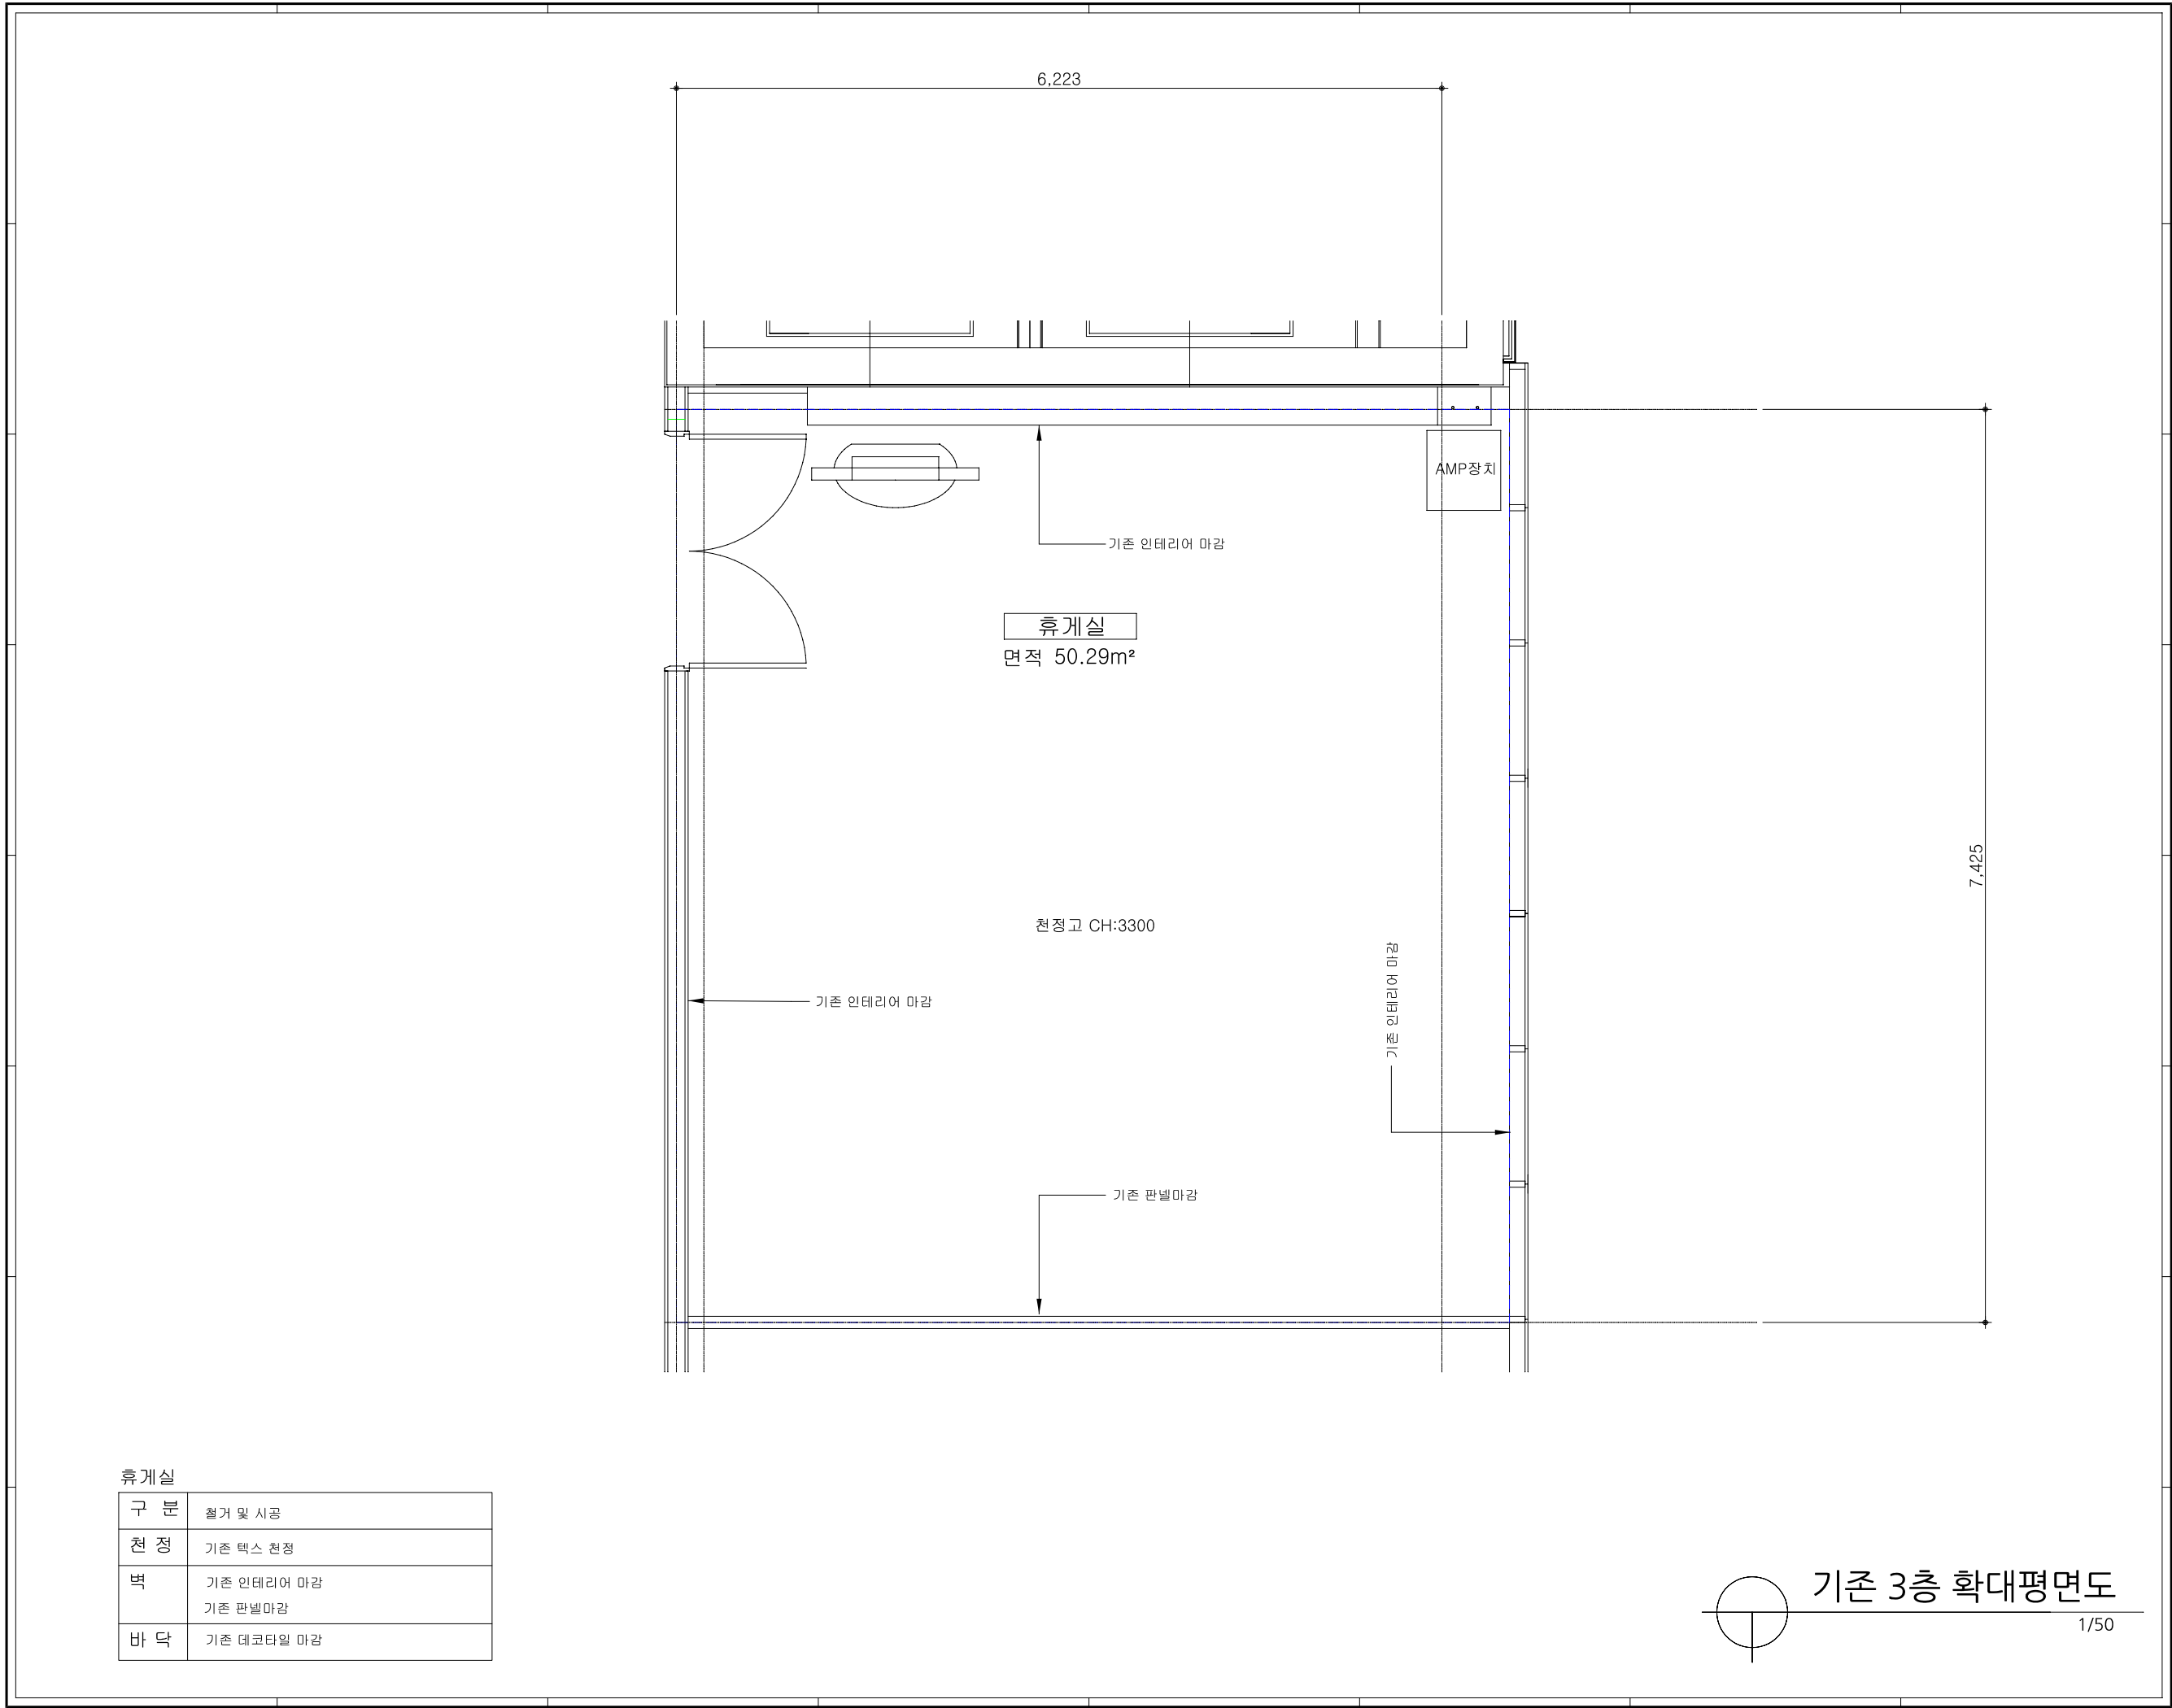

휴게실

구 분	철거 및 시공
천 정	기존 텍스 천정
벽	기존 인테리어 마감 기존 판넬마감
바 닥	기존 데코타일 마감

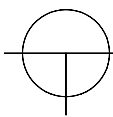

기존 3층 확대평면도

1/50

PROJECT TITLE



피지컬 시리빙센터 구축 공사

Date.

No. Revision

NOTE

Structure


Mechanical

Electrical

Fire Protection

Civil

Landscape

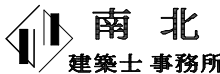

建築士 鄭 範 洙

전북 전주시 완산구 서신로57 7층

TEL : 063)247-7787

FAX : 063)247-7786

E-MAIL : nba2007@daum.net

SHEET TITLE

기존 3층 확대평면도

DESIGN BY

SCALE

A3 1/50

CHECKED BY


DATE

APPROVED BY

SHEET NO.

SERIAL NO.

A- 304

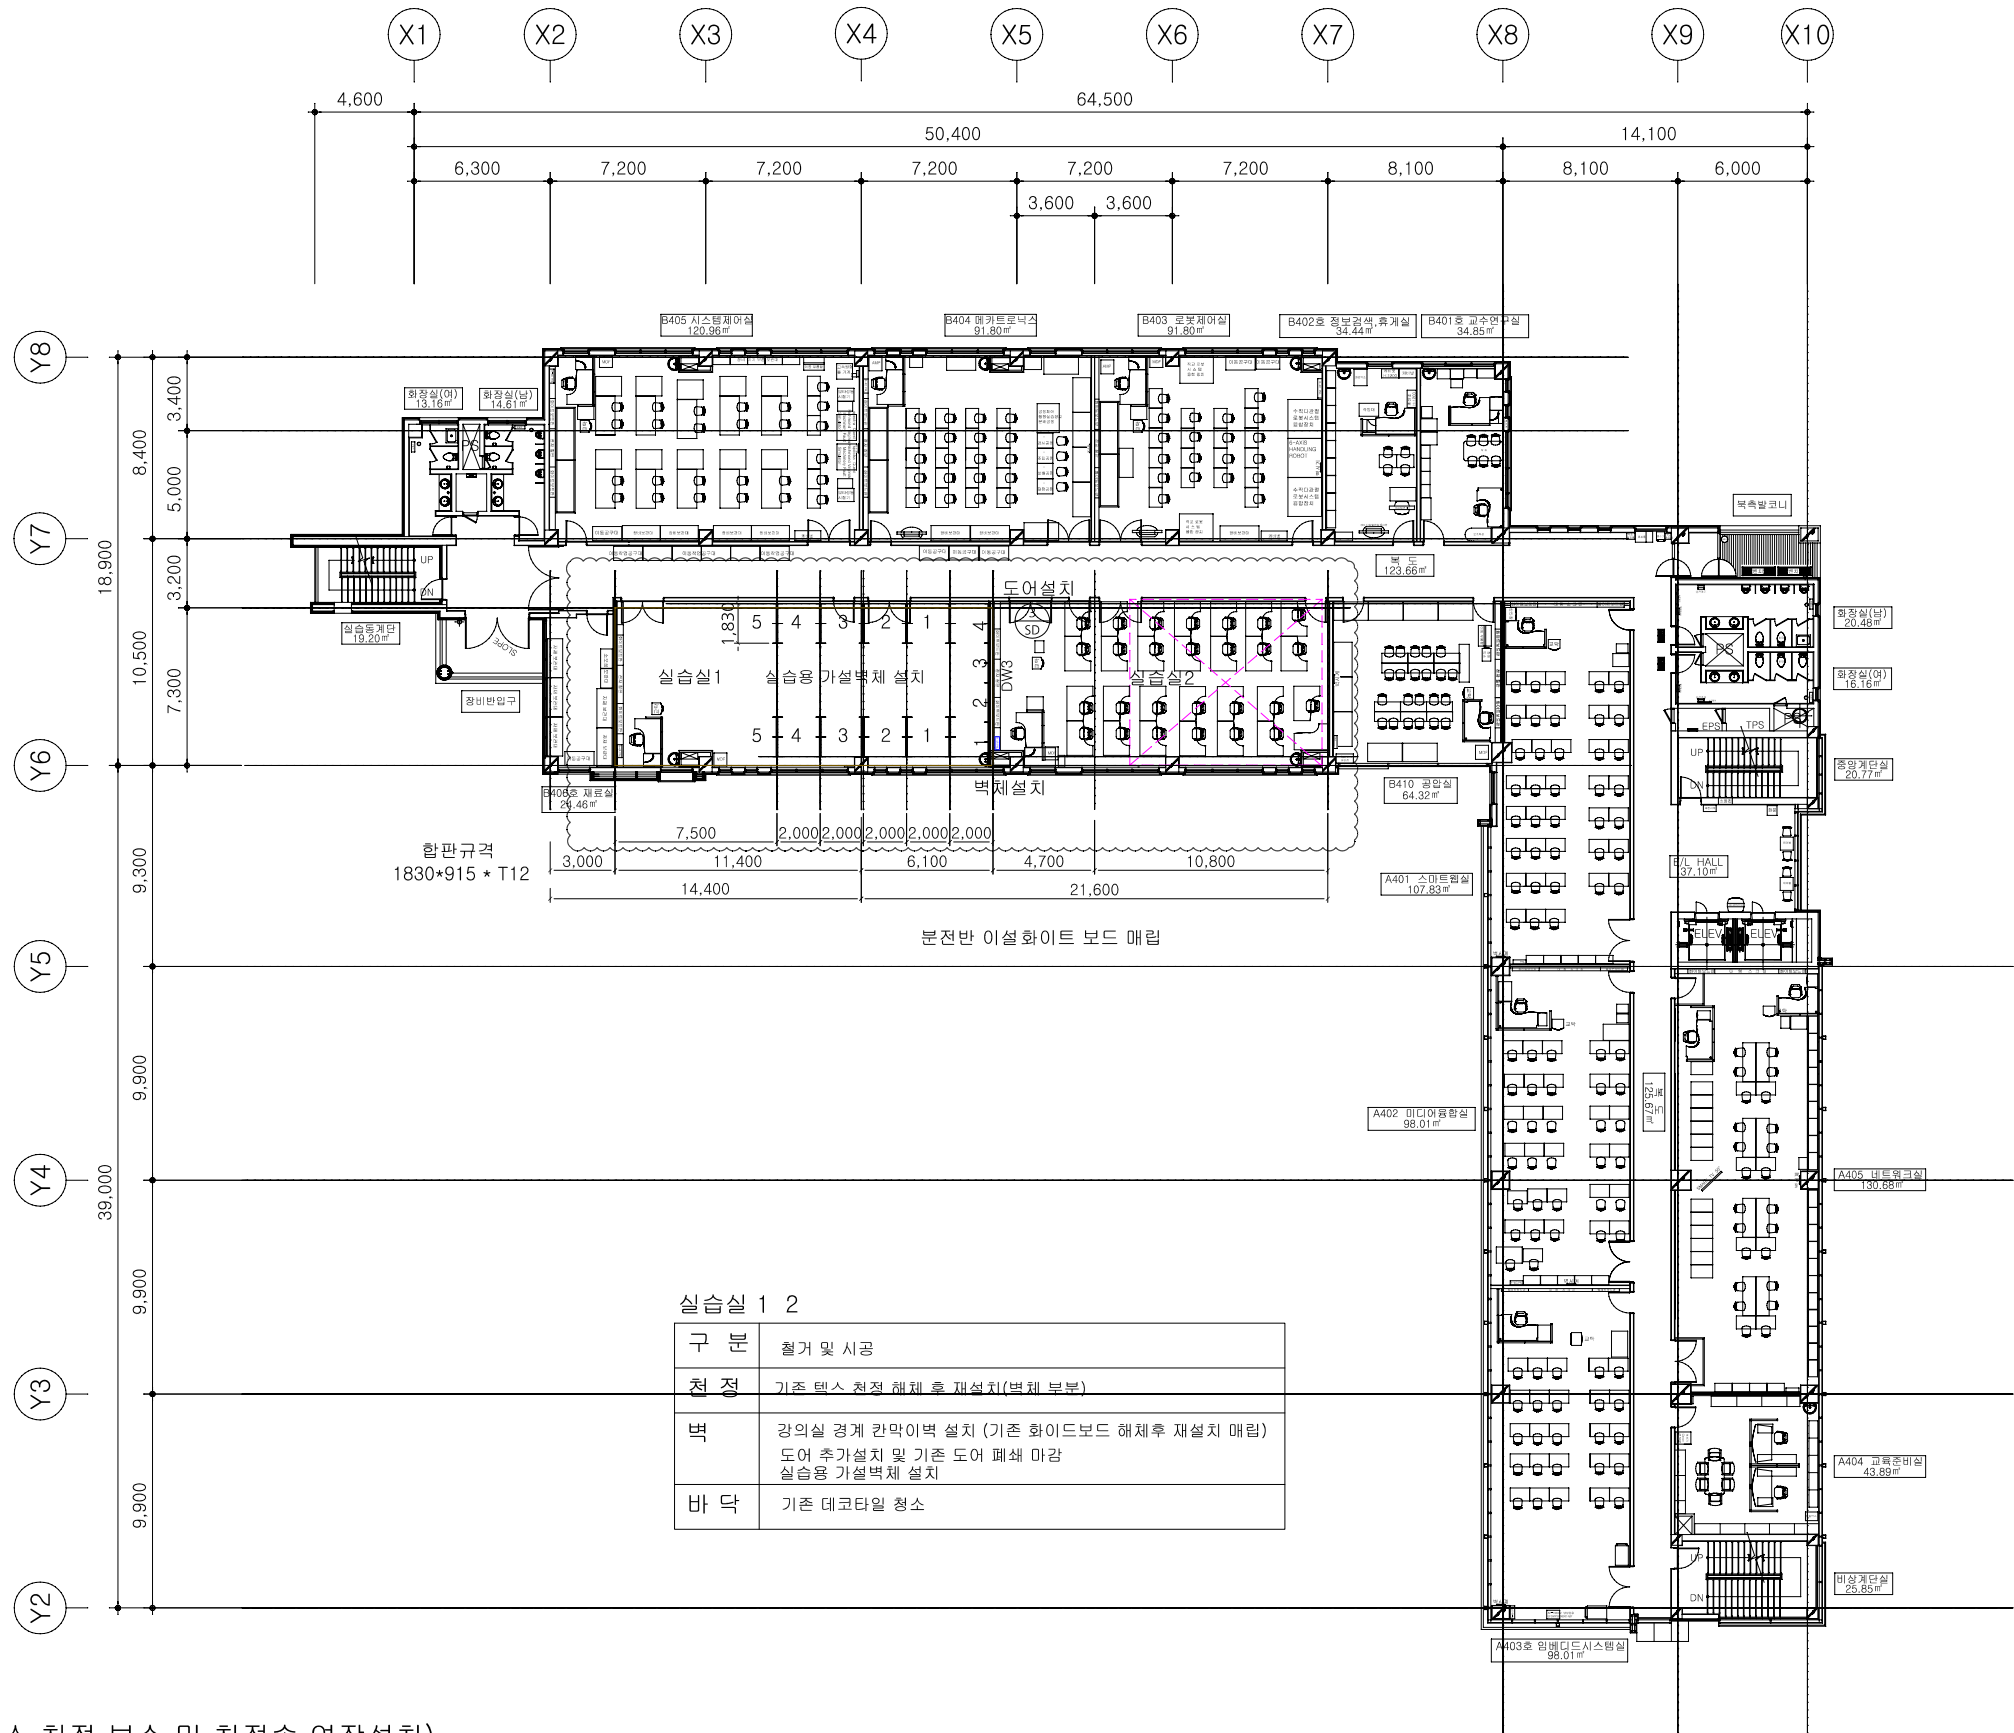

4층 공사 범위표

1. 칸막이벽 이설 (바닥청소,천정 보수 및 천정속 연장설치)
2. 분전반 이설 기능 변경 강의실1 → 실습실
3. 조명등 S/W조정
4. 실습장 부스 설치
- 5.후로어 콘센트 전원 연결

PROJECT TITLE



피지컬 시리빙센터 구축 공사

Date.

No. Revision

-
-
-
-
-
-
-
-
-
-

NOTE

Structure


Mechanical

Electrical

Fire Protection

Civil

Landscape

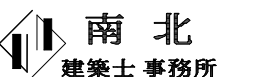

建築士 鄭 範 洙

전북 전주시 완산구 서신로57 7층

TEL : 063)247-7787

FAX : 063)247-7786

E-MAIL : nba2007@daum.net

SHEET TITLE

변경후 4층평면도

DESIGN BY

SCALE

A3 1/350

CHECKED BY


DATE



APPROVED BY

SHEET NO.



SERIAL NO.

A- 400

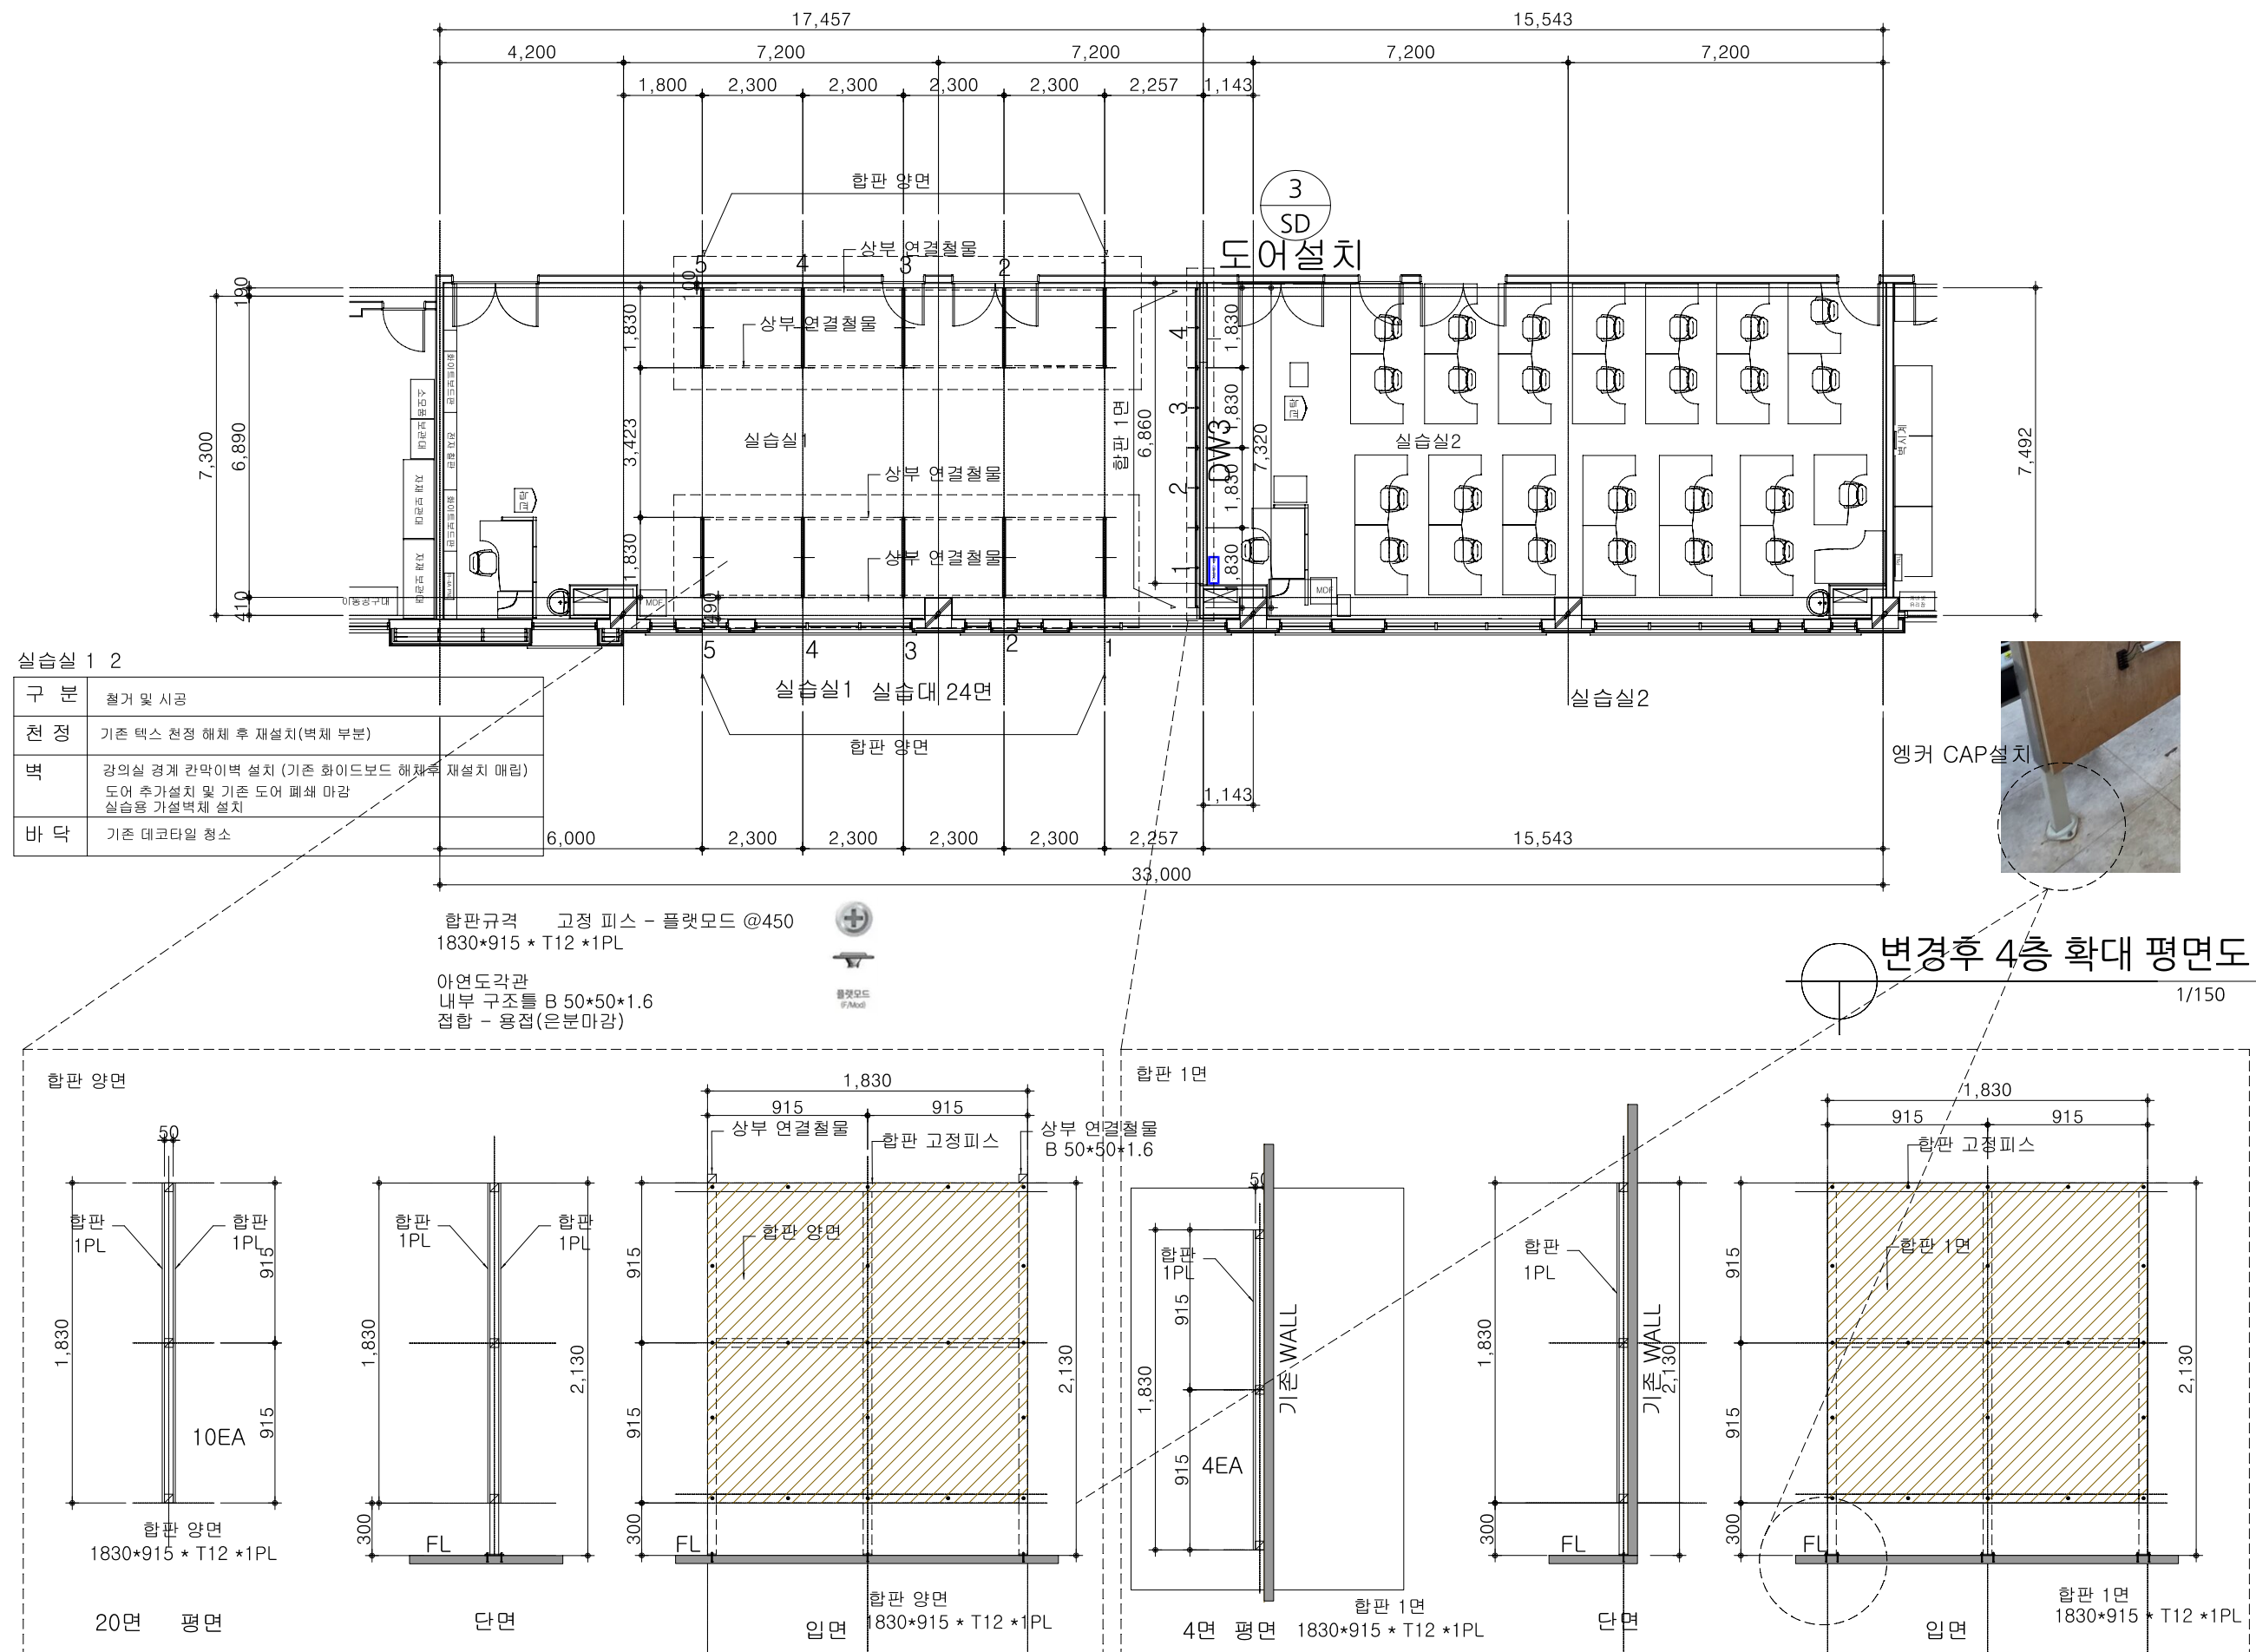

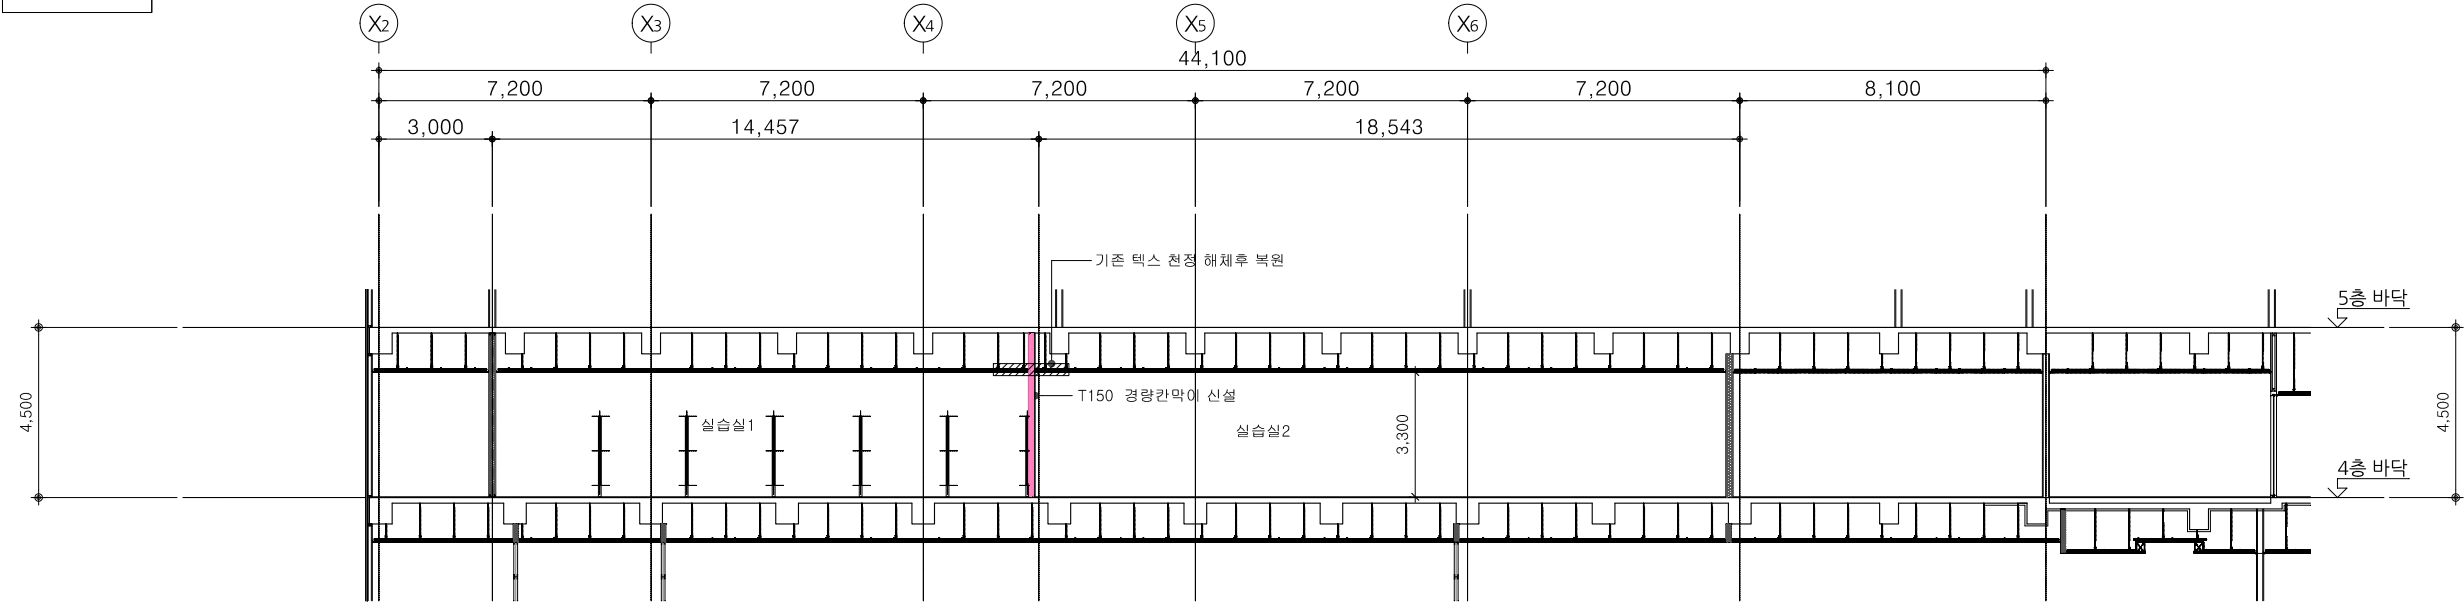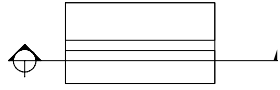

횡단면도 - 1 (변경후)
A1: 1/100

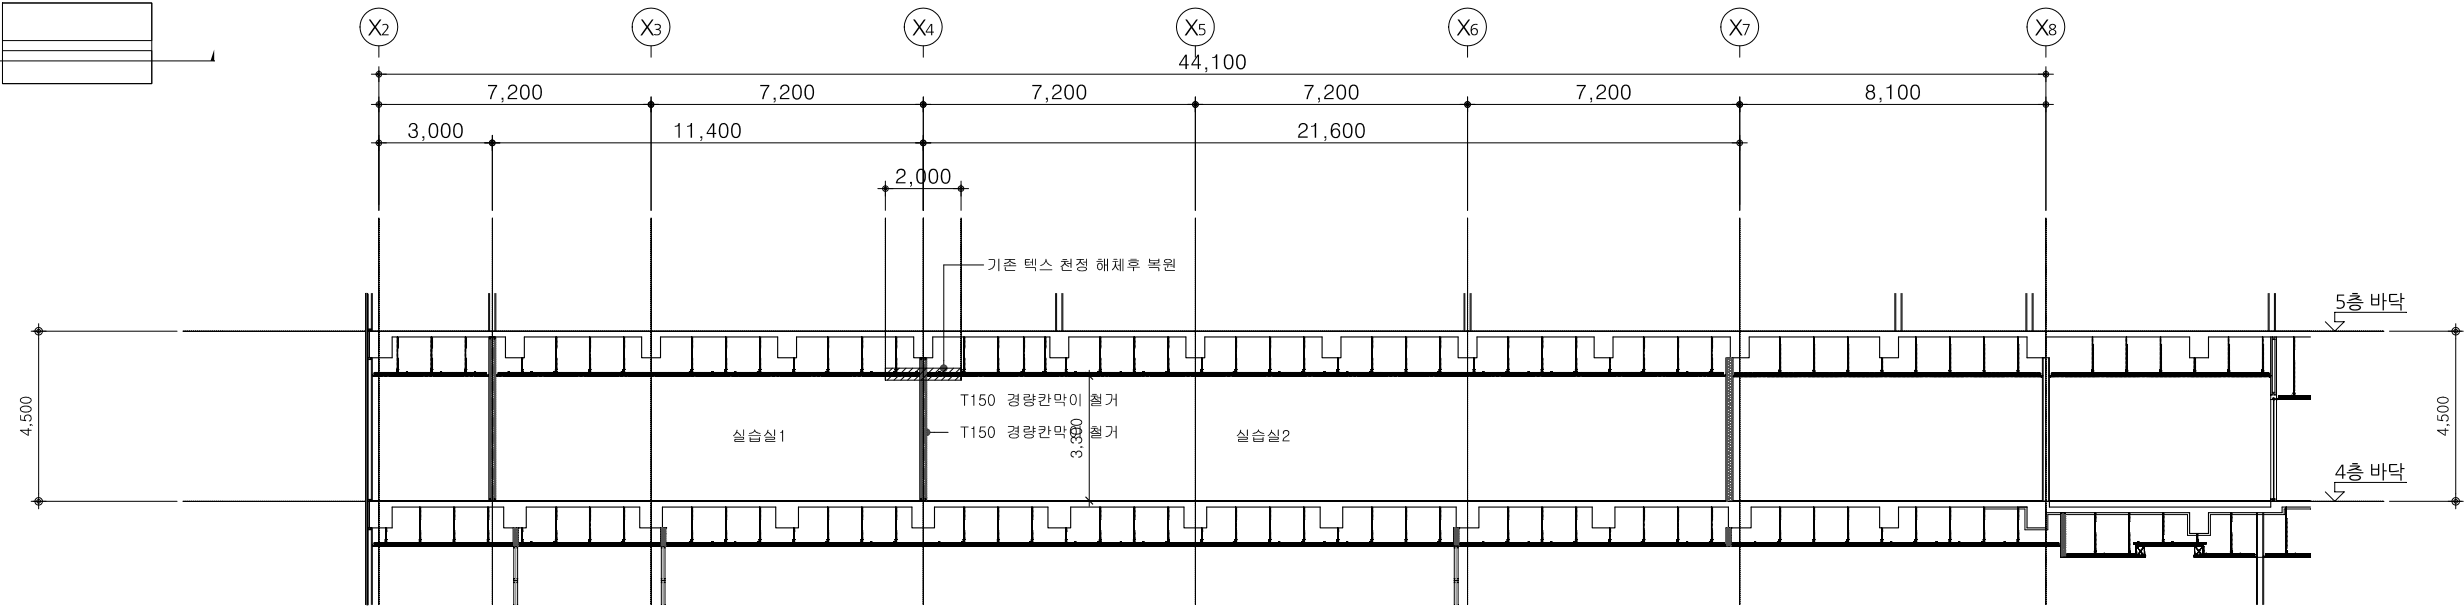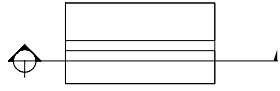

횡단면도 - 1 (변경전)
A1: 1/100

- * 주 기 사 항 *
1. 천정텍스는 경계벽설치를 위해 철거 후 재설치 기존텍스 시공할 것.
 2. 경계벽 이설에 따른 기존 바닥 벽 천정 벽체등 기존벽체 철거에 의한 노출부위 청소

PROJECT TITLE

페이지컬 시리빙센터 구축 공사

Date.	
No.	Revision
-	-
-	-
-	-
-	-
-	-
-	-
-	-
-	-
-	-
NOTE	

Structure

Mechanical

Electrical

Fire Protection

Civil

Landscape

南北
建築士事務所


建築士 鄭 範 洙

전북 전주시 완산구 서신로57 7층
TEL : 063)247-7787
FAX : 063)247-7786
E-MAIL : nba2007@daum.net


SHEET TITLE

변경 전후 횡단면도


DESIGN BY	SCALE A3 1/200
CHECKED BY	DATE
APPROVED BY	SHEET NO.
SERIAL NO.	1 A-402

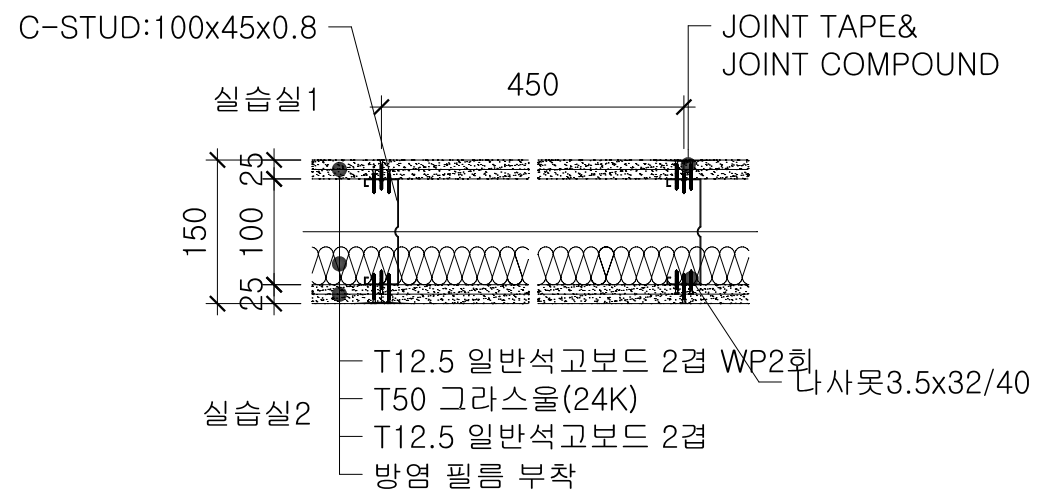

DW3 평면도

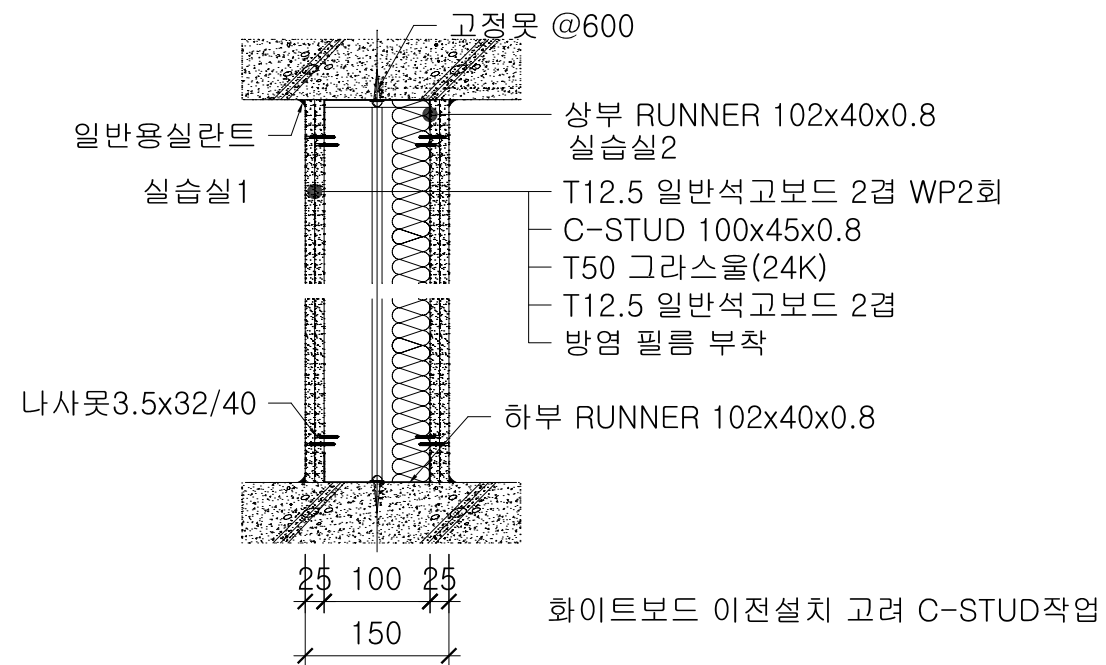

DW3 단면도

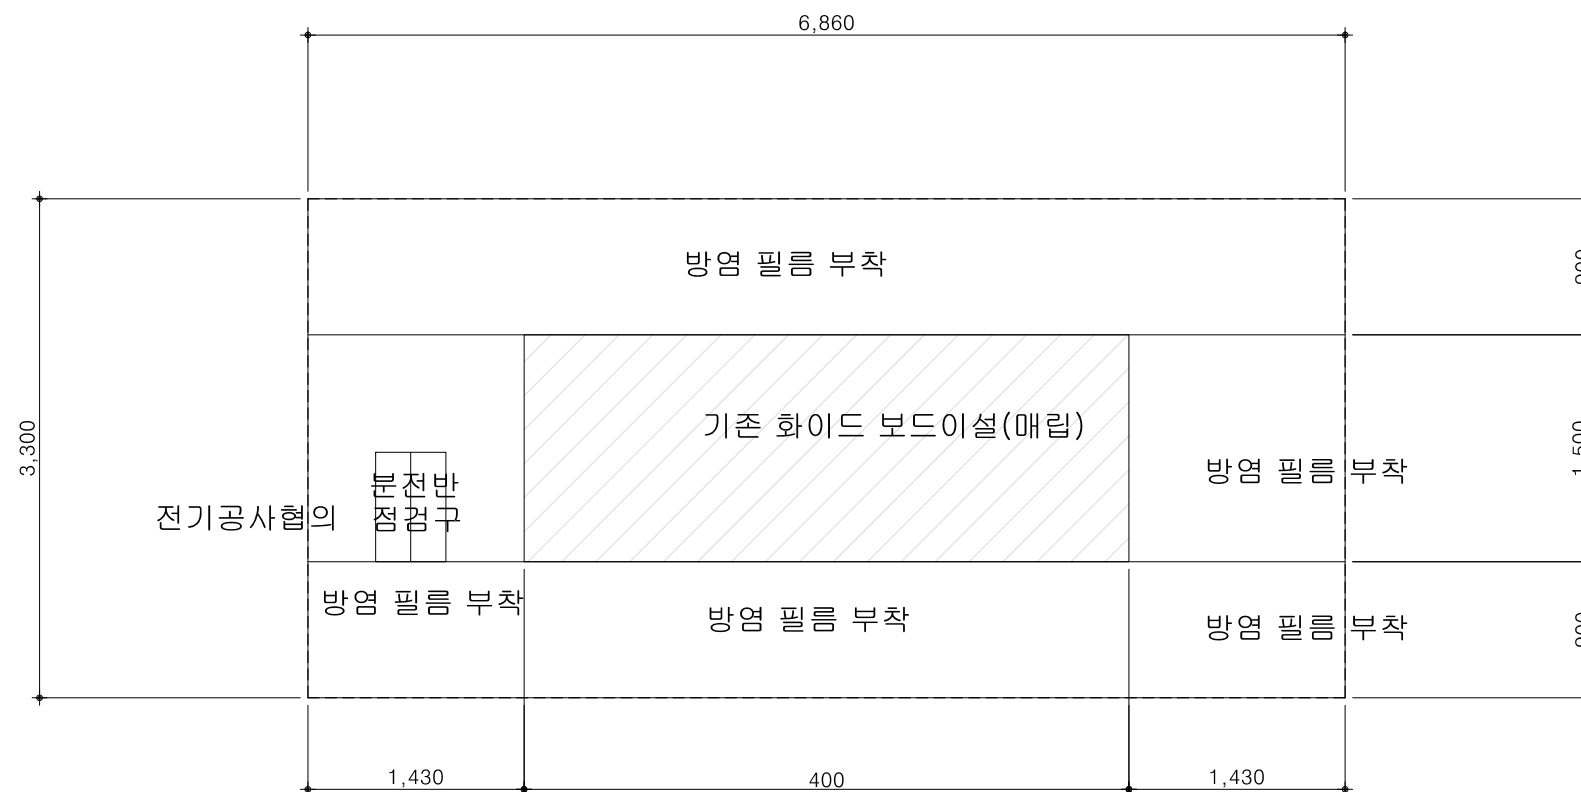

기존 벽체와 동일 시공

벽체 전개도

PROJECT TITLE



피지컬 AI리빙센터 구축 공사

Date.

No. Revision

-	-
-	-
-	-
-	-
-	-
-	-
-	-
-	-
-	-
-	-

NOTE

Structure


Mechanical

Electrical

Fire Protection

Civil

Landscape

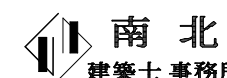

建築士 鄭 範 洙

전북 전주시 완산구 서신로57 7층

TEL : 063)247-7787

FAX : 063)247-7786

E-MAIL : nba2007@daum.net

SHEET TITLE

경량벽체 상세도2

DESIGN BY

SCALE

A3 1/100

CHECKED BY

DATE

APPROVED BY

SHEET NO.

SERIAL NO.

A- 403

형태

2,000

T9 MDF몰딩 (W:200)

2,100

F.L.

F.L.

신설

명칭

철재 양여닫이문

위치

3실습실2

재료

SD45X150X1.6T/방청 후 조합페인트2회

유리 / 마감

1개소양면철판/방청 후 조합페인트

철물

부속철물 일체

형태

F.L.

F.L.

명칭

위치

재료

유리 / 마감

철물

PROJECT TITLE

피지컬 시리빙센터 구축 공사

Date.

No.

Revision

-

-

-

-

-

-

-

-

-

-

NOTE

Structure

Mechanical

Electrical

Fire Protection

Civil

Landscape

南北

建築士事務所

建築士 鄭 範 洙

전북 전주시 완산구 서신로57 7층
TEL : 063)247-7787
FAX : 063)247-7786
E-MAIL : nba2007@daum.net

SHEET TITLE

실습실2 창호도

DESIGN BY

SCALE

CHECKED BY


DATE

APPROVED BY


SHEET NO.

SERIAL NO.

A- 404

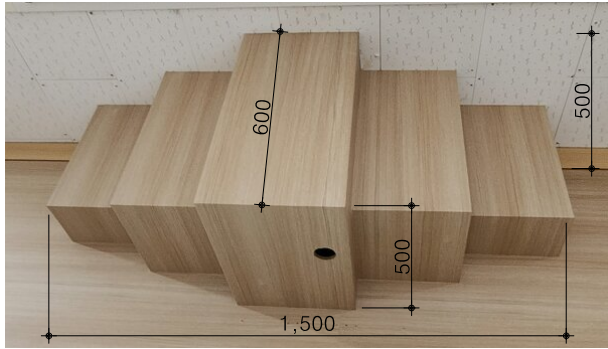

천정장식 철거
T12.5*2PL 위 필름지

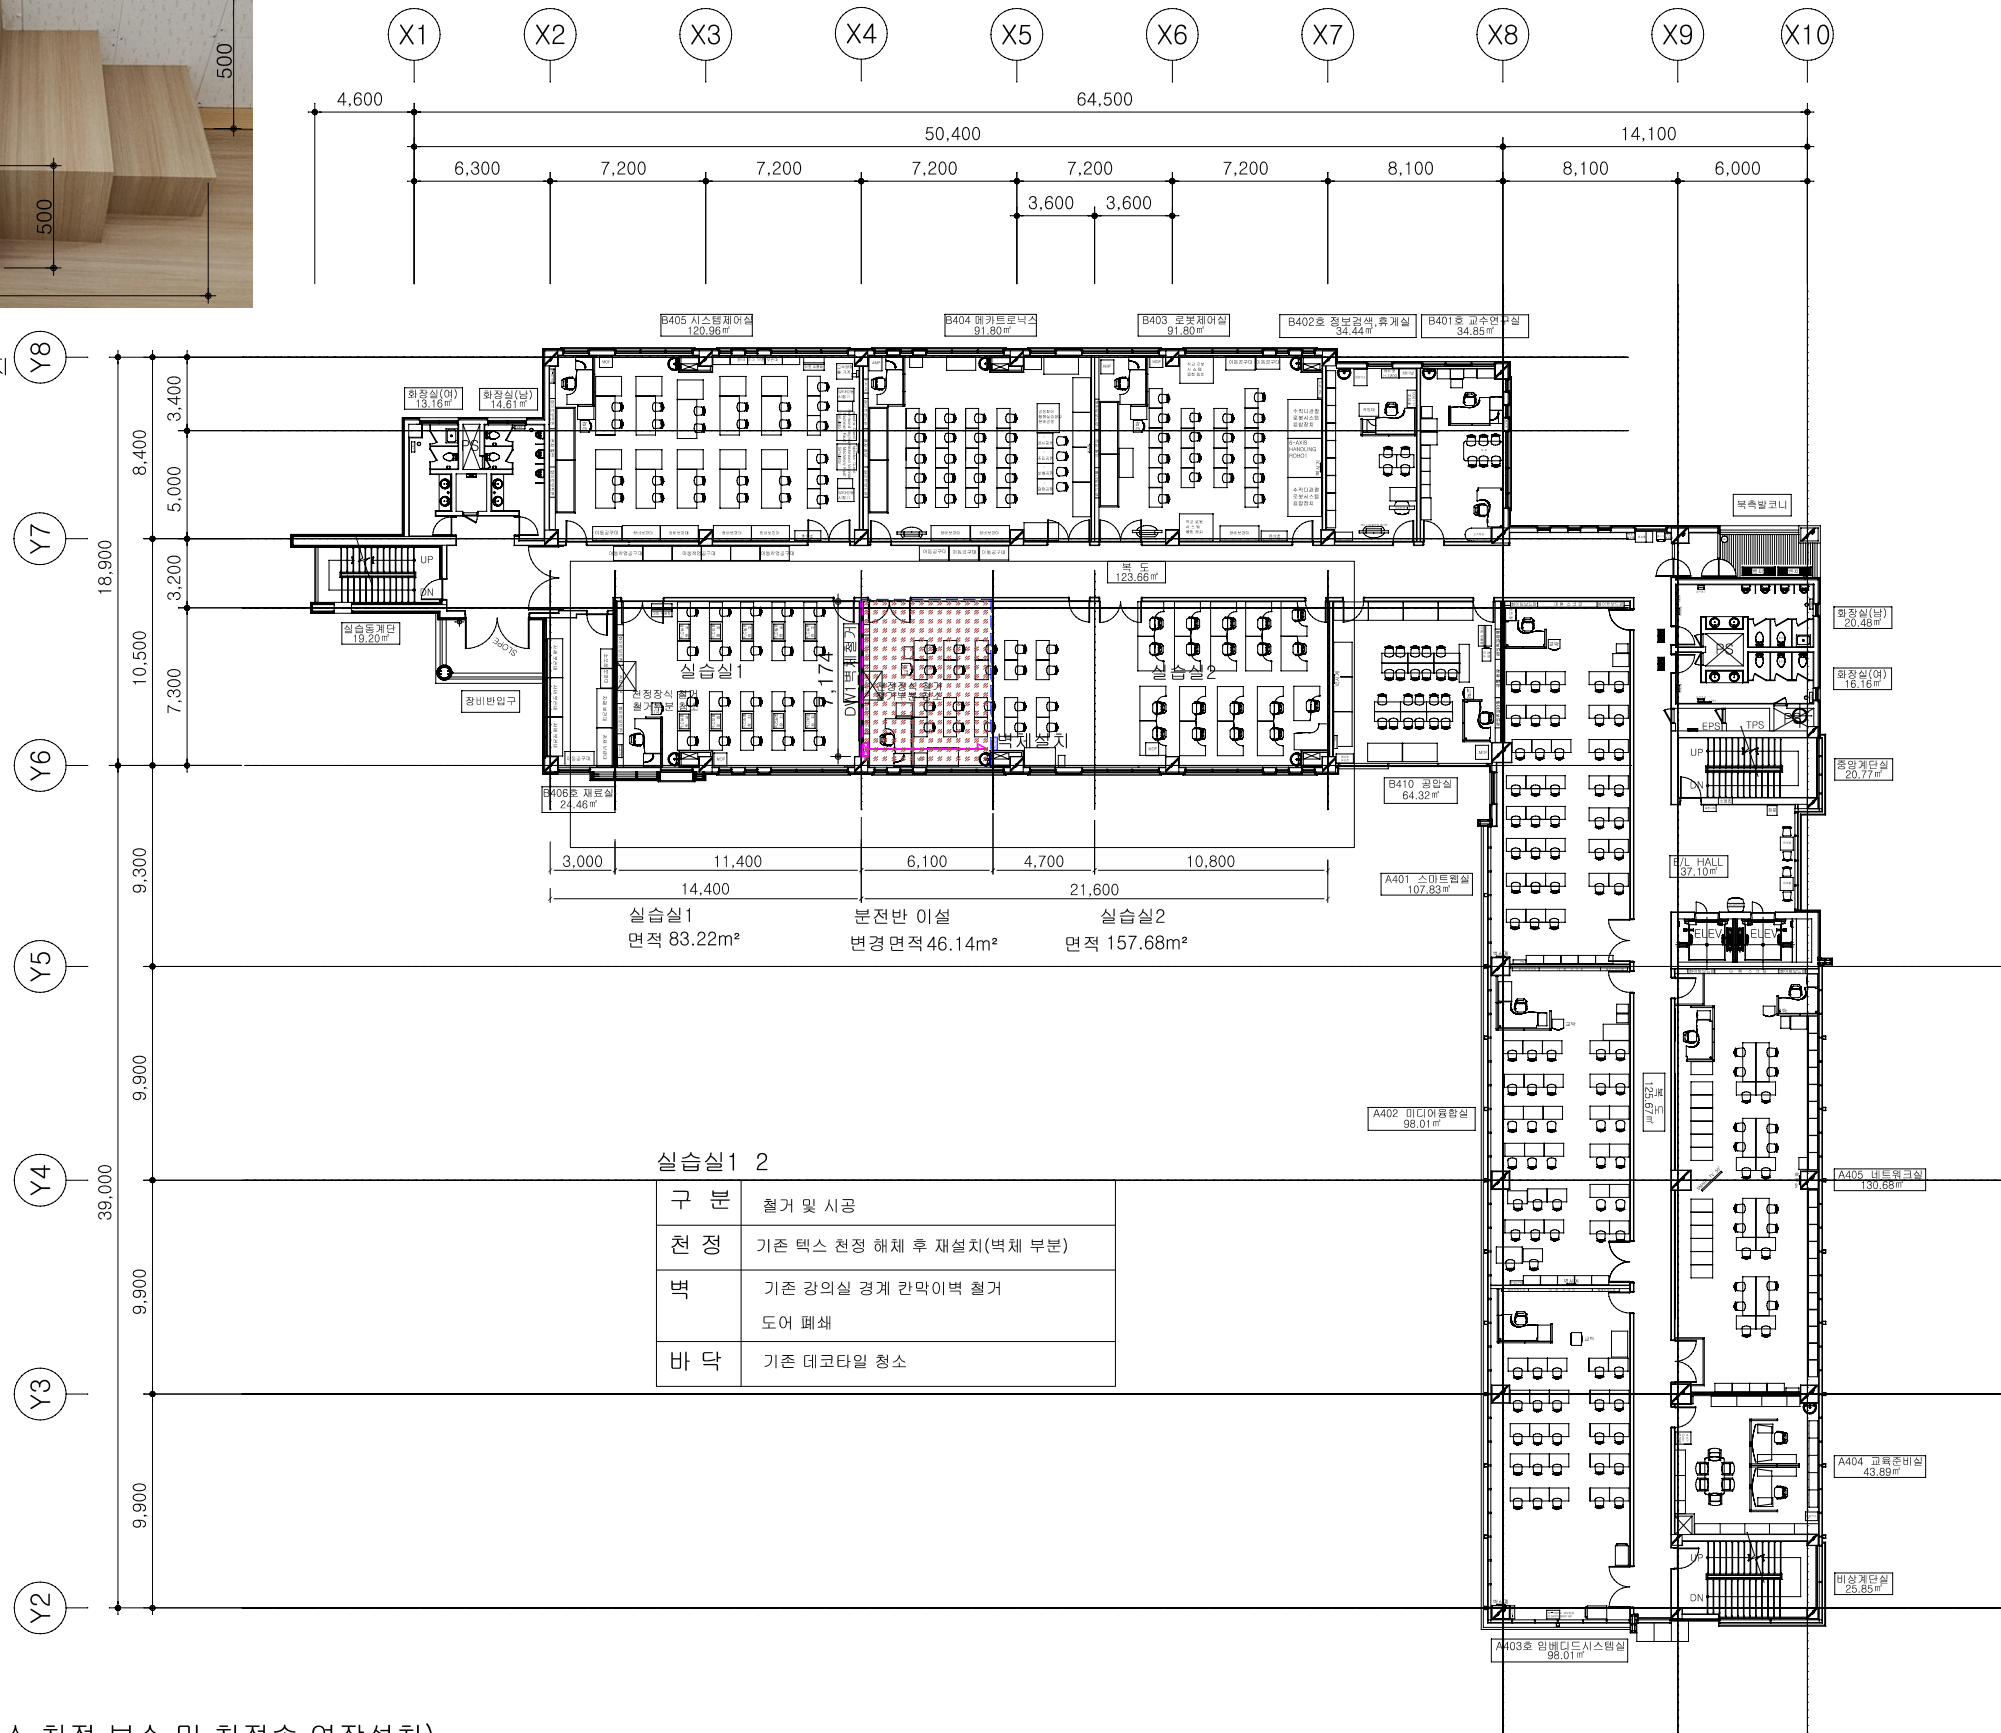

4층 공사 범위표

1. 칸막이벽 이설 (바닥청소,천정 보수 및 천정속 연장설치)
2. 분전반 이설 기능 변경 강의실1 ➔ 실습실
3. 조명등 S/W조정
4. 실습장 부스 설치
- 5.후로어 콘센트 전원 연결

기존 4층평면도

1/350

PROJECT TITLE



피지컬 시리빙센터 구축 공사

Date.

No. Revision

NOTE

Structure


Mechanical

Electrical

Fire Protection

Civil

Landscape

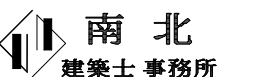

建築士 鄭 範 洙

전북 전주시 완산구 서신로57 7층

TEL : 063)247-7787

FAX : 063)247-7786

E-MAIL : nba2007@daum.net

SHEET TITLE

기존 4층평면도

DESIGN BY

SCALE

A3 1/350

CHECKED BY


DATE

APPROVED BY

SHEET NO.

SERIAL NO.

A- 405

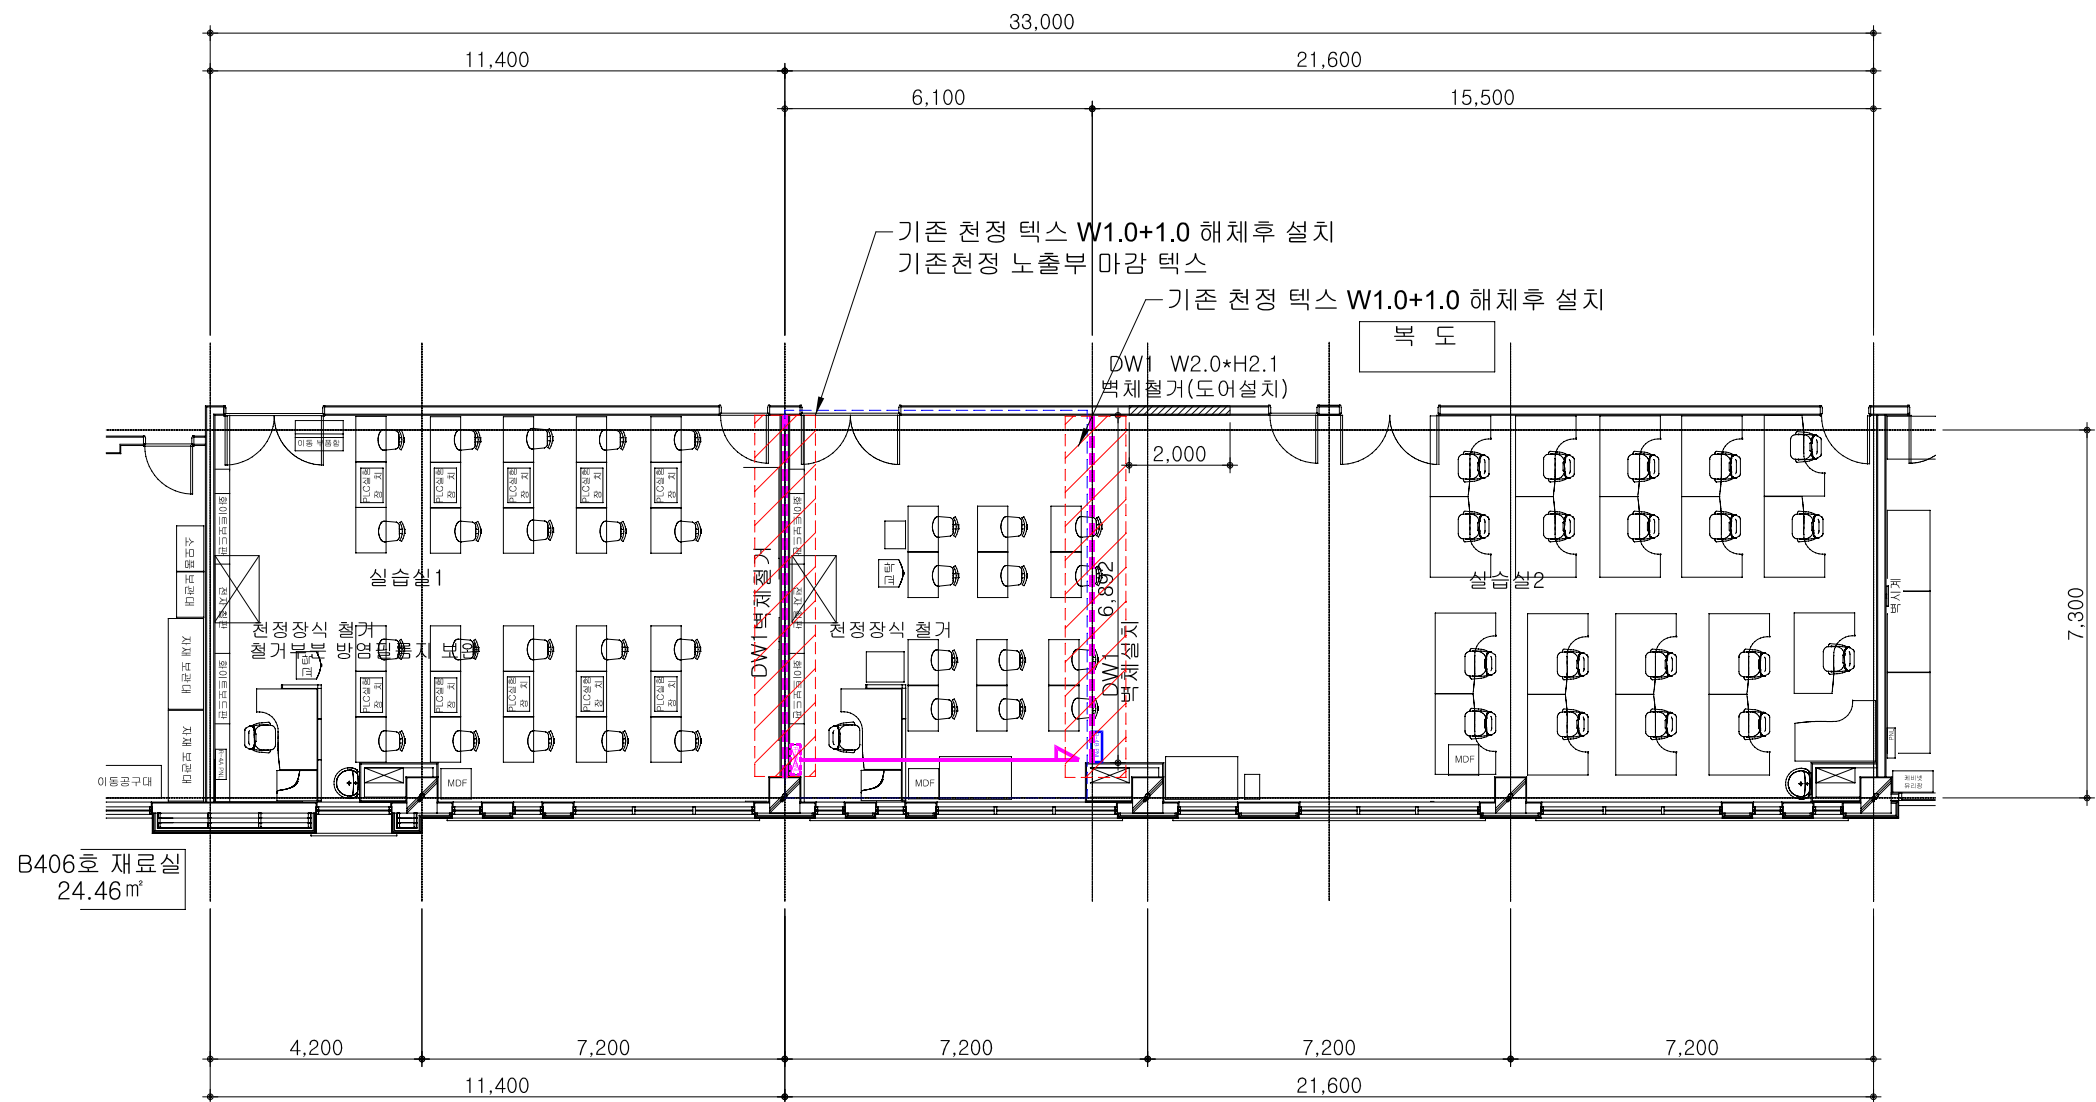

실습실1 2

구 분	철거 및 시공
천 정	기존 텍스 천정 해체 후 재설치(벽체 부분)
벽	기존 강의실 경계 칸막이벽 철거 도어 폐쇄
바 닥	기존 데코타일 청소

기존 4층 확대 평면도
1/150

PROJECT TITLE



피지컬 시리빙센터 구축 공사

Date.

No. Revision

-
-
-
-
-
-
-
-
-
-

NOTE

Structure


Mechanical

Electrical

Fire Protection

Civil

Landscape

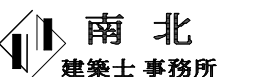

建築士 鄭 範 洙

전북 전주시 완산구 서신로57 7층

TEL : 063)247-7787

FAX : 063)247-7786

E-MAIL : nba2007@daum.net

SHEET TITLE

기존 4층 확대 평면도

DESIGN BY

SCALE

A3 1/150

CHECKED BY


DATE

APPROVED BY

SHEET NO.


SERIAL NO.

A- 406

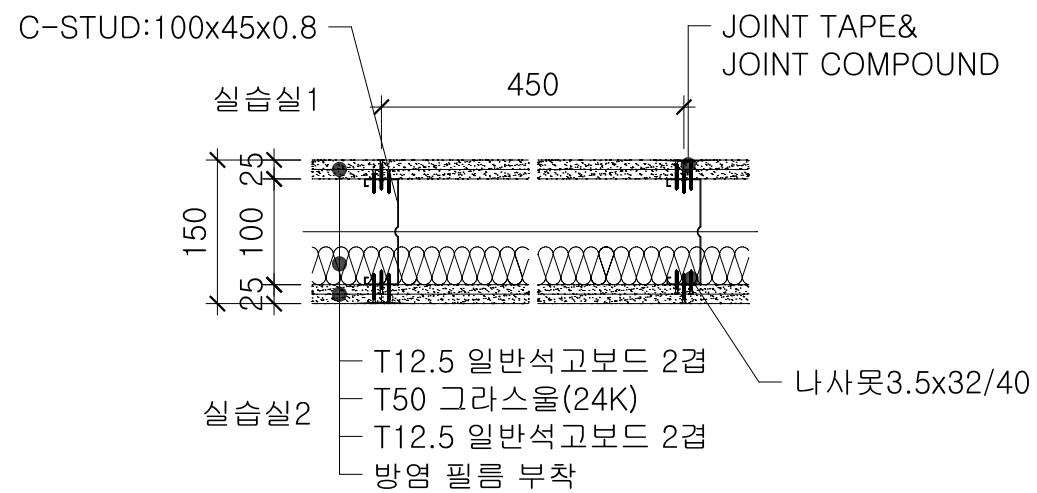

기존벽체 철거 W7.174*H3.3

DW1 평면도

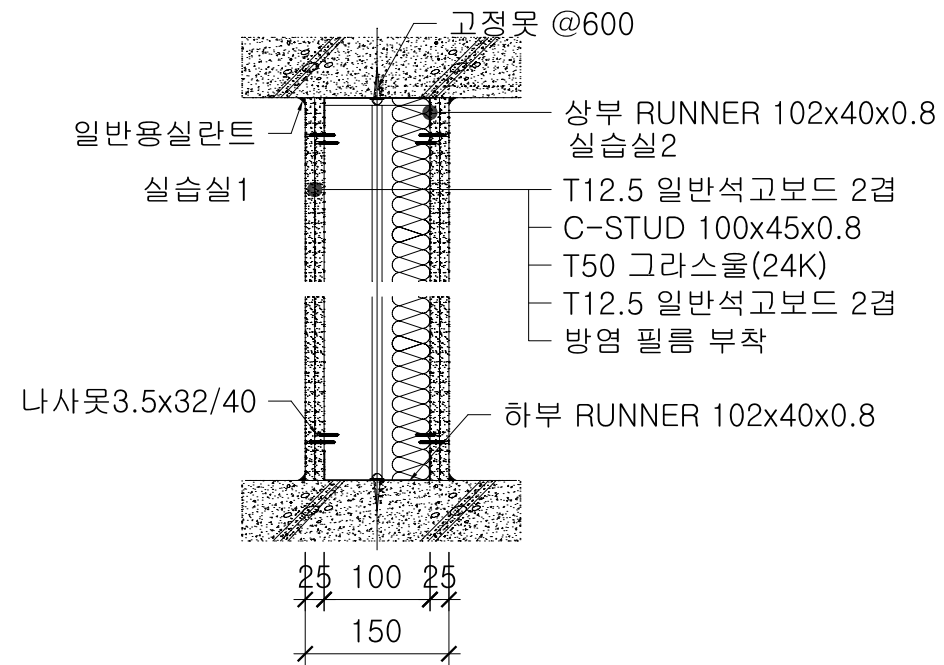

기존벽체 철거 W7.174*H3.3

DW1 단면도

PROJECT TITLE



피지컬 AI리빙센터 구축 공사

Date.

No. Revision

-

-

Structure


Mechanical

Electrical

Fire Protection

Civil

Landscape

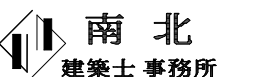

建築士 鄭 範 洙

전북 전주시 완산구 서신로57 7층

TEL : 063)247-7787

FAX : 063)247-7786

E-MAIL : nba2007@daum.net

SHEET TITLE

경량벽체 상세도2

DESIGN BY

SCALE

A3 1/100

CHECKED BY

DATE

APPROVED BY

SHEET NO.

SERIAL NO.

A- 407



PROJECT TITLE



피지컬 시리빙센터 구축 공사

Date.

No. Revision

-

-

-

-

-

-

-

-

-

-

NOTE

Structure


Mechanical

Electrical

Fire Protection

Civil

Landscape

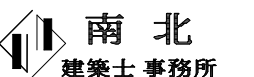

建築士 鄭 範 洙

전북 전주시 완산구 서신로57 7층

TEL : 063)247-7787

FAX : 063)247-7786

E-MAIL : nba2007@daum.net

SHEET TITLE

안내 전광판 이미지

DESIGN BY

SCALE

A3 1/30

CHECKED BY

DATE

APPROVED BY

SHEET NO.

SERIAL NO.

A- 500

안내 전광판 프레임 도면

안내 전광판 프레임 도면

TOP VIEW

창문 필름지 (기존 철거후 신규 설치)
W5.589*H1.4

스크린

422 4.810 398 5.630

40x40x1.4 각파이프 아연도

735

5.589

257

각각 4개소 기둥고정
M8 스텐 앵커볼트 L 50-100

FRONT VIEW

665 3.300 2.035 1.955 600

T12.5*2PL 석고보드 방염 필름지 마감(지정색) 디자인 협의 시공

스크린 설치공간

점검구

M8 스텐 앵커볼트 L 50-100 @1200

아연도 화스너 40*40*4T

525 580

T1.2 스텐판위 방염필름지(지정)

매립형손잡이

SIDE VIEW

1.400 5.589

창문 필름지 (기존 철거후 신규 설치)

실내 창문

텍스 천정

천정내부 보강 40x40x1.4 각파이프

T12.5*2PL 석고보드 방염 필름지 마감(지정색)

MDF 지정색

아연도 40x40x1.4 각파이프

MDF 지정색

기성품 카버 - 환기구 Ø200 색상 형태(원형 사각)협의시공

FL

걸레받이 세라민도장2회 H100

A- 501

안내 전광판 1


■ 피지컬 AI리빙센터 구축 공사

기계설비

2026.07



한국폴리텍대학
신기술교육원

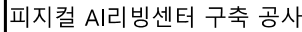

NOTE


 **南 北**
建築士事務所

建築士 鄭 範 洙

전북 전주시 완산구 서신로57 7층
TEL : 063)247-7787
FAX : 063)247-7786
E-MAIL : nba2007@daum.net

SHEET TITLE	
도면 목록표	
DESIGN BY	SCALE A3 : 1/ NONE
CHECKED BY	DATE
APPROVED BY	SHEET NO.
SERIAL NO.	M- 01

[illegible]

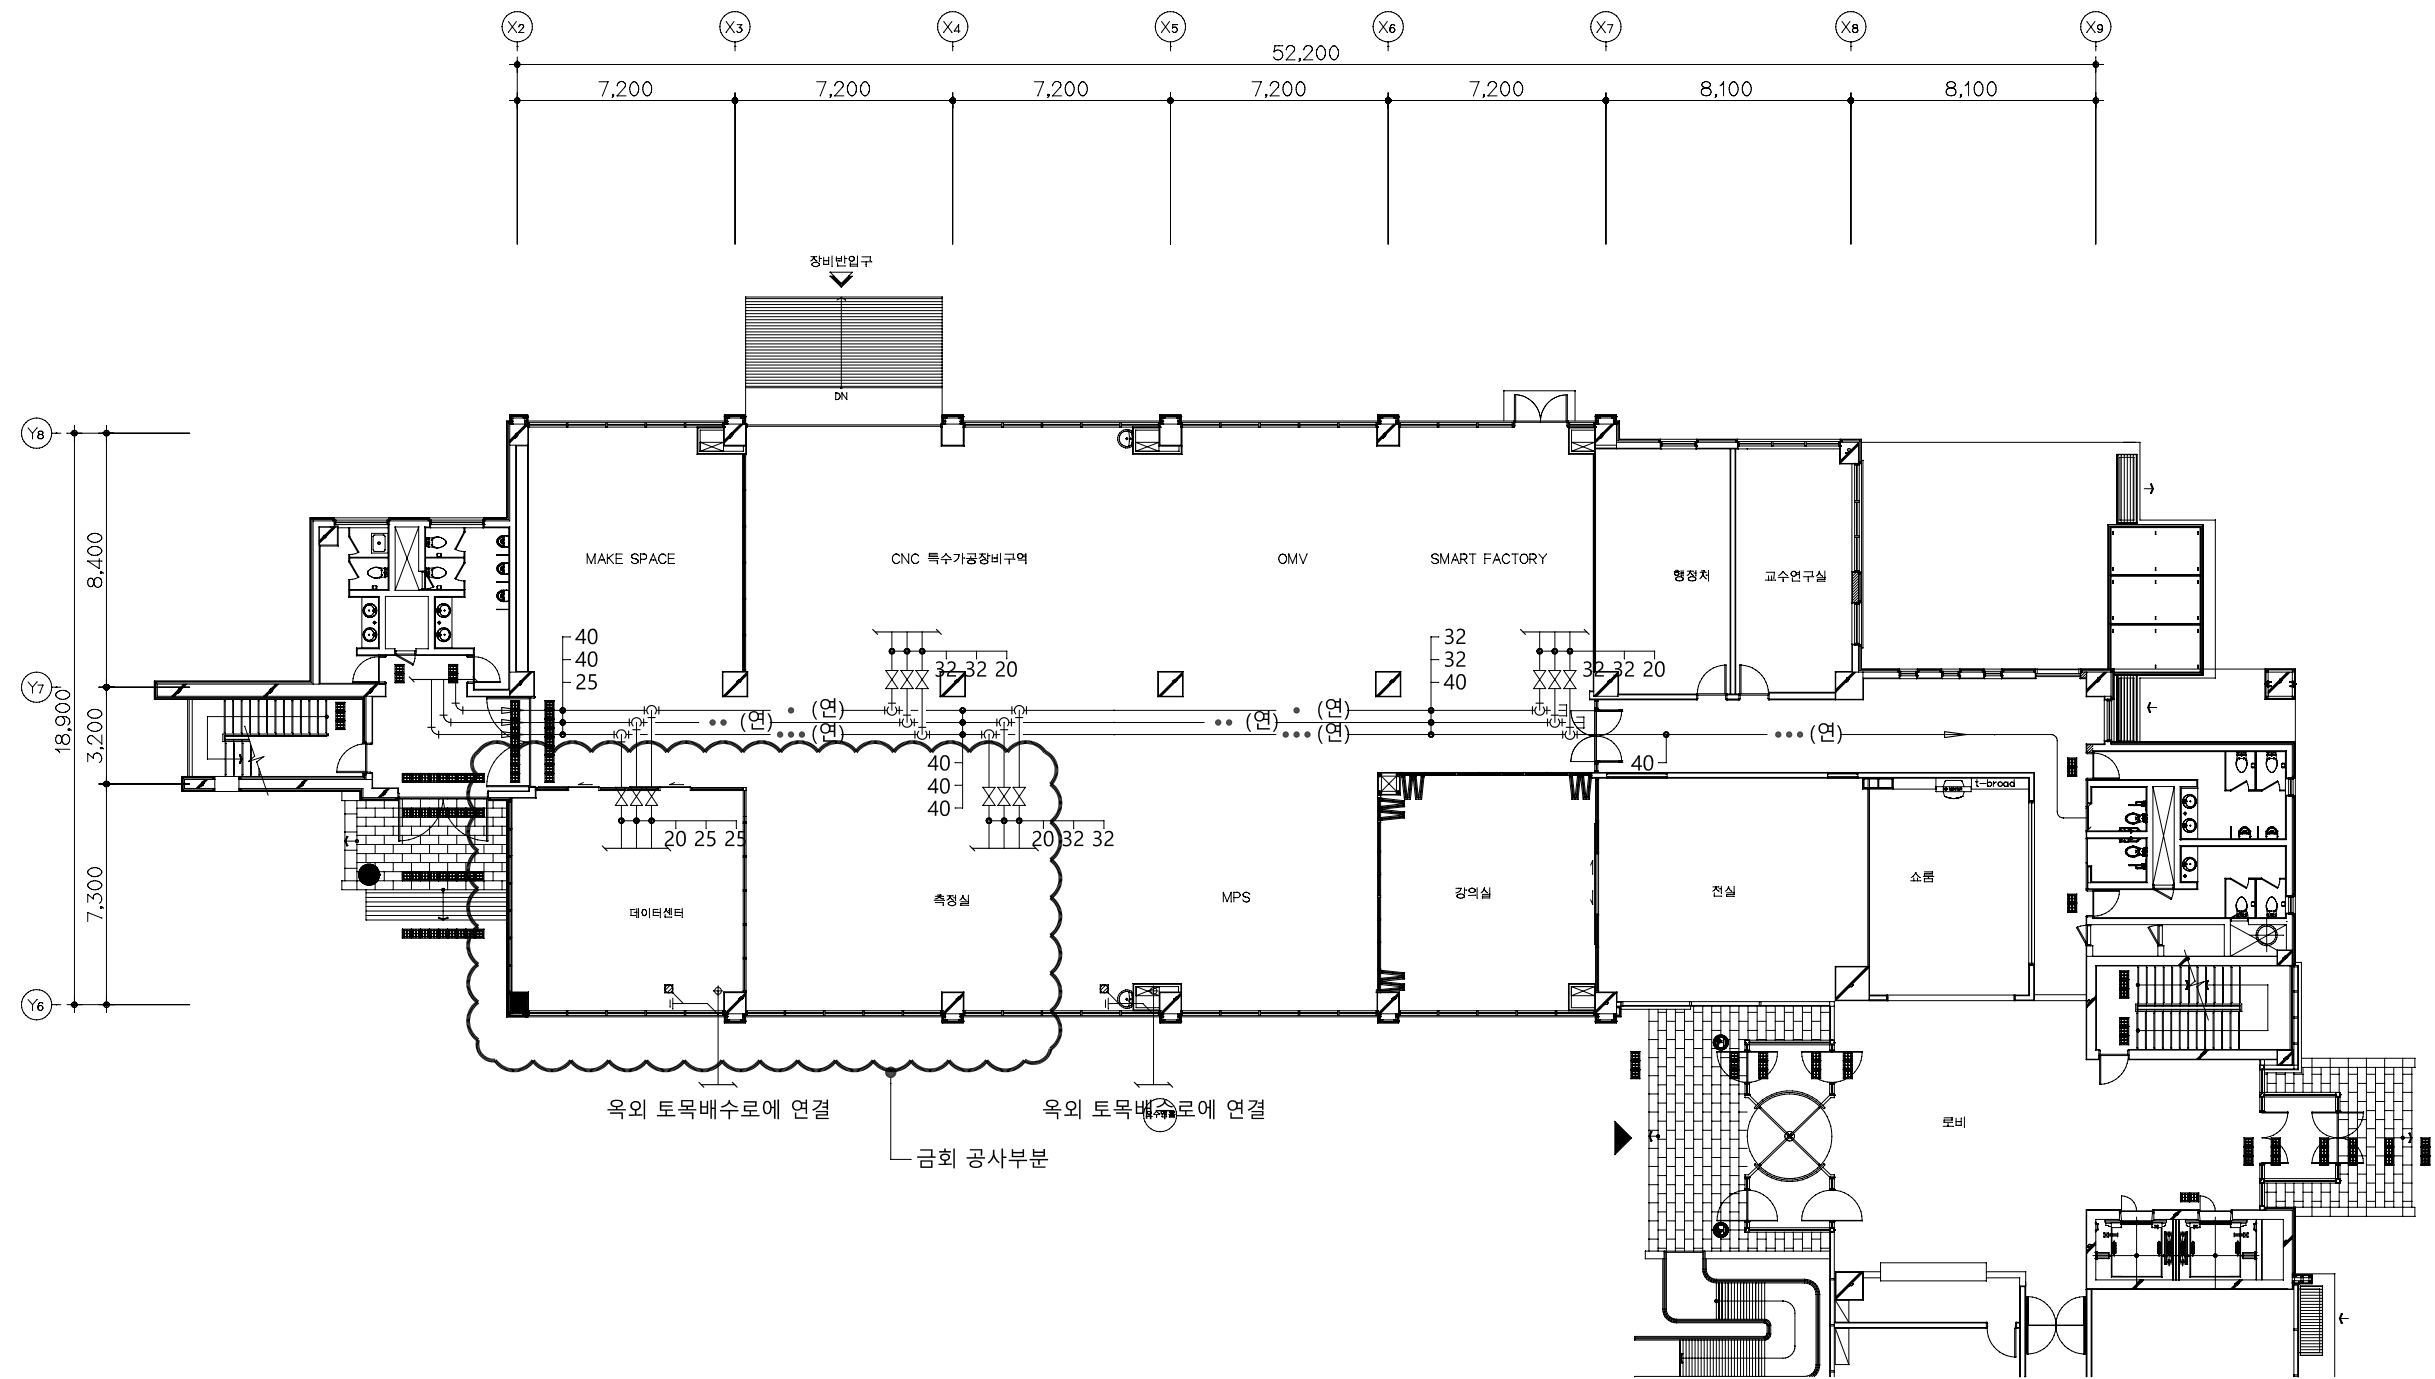

1 1층 위생배관 평면도- 변경전
SCALE= A3 : 1/ 250

PROJECT TITLE



피지컬 AI리빙센터 구축 공사

Date.

No.	Revision
-	-
-	-
-	-
-	-
-	-
-	-
-	-
-	-
-	-
-	-

NOTE

Structure


Mechanical

Electrical

Fire Protection

Civil

Landscape

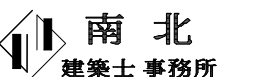

建築士 鄭 範 洙

전북 전주시 완산구 서신로57 7층

TEL : 063)247-7787

FAX : 063)247-7786

E-MAIL : nba2007@daum.net

SHEET TITLE

1층 위생배관 평면도- 변경전

DESIGN BY

SCALE

CHECKED BY


DATE

APPROVED BY

SHEET NO.

SERIAL NO.

M- 02

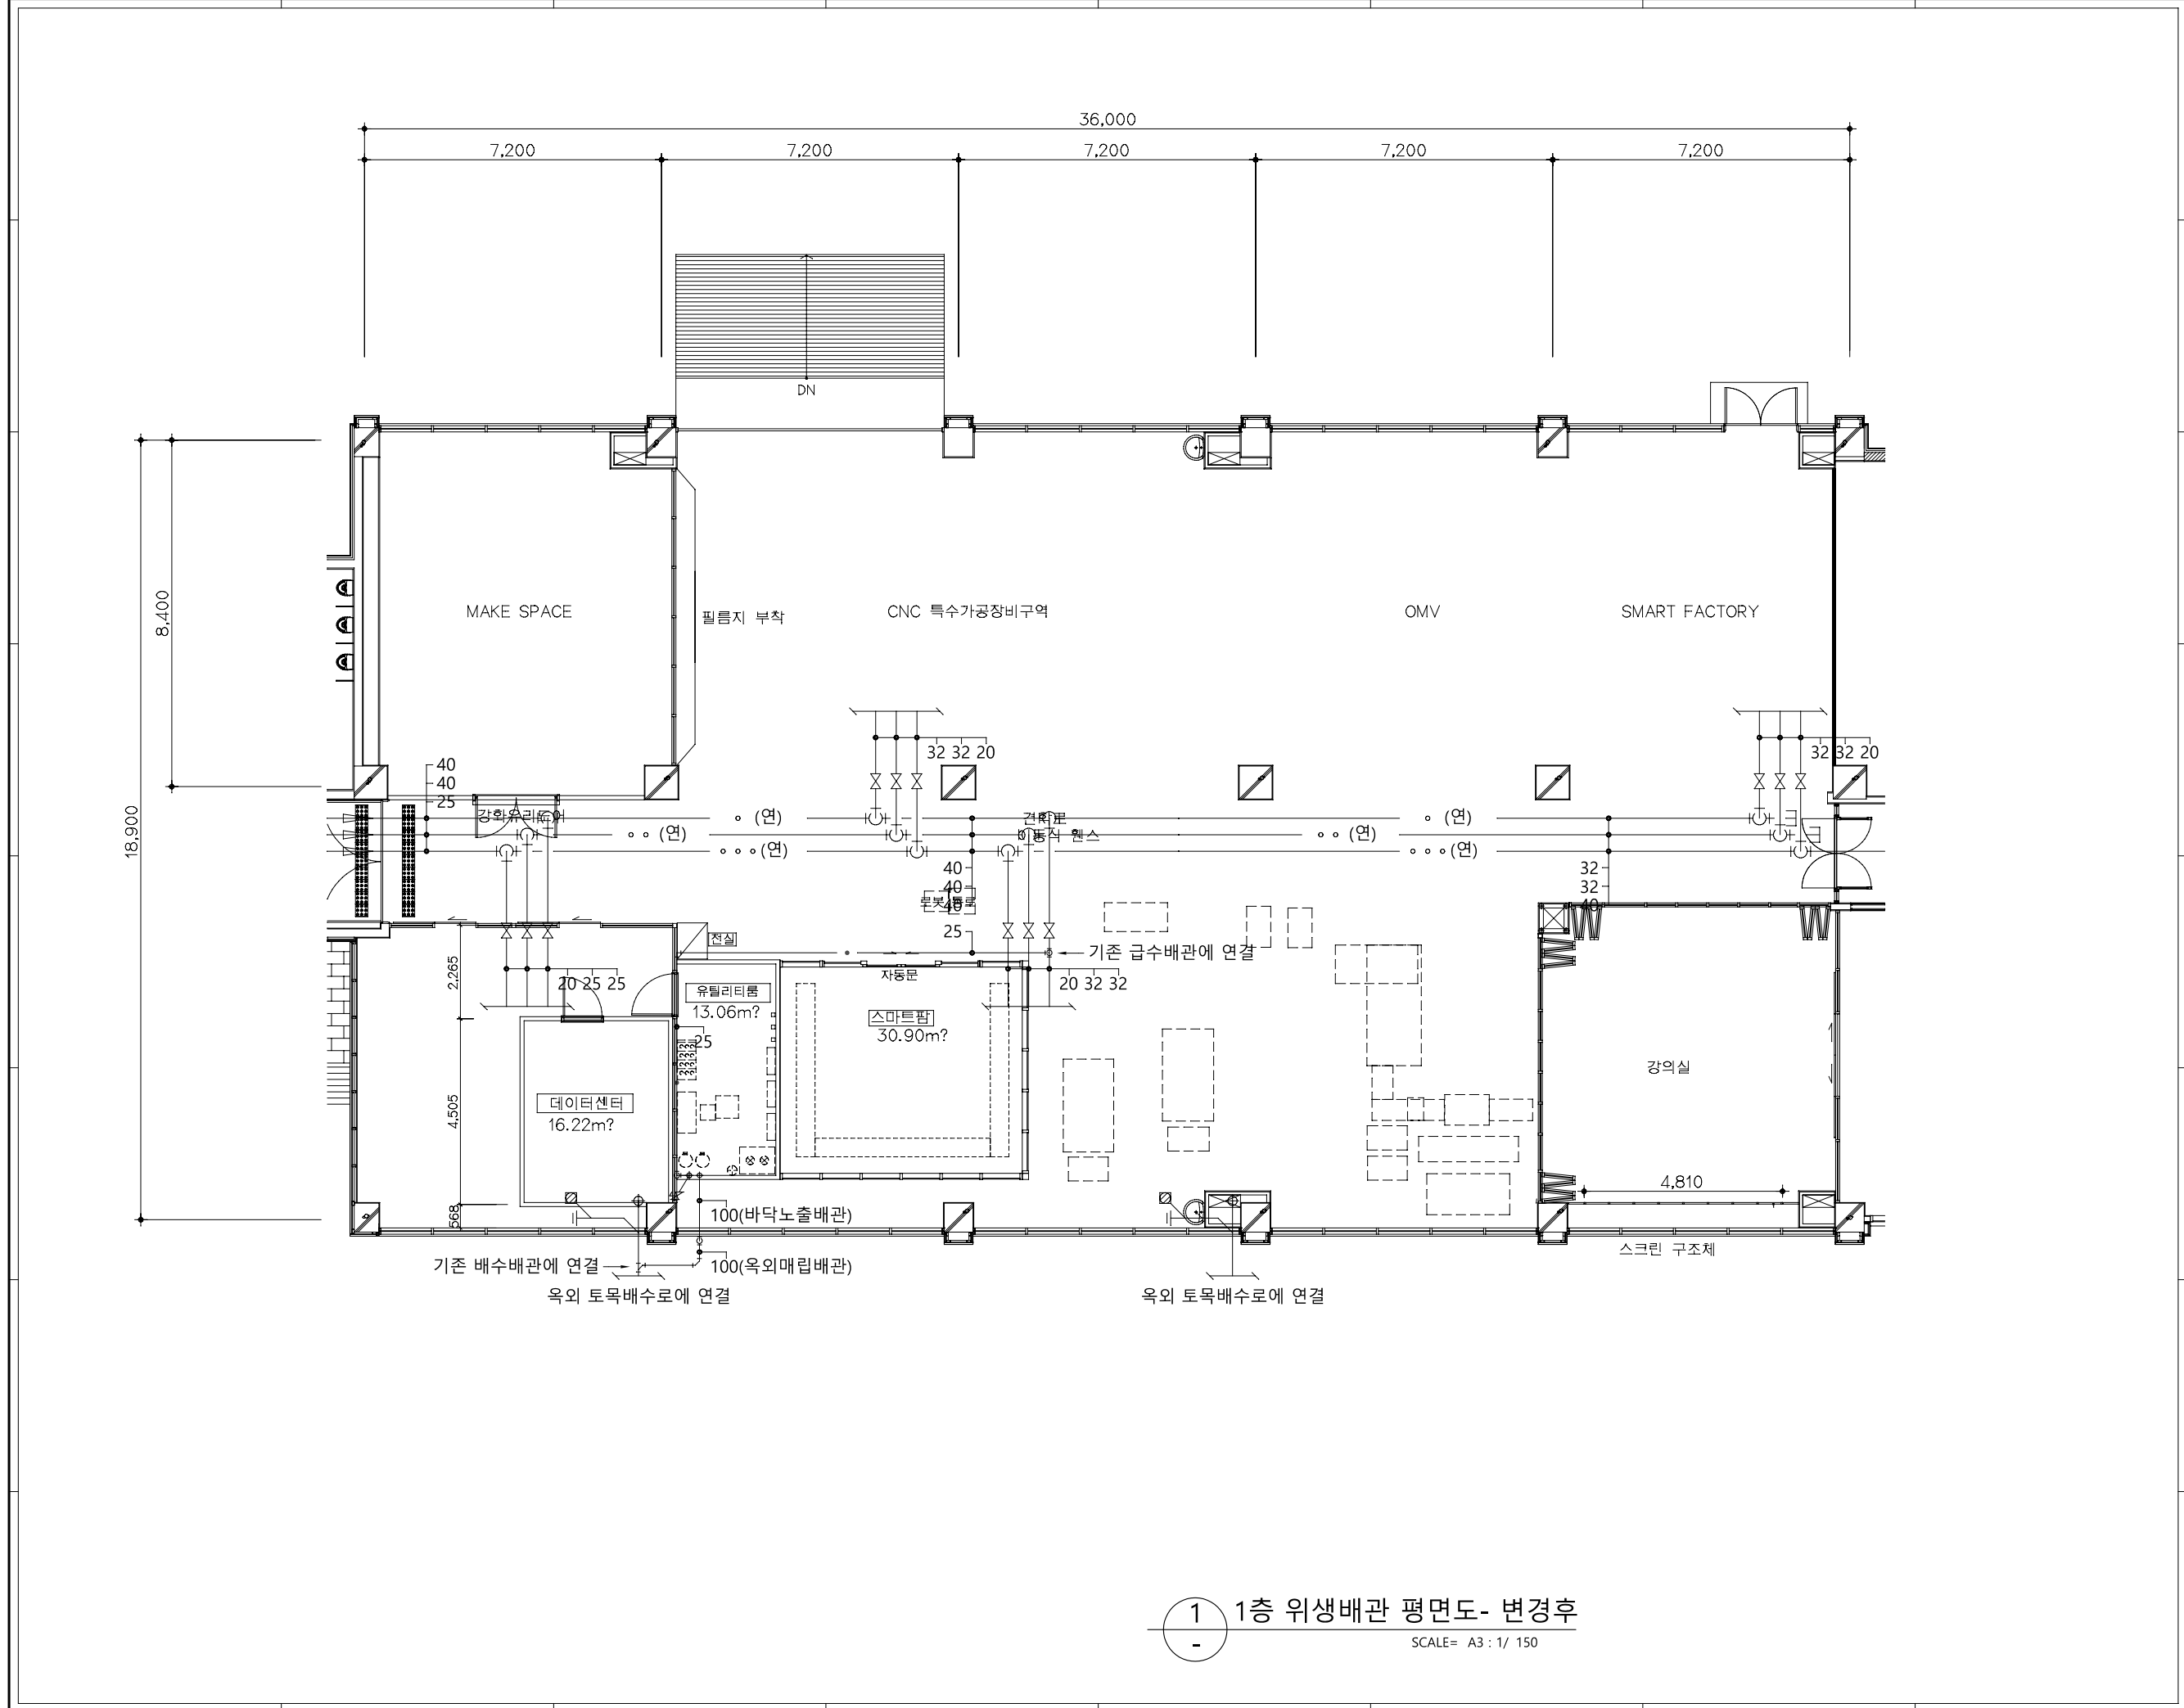

1 1층 위생배관 평면도- 변경후
SCALE= A3 : 1/ 150

PROJECT TITLE


피지컬 AI리빙센터 구축 공사

Date.

No.	Revision
-	-
-	-
-	-
-	-
-	-
-	-
-	-
-	-
-	-

NOTE

Structure

Mechanical

Electrical

Fire Protection

Civil

Landscape


 南北
建築士事務所
建築士 鄭 範 洙

전북 전주시 완산구 서신로57 7층
TEL : 063)247-7787
FAX : 063)247-7786
E-MAIL : nba2007@daum.net

SHEET TITLE

1층 위생배관 평면도- 변경후

DESIGN BY	SCALE A3 : 1/ 150
CHECKED BY	DATE
APPROVED BY	SHEET NO. M- 03
SERIAL NO.	

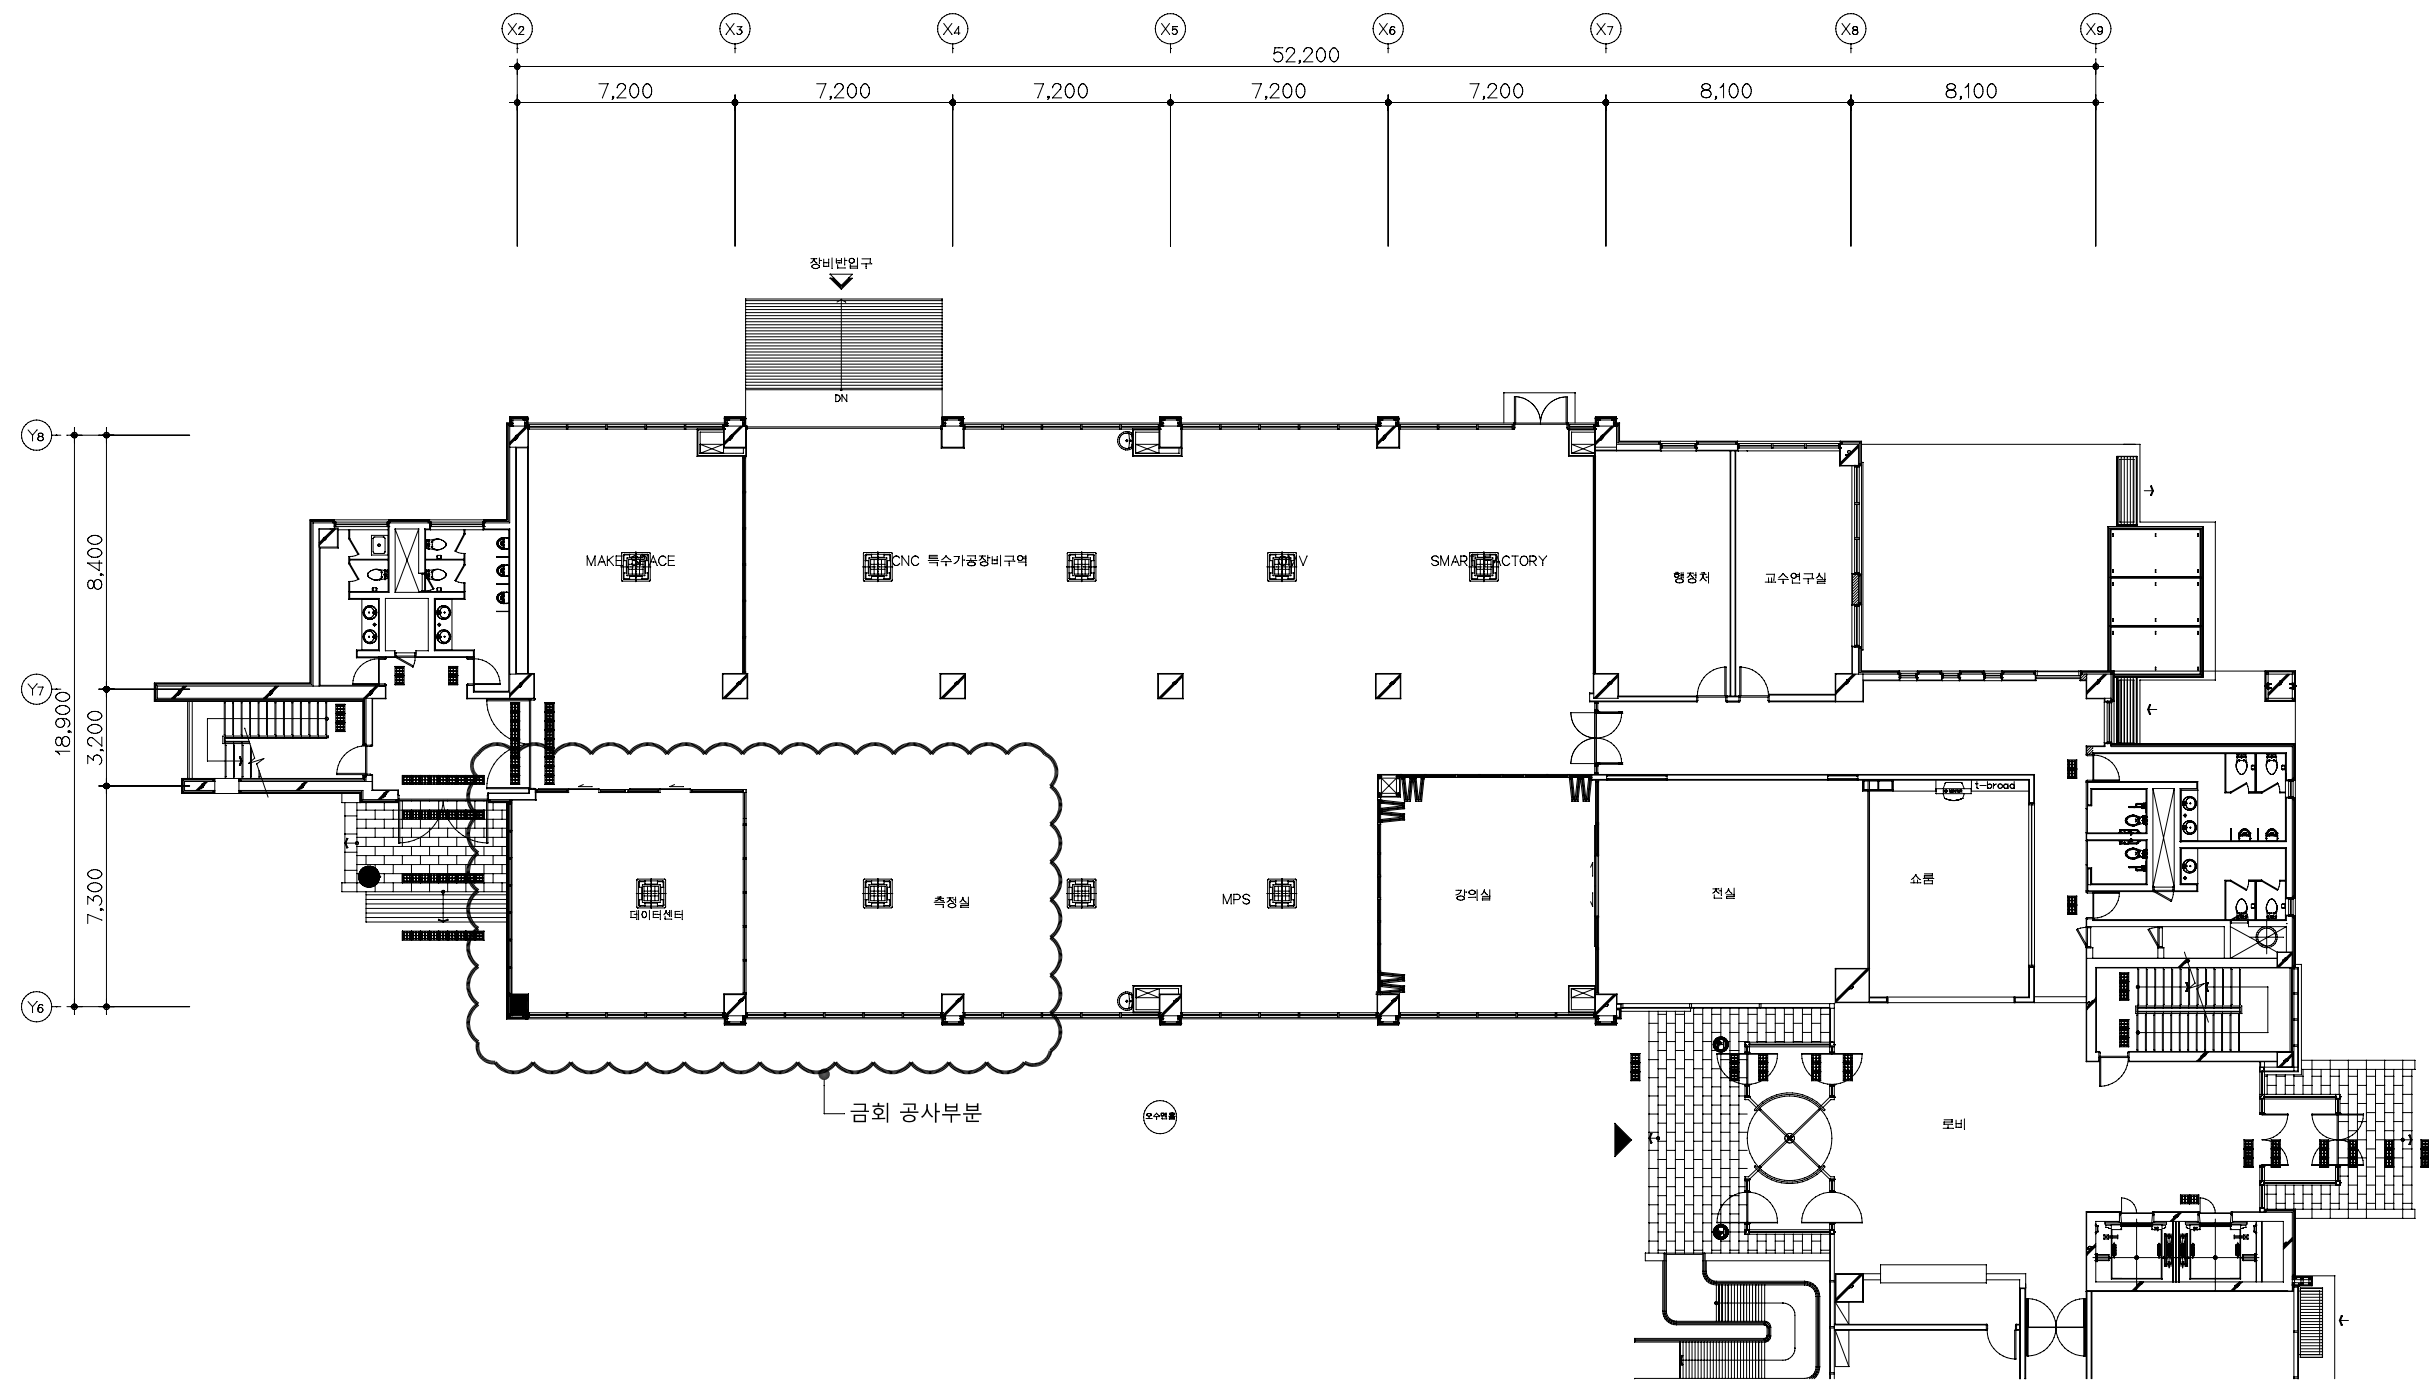

1 1층 냉난방기 평면도- 변경전
SCALE= A3 : 1/ 250

PROJECT TITLE



피지컬 AI리빙센터 구축 공사

Date.

No. Revision

-	
-	
-	
-	
-	
-	
-	
-	
-	
-	
-	

NOTE

Structure


Mechanical

Electrical

Fire Protection

Civil

Landscape

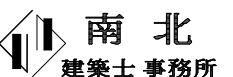

建築士 鄭 範 洙

전북 전주시 완산구 서신로57 7층

TEL : 063)247-7787

FAX : 063)247-7786

E-MAIL : nba2007@daum.net

SHEET TITLE

1층 냉난방기 평면도- 변경전

DESIGN BY

SCALE

A3 : 1/ 250

CHECKED BY


DATE

APPROVED BY

SHEET NO.


SERIAL NO.

M- 04

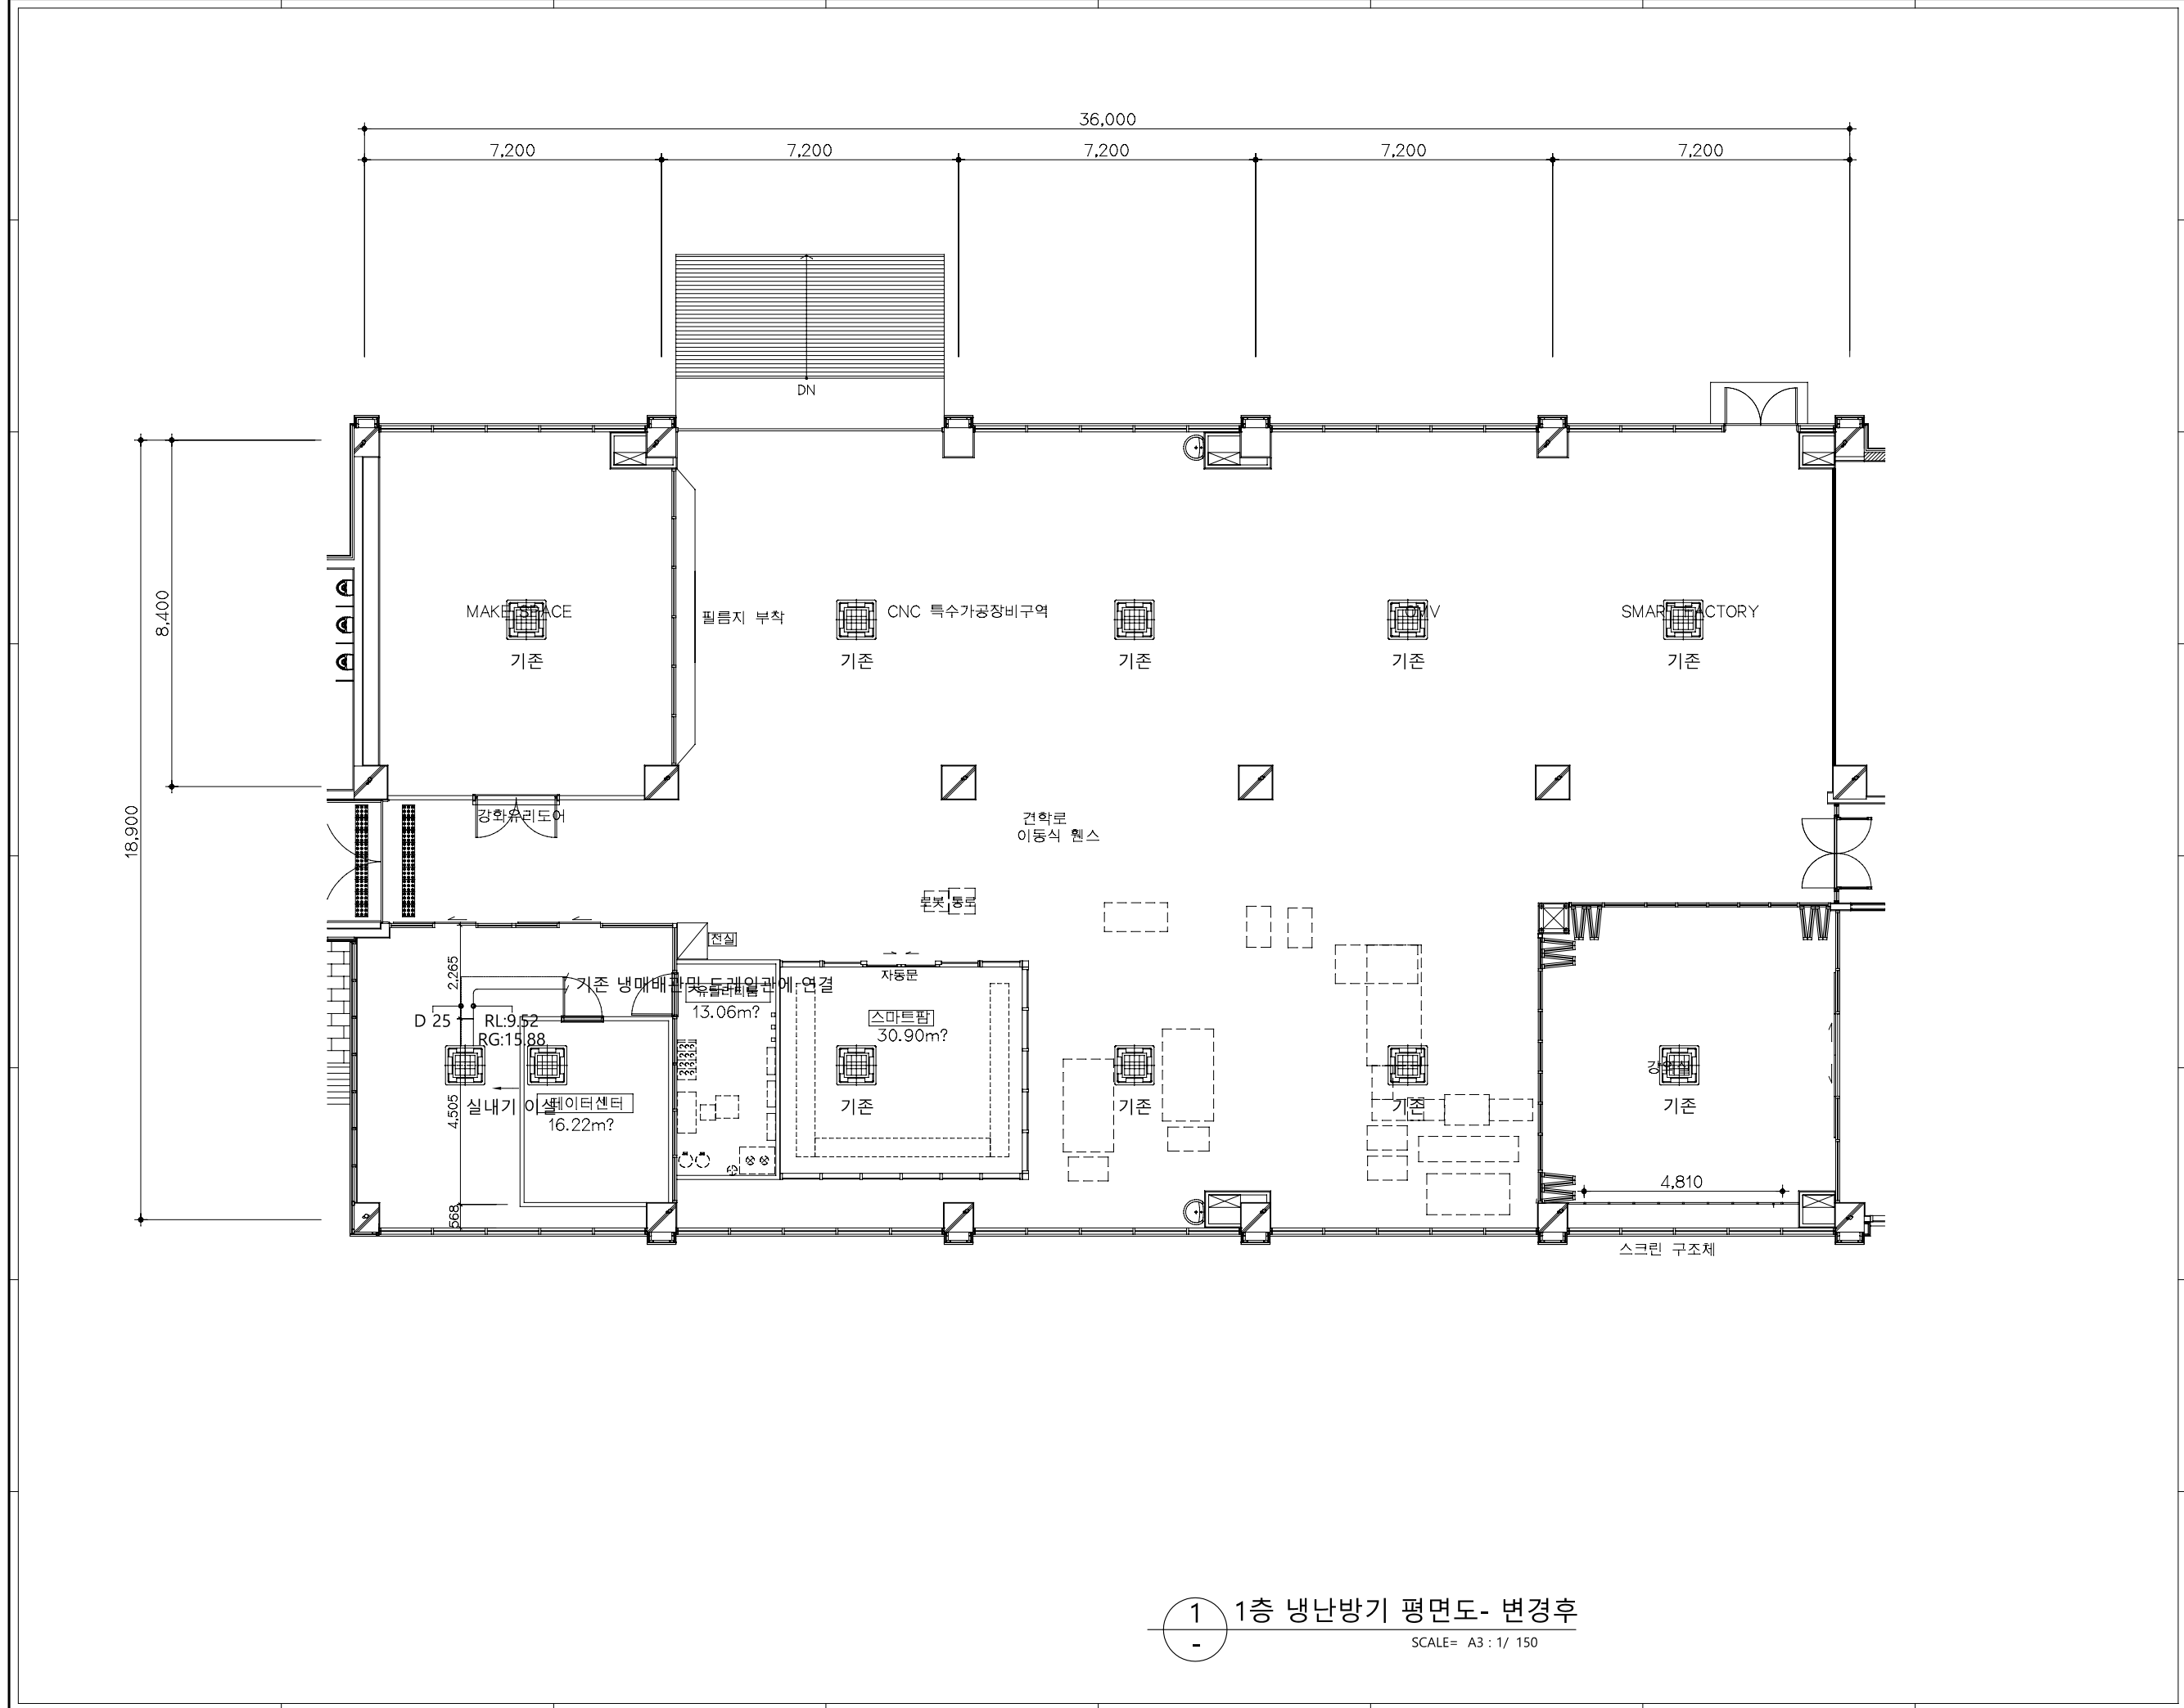

1 1층 냉난방기 평면도- 변경후
SCALE= A3 : 1/ 150

PROJECT TITLE	
피지컬 AI리빙센터 구축 공사	
Date.	
No.	Revision
-	-
-	-
-	-
-	-
-	-
-	-
-	-
-	-
-	-
NOTE	
Structure	
Mechanical	
Electrical	
Fire Protection	
Civil	
Landscape	
南北 建築士事務所 전북 전주시 완산구 서신로57 7층 TEL : 063)247-7787 FAX : 063)247-7786 E-MAIL : nba2007@daum.net	
SHEET TITLE	
1층 냉난방기 평면도- 변경후	
DESIGN BY	SCALE A3 : 1/ 150
CHECKED BY	DATE
APPROVED BY	SHEET NO.
SERIAL NO.	M- 05

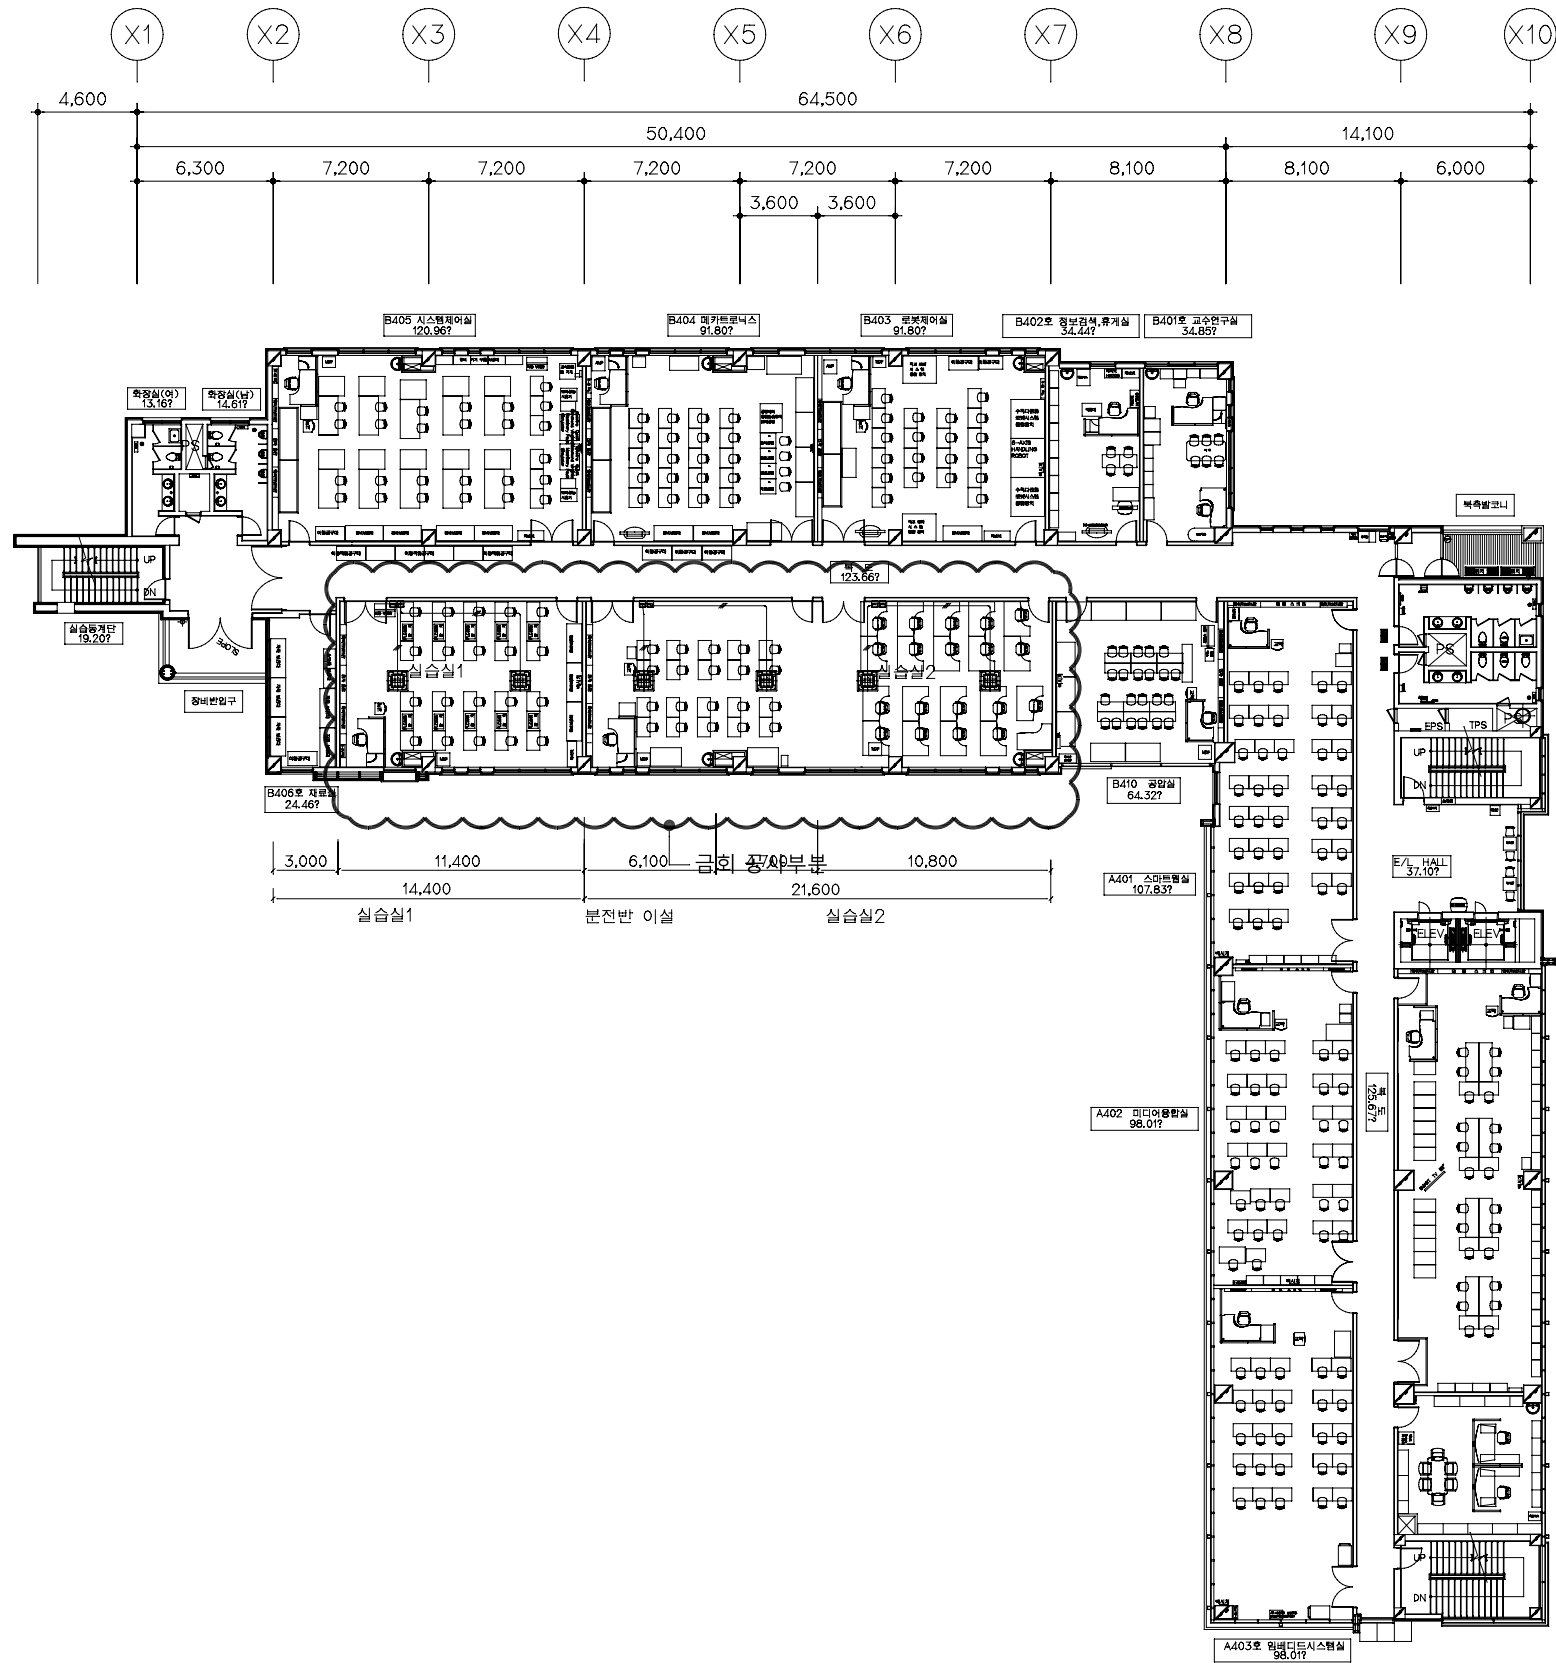

1 4층 냉난방기 평면도- 변경전
- SCALE= A3 : 1/ 350

PROJECT TITLE



피지컬 A리빙센터 구축 공사

Date.

No.	Revision
-	-
-	-
-	-
-	-
-	-
-	-
-	-
-	-
-	-
-	-

NOTE

Structure


Mechanical

Electrical

Fire Protection

Civil

Landscape

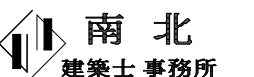

建築士 鄭 範 洙

전북 전주시 완산구 서신로57 7층

TEL : 063)247-7787

FAX : 063)247-7786

E-MAIL : nba2007@daum.net

SHEET TITLE

4층 냉난방기 평면도- 변경전

DESIGN BY

SCALE

CHECKED BY


DATE

APPROVED BY

SHEET NO.

SERIAL NO.

M- 06

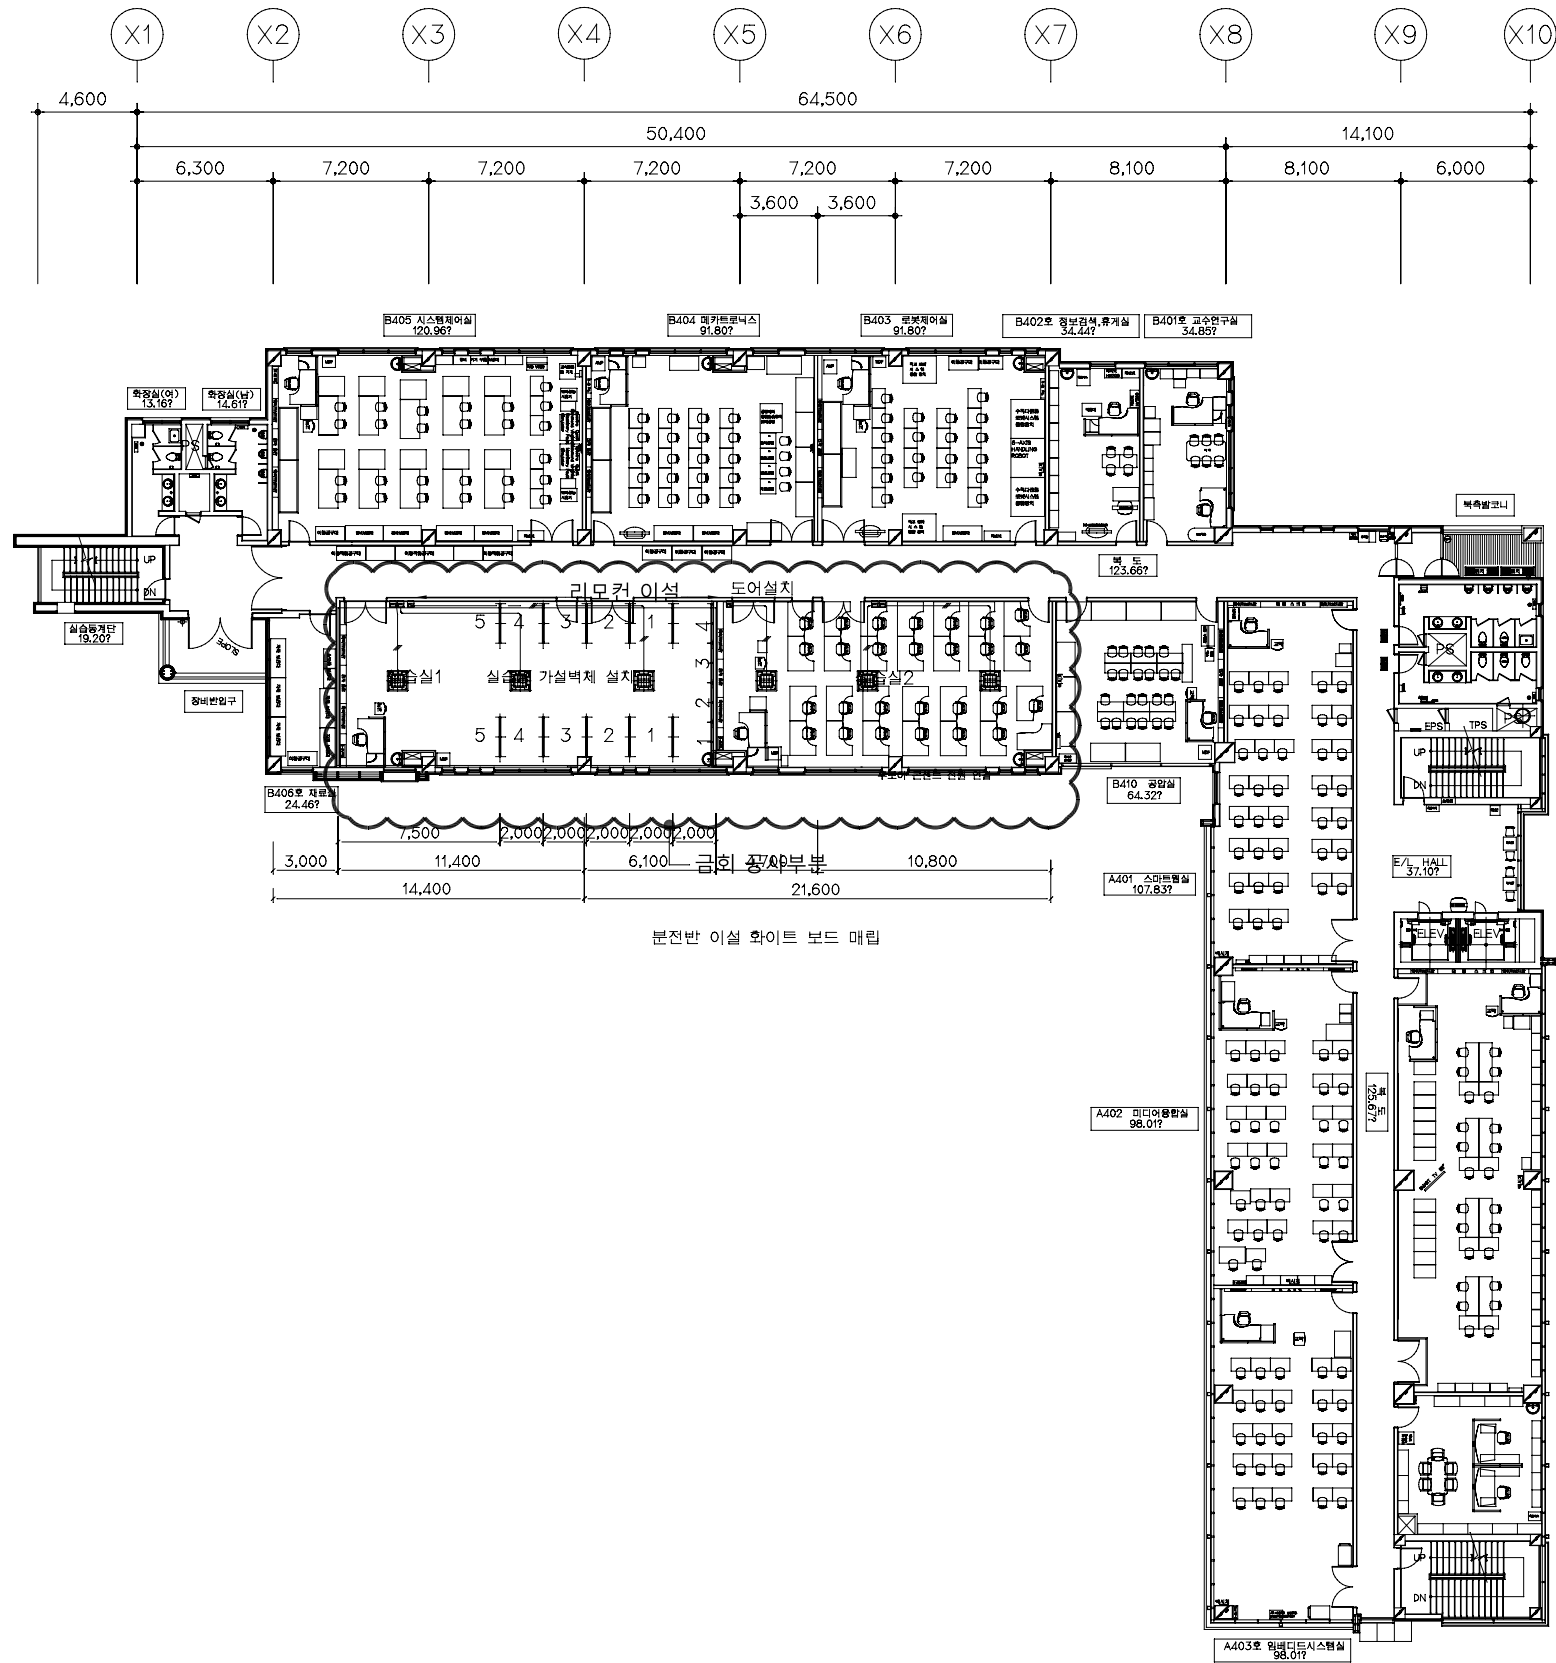

PROJECT TITLE



피지컬 이리빙센터 구축 공사

Date.

No.	Revision
-	-
-	-
-	-
-	-
-	-
-	-
-	-
-	-
-	-
-	-

NOTE

Structure


Mechanical

Electrical

Fire Protection

Civil

Landscape

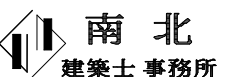

建築士 鄭 範 洙

전북 전주시 완산구 서신로57 7층

TEL : 063)247-7787

FAX : 063)247-7786

E-MAIL : nba2007@daum.net

SHEET TITLE

4층 냉난방기 평면도- 변경후

DESIGN BY

SCALE

A3 : 1/ 350

CHECKED BY

DATE

APPROVED BY

SHEET NO.

SERIAL NO.

M- 07